



ОБЩЕСТВО С ОГРАНИЧЕННОЙ ОТВЕТСТВЕННОСТЬЮ  
«ЗАБТРАНСПРОЕКТ»

Свидетельство № 1ГМС-3 9 от 7 марта 2017 г.

СРО-И-032-22122011

## ТЕХНИЧЕСКИЙ ПАСПОРТ

железнодорожного пути  
необщего пользования  
АО «Читаглавснаб»

*Путь №ГМС-3*

ст. Чита-1

2504-ТП

Ведущий инженер  
ООО «Забтранспроект»

Егиазарян Н.А.

Инженер  
ООО «Забтранспроект»

Городний К.А.

Чита,

2025

|              |         |
|--------------|---------|
| Взам. Инв. № |         |
| Подп. и дата |         |
| Инв. № подл. | 2504-ТП |

## ОБЩИЕ СВЕДЕНИЯ

Место примыкания железнодорожного пути необщего пользования:

*железнодорожный путь необщего пользования №ГМС-3 АО «Читаглавснаб» примыкает стрелочным переводом СП132 к железнодорожному пути необщего пользования №1 Базы №2 ПЧМ Чита*

Границы железнодорожного пути необщего пользования:

*сигнальный знак «Граница пути необщего пользования» (ПК0+32,98), установленный на расстоянии 32,98м от переднего стыка рамного рельса стрелочного перевода №132.*

Наличие предохранительных устройств:

*нет*

Дата заключения договора на эксплуатацию железнодорожного пути необщего пользования и срок его действия:

Порядок подачи и уборки вагонов (кем производится – железной дорогой, средствами предприятия или маневровым порядком), серия локомотива, применяемого при подаче и уборке вагонов:

*подача и уборка вагонов на путь необщего пользования №ГМС-3 АО «Читаглавснаб» осуществляется маневровым порядком локомотивами серии ТЭМ2, ТЭМ18 ст. Чита-1 Забайкальской железной дороги.*

|              |  |
|--------------|--|
| Взам. Инв. № |  |
| Подп. и дата |  |
| Инв. №подл.  |  |

|            |           |      |        |       |      |   |
|------------|-----------|------|--------|-------|------|---|
|            |           |      |        |       |      |   |
| Изм.       | Коп.уч.   | Лист | № док. | Подп. | Дата | <div style="font-size: 1.2em; font-weight: bold;">2504– ТП</div> <div style="margin-top: 20px;"> Технический паспорт<br/>железнодорожного пути необщего<br/>пользования<br/>АО «Читаглавснаб» </div> |
| Разработал | Городний  |      |        |       |      |   |
| Проверил   | Егиазарян |      |        |       |      |   |
|            |           |      |        |       |      |   |
|            |           |      |        |       |      |   |

|                      |      |        |
|----------------------|------|--------|
| Стадия               | Лист | Листов |
|                      | 1    | 12     |
| ООО «Забтранспроект» |      |        |

# 1 ХАРАКТЕРИСТИКА ПУТИ

**Таблица 1.1 – Примыкания других железнодорожных путей к железнодорожным путям предприятия**

| Наименование предприятия | Место примыкания (пикет, стрелка) | Длина путей км. | Предприятие обслуживающее путь необщего пользования |
|--------------------------|-----------------------------------|-----------------|-----------------------------------------------------|
|--------------------------|-----------------------------------|-----------------|-----------------------------------------------------|

**Таблица 1.2 - Ведомость железнодорожных путей предприятия**

| № пути | Граница путей                              |                   | Специализация          | Дата внесения изменений | Ф.И.О. должность внесшего изменения | Подпись |
|--------|--------------------------------------------|-------------------|------------------------|-------------------------|-------------------------------------|---------|
|        | от                                         | до                |                        |                         |                                     |         |
| ГМС-3  | Знак ГПП<br>АО «Читаглавснаб»<br>ПК0+32,98 | Упор<br>ПК5+19,77 | Погрузочно-выгрузочный | 03.2025                 | Егиазарян Н.А.                      |         |

**Таблица 1.3 – Данные по длине путей**

| № пути       | Граница путей                              |                   | Длины путей, м |               | Дата внесения изменений | Ф.И.О. должность внесшего изменения | Подпись |
|--------------|--------------------------------------------|-------------------|----------------|---------------|-------------------------|-------------------------------------|---------|
|              | от                                         | до                | полная         | полезная      |                         |                                     |         |
| ГМС-3        | Знак ГПП<br>АО «Читаглавснаб»<br>ПК0+32,98 | Упор<br>ПК5+19,77 | 486,79         | 463,31        | 03.2025                 | Егиазарян Н.А.                      |         |
| <b>ИТОГО</b> |                                            |                   | <b>486,79</b>  | <b>463,31</b> |                         |                                     |         |

|               |              |              |
|---------------|--------------|--------------|
| Инва. № подл. | Подп. и дата | Взам. Инв. № |
| 2504-ТП       |              |              |

|      |         |      |        |       |      |           |      |
|------|---------|------|--------|-------|------|-----------|------|
| Изм. | Кол.уч. | Лист | № док. | Подп. | Дата | 2504 – ТП | Лист |
|      |         |      |        |       |      |           | 2    |

## 2 НИЖНЕЕ СТРОЕНИЕ ПУТИ И ИСКУССТВЕННЫЕ СООРУЖЕНИЯ

**Таблица 2.1 – Наличие насыпей или выемок**

| № пути | Граница путей                               |                   | Наличие насыпей право/лево | Дата внесения изменений | Ф.И.О. должность внесшего изменения | Подпись |
|--------|---------------------------------------------|-------------------|----------------------------|-------------------------|-------------------------------------|---------|
|        | от пикета                                   | до пикета         |                            |                         |                                     |         |
| ГМС-3  | Знак ГПНП<br>АО «Читаглавснаб»<br>ПК0+32,98 | Упор<br>ПК5+19,77 | нет                        | 03.2025                 | Егиазарян<br>Н.А.                   |         |

**Таблица 2.2 – Наличие водоотводных сооружений**

| № пути | Граница путей                               |                   | Водоотводное устройство право/лево | Дата внесения изменений | Ф.И.О. должность внесшего изменения | Подпись |
|--------|---------------------------------------------|-------------------|------------------------------------|-------------------------|-------------------------------------|---------|
|        | от пикета                                   | до пикета         |                                    |                         |                                     |         |
| ГМС-3  | Знак ГПНП<br>АО «Читаглавснаб»<br>ПК0+32,98 | Упор<br>ПК5+19,77 | нет                                | 03.2025                 | Егиазарян<br>Н.А.                   |         |

**Таблица 2.3 – Деформация земляного полотна**

| № пути | Граница путей                               |                   | Тип деформации право/лево | Дата внесения изменений | Ф.И.О. должность внесшего изменения | Подпись |
|--------|---------------------------------------------|-------------------|---------------------------|-------------------------|-------------------------------------|---------|
|        | от пикета                                   | до пикета         |                           |                         |                                     |         |
| ГМС-3  | Знак ГПНП<br>АО «Читаглавснаб»<br>ПК0+32,98 | Упор<br>ПК5+19,77 | нет                       | 03.2025                 | Егиазарян<br>Н.А.                   |         |

**Таблица 2.4 – Искусственные сооружения**

| № пути | Граница путей                               |                   | Вид искусственного сооружения | Дата внесения изменений | Ф.И.О. должность внесшего изменения | Подпись |
|--------|---------------------------------------------|-------------------|-------------------------------|-------------------------|-------------------------------------|---------|
|        | от пикета                                   | до пикета         |                               |                         |                                     |         |
| ГМС-3  | Знак ГПНП<br>АО «Читаглавснаб»<br>ПК0+32,98 | Упор<br>ПК5+19,77 | нет                           | 03.2025                 | Егиазарян<br>Н.А.                   |         |

**Таблица 2.5 – Пересечения с автомобильными дорогами**

| № пути | от пикета                                   | до пикета         | Вид пересечения                    | Дата внесения изменений | Ф.И.О. должность внесшего изменения | Подпись |
|--------|---------------------------------------------|-------------------|------------------------------------|-------------------------|-------------------------------------|---------|
| ГМС-3  | Знак ГПНП<br>АО «Читаглавснаб»<br>ПК0+32,98 | Упор<br>ПК5+19,77 | Переезд<br>шир. 6,50м<br>ПК1+81,44 | 03.2025                 | Егиазарян<br>Н.А.                   |         |

|              |              |
|--------------|--------------|
| Инв. № подл. | Взам. Инв. № |
| 2504-ТП      |              |
| Подп. и дата |              |

|      |         |      |        |       |      |           |  |  |  |  |      |
|------|---------|------|--------|-------|------|-----------|--|--|--|--|------|
| Изм. | Кол.уч. | Лист | № док. | Подп. | Дата | 2504 – ТП |  |  |  |  | Лист |
|      |         |      |        |       |      |           |  |  |  |  | 3    |

### 3 ВЕРХНЕЕ СТРОЕНИЕ ПУТИ

**Таблица 3.1 – Род балласта в балластном слое**

| № пути | Граница путей                               |                   | Род балласта | Дата внесения изменений | Ф.И.О. должность внесшего изменения | Подпись |
|--------|---------------------------------------------|-------------------|--------------|-------------------------|-------------------------------------|---------|
|        | от пикета                                   | до пикета         |              |                         |                                     |         |
| ГМС-3  | Знак ГППП<br>АО «Читаглавснаб»<br>ПК0+32,98 | Упор<br>ПК5+19,77 | ПГС          | 03.2025                 | Егиазарян<br>Н.А.                   |         |

**Таблица 3.2 – Толщина балластного слоя**

| № пути | Граница путей                               |                   | Толщина  | Дата внесения изменений | Ф.И.О. должность внесшего изменения | Подпись |
|--------|---------------------------------------------|-------------------|----------|-------------------------|-------------------------------------|---------|
|        | от пикета                                   | до пикета         |          |                         |                                     |         |
| ГМС-3  | Знак ГППП<br>АО «Читаглавснаб»<br>ПК0+32,98 | Упор<br>ПК5+19,77 | 10-15 см | 03.2025                 | Егиазарян<br>Н.А.                   |         |

**Таблица 3.3 – Загрязнение балластного слоя**

| № пути | Граница путей                               |                   | Загрязнение | Дата внесения изменений | Ф.И.О. должность внесшего изменения | Подпись |
|--------|---------------------------------------------|-------------------|-------------|-------------------------|-------------------------------------|---------|
|        | от пикета                                   | до пикета         |             |                         |                                     |         |
| ГМС-3  | Знак ГППП<br>АО «Читаглавснаб»<br>ПК0+32,98 | Упор<br>ПК5+19,77 | 25%         | 03.2025                 | Егиазарян<br>Н.А.                   |         |

**Таблица 3.4 – Загрязняемость балластного слоя**

| № пути | Граница путей                               |                   | Загрязняемость | Дата внесения изменений | Ф.И.О. должность внесшего изменения | Подпись |
|--------|---------------------------------------------|-------------------|----------------|-------------------------|-------------------------------------|---------|
|        | от пикета                                   | до пикета         |                |                         |                                     |         |
| ГМС-3  | Знак ГППП<br>АО «Читаглавснаб»<br>ПК0+32,98 | Упор<br>ПК5+19,77 | до 5%          | 03.2025                 | Егиазарян<br>Н.А.                   |         |

|              |         |
|--------------|---------|
| Инв. № подл. | 2504-ТП |
| Подп. и дата |         |
| Взам. Инв. № |         |

|      |         |      |        |       |      |           |  |  |  |      |
|------|---------|------|--------|-------|------|-----------|--|--|--|------|
| Изм. | Кол.уч. | Лист | № док. | Подп. | Дата | 2504 – ТП |  |  |  | Лист |
|      |         |      |        |       |      |           |  |  |  | 4    |

Таблица 3.5 – Эпюра шпал, количество шпал в пути, материал шпал

| № пути                   | Граница путей                               |                      | Эпюра,<br>количество<br>материал | Дата<br>внесения<br>изменений | Ф.И.О.<br>должность<br>внесшего<br>изменения | Подпись |
|--------------------------|---------------------------------------------|----------------------|----------------------------------|-------------------------------|----------------------------------------------|---------|
|                          | от пикета                                   | до пикета            |                                  |                               |                                              |         |
| Шпалы – эпюра 1600 шп/км |                                             |                      |                                  |                               |                                              |         |
| ГМС-3                    | Знак ГППП<br>АО «Читаглавснаб»<br>ПК0+32,98 | Упор<br>ПК5+19,77    | 778 шп                           | 03.2025                       | Егиазарян<br>Н.А.                            |         |
| Итого                    |                                             | Шпалы: дер – 778 шп. |                                  |                               |                                              |         |

Таблица 3.9 – Тип рельсов

| № пути | Граница путей                               |                                       | Тип рельсов,<br>длина, м. | Дата<br>внесения<br>изменений | Ф.И.О.<br>должность<br>внесшего<br>изменения | Подпись |
|--------|---------------------------------------------|---------------------------------------|---------------------------|-------------------------------|----------------------------------------------|---------|
|        | от пикета                                   | до пикета                             |                           |                               |                                              |         |
| ГМС-3  | Знак ГППП<br>АО «Читаглавснаб»<br>ПК0+32,98 | ПК3+12,94                             | P65 279,96м x 2           | 03.2025                       | Егиазарян<br>Н.А.                            |         |
|        | ПК3+12,94                                   | Упор<br>ПК5+19,77                     | P50 260,83м x 2           |                               |                                              |         |
| Итого  |                                             | Рельсы P65 –559,92 м<br>P50 –521.66 м |                           |                               |                                              |         |

Таблица 3.7 – Наличие сварных стыков

| № пути | Граница путей                               |                   | Наличие<br>сварных<br>стыков | Дата<br>внесения<br>изменений | Ф.И.О.<br>должность<br>внесшего<br>изменения | Подпись |
|--------|---------------------------------------------|-------------------|------------------------------|-------------------------------|----------------------------------------------|---------|
|        | от пикета                                   | до пикета         |                              |                               |                                              |         |
| ГМС-3  | Знак ГППП<br>АО «Читаглавснаб»<br>ПК0+32,98 | Упор<br>ПК5+19,77 | нет                          | 03.2025                       | Егиазарян<br>Н.А.                            |         |

Таблица 3.8 – Ведомость стрелочных переводов

| №<br>Стрелочного<br>перевода | Вид стрелочного<br>перевода,<br>отклонение | Тип и марка<br>стрелочного<br>перевода | Полная<br>длина, м | Дата<br>внесения<br>изменений | Ф.И.О.<br>должность<br>внесшего<br>изменения | Подпись |
|------------------------------|--------------------------------------------|----------------------------------------|--------------------|-------------------------------|----------------------------------------------|---------|
| -                            |                                            |                                        |                    | 03.2025                       | Егиазарян<br>Н.А.                            |         |

Таблица 3.9 – Верхнее строение пути на стрелочных переводах

| № стрелочного перевода | Тип рельсов | Подрельсовое основание |      | Вид балласта | Дата внесения изменений | Ф.И.О. должность внесшего изменения | Подпись |
|------------------------|-------------|------------------------|------|--------------|-------------------------|-------------------------------------|---------|
|                        |             | Шпалы                  | Брус |              |                         |                                     |         |
| -                      |             |                        |      |              | 03.2025                 | Егиазарян Н.А.                      |         |

|              |         |
|--------------|---------|
| Взам. Инв. № |         |
| Подп. и дата |         |
| Инв. № подл. | 2504-ТП |

|      |         |      |        |       |      |           |  |      |
|------|---------|------|--------|-------|------|-----------|--|------|
| Изм. | Кол.уч. | Лист | № док. | Подп. | Дата | 2504 – ТП |  | Лист |
|      |         |      |        |       |      |           |  | 5    |

Таблица 3.10 – Стыковые крепления

| № пути | Накладки        |        | Количество стыковых болтов | Дата внесения изменений | Ф.И.О. должность внесшего изменения | Подпись |
|--------|-----------------|--------|----------------------------|-------------------------|-------------------------------------|---------|
|        | тип             | Кол-во |                            |                         |                                     |         |
| ГМС-3  | Двухголовые Р65 | 56     | 224                        | 03.2025                 | Егиязарян Н.А.                      |         |
|        | Р65/Р50         | 8      | 32                         |                         |                                     |         |
|        | Двухголовые Р50 | 44     | 176                        |                         |                                     |         |

Таблица 3.11 – Промежуточные крепления

| № пути | Промежуточное крепление |                  | Дата внесения изменений | Ф.И.О. должность внесшего изменения | Подпись |
|--------|-------------------------|------------------|-------------------------|-------------------------------------|---------|
|        | Подкладки, шт           | Прикрепители, шт |                         |                                     |         |
| ГМС-3  | 1556                    | 6224             | 03.2025                 | Егиязарян Н.А.                      |         |

Таблица 3.12 – Закрепление от угона

| № пути | Граница путей                             |                   | Количество/ тип противоугонов | Дата внесения изменений | Ф.И.О. должность внесшего изменения | Подпись |
|--------|-------------------------------------------|-------------------|-------------------------------|-------------------------|-------------------------------------|---------|
|        | от пикета                                 | до пикета         |                               |                         |                                     |         |
| ГМС-3  | Знак ГПП<br>АО «Читаглавнаб»<br>ПК0+32,98 | Упор<br>ПК5+19,77 | нет                           | 03.2025                 | Егиязарян Н.А.                      |         |

|              |              |              |
|--------------|--------------|--------------|
| Инв. № подл. | Подп. и дата | Взам. Инв. № |
| 2504-ТП      |              |              |
| Изм.         | Кол.уч.      | Лист         |
| № док.       | Подп.        | Дата         |

#### 4 ТЕХНИЧЕСКОЕ ОСНАЩЕНИЕ ГРУЗОВОГО ФРОНТА

Наличие договора на подачу/уборку вагонов: \_\_\_\_\_

Наличие лицензии:

Наличие таможенных складов временного хранения:

### Таблица 4.1 – Вместимость грузовых фронтов

| №<br>грузового<br>фронта | Наименование.<br>Грузового<br>фронта | Местоположение |           |           | Длина,<br>м. | Вместимость,<br>усл. ваг. |
|--------------------------|--------------------------------------|----------------|-----------|-----------|--------------|---------------------------|
|                          |                                      | № пути         | от пикета | до пикета |              |                           |
| ГФ1                      | Открытая<br>площадка<br>(слева)      | ГМС-3          | ПК1+92,64 | ПК2+99,64 | 107,0        | 7 (кр., пл., пв.)         |
| ГФ2                      | Рампа<br>(слева)                     | ГМС-3          | ПК3+91,47 | ПК5+17,42 | 125,95       | 8 (кр., пл., пв.)         |

### Технико-технологическая характеристика грузовых фронтов:

ГФ1 – открытая площадка (слева):

Среднесуточный вагонооборот (максимальный) – 7 вагонов.

Перечень перерабатываемых грузов – погрузка/выгрузка: строительные материалы, кирпич, цемент в МКР, металлолом, металлопрокат, черный металл, металлические конструкции, ЖБИ, оборудование, автомобили, машины и механизмы, сельскохозяйственные машины, контейнера среднетоннажные и крупнотоннажные до 20тн.

Перечень перерабатываемых опасных грузов – нет.

Средства механизации: козловой кран, грузоподъемность 20тн.; погрузчик вилочный, грузоподъемность 3тн.; погрузчик вилочный, грузоподъемность 5 тн.

*ГФ2 – рампа (слева):*

Среднесуточный вагонооборот (максимальный) – 8 вагонов.

Перечень перерабатываемых грузов – погрузка/выгрузка: тарно-штучные грузы, строительные материалы, кирпич, цемент в МКР, битум в мешках, кабель, стекло.

Перечень перерабатываемых опасных грузов – нет.

Средства механизации: погрузчик вилочный, грузоподъемность 3тн.; погрузчик вилочный, грузоподъемность 5 тн.

*Технический паспорт составлен на основании имеющихся документов и результатов инструментальной съемки и фактического состояния пути.*

*Данный технический паспорт предназначен только для разработки инструкции о порядке обслуживания и организации движения на железнодорожном пути необщего пользования АО «Читаглавснаб».*

Данный технический паспорт не устанавливает права собственности на железнодорожные пути, стрелочные переводы.

Ведущий инженер  
ООО «Забтранспроект»

Егiazарян Н.А.

Взам. ИИНВ. №

Подп. и дата

ИНВ. № подл.

2504-TP

|      |         |      |        |       |      |
|------|---------|------|--------|-------|------|
| Изм. | Кол.уч. | Лист | № док. | Подп. | Дата |
|------|---------|------|--------|-------|------|

2504 – ТП

Лист

7



Свидетельства о допуске к работам в области инженерных изысканий, которые оказывают влияние на безопасность объектов капитального строительства

Саморегулируемая организация  
основанная на членстве лиц, осуществляющих изыскания  
(вид саморегулируемой организации)

**АССОЦИАЦИЯ ИНЖЕНЕРОВ-ИЗЫСКАТЕЛЕЙ**  
**«Инженерная подготовка нефтегазовых комплексов»**  
192012, г. Санкт-Петербург, пер. 3-й Рабфакровский, д. 5.  
корп. 4, литер А, оф. 4.11.  
[www.ingneft.ru](http://www.ingneft.ru)  
**№СРО-И-032-22122011**

Санкт - Петербург (место выдачи Свидетельства) «07» марта 2017г.  
(дата выдачи Свидетельства)

**СВИДЕТЕЛЬСТВО**  
о допуске к определённому виду или видам работ, которые  
оказывают влияние на безопасность объектов капитального  
строительства  
**№ 1266**

Выдано члену саморегулируемой организации

Общество с ограниченной ответственностью «Забтранспроект»,  
ОГРН 1127536004012, ИНН 7536127844,  
672039, Забайкальский край, г.Чита, ул.Красноярская, дом 31, пом.47

Основание выдачи Свидетельства: решение Контрольно-дисциплинарного комитета  
(наименование органа управления саморегулируемой организации,  
АС «Инженерная подготовка нефтегазовых комплексов»  
№ 7КДК от 07 марта 2017г.  
(номер протокола, дата заседания)

Настоящим Свидетельством подтверждается допуск к работам, указанным в  
приложении к настоящему Свидетельству, которые оказывают влияние на  
безопасность объектов капитального строительства.  
Начало действия с «07» марта 2017г.  
Свидетельство без приложения не действительно.  
Свидетельство выдано без ограничения срока и территории его действия.  
Свидетельство выдано взамен ранее выданного № 147 от 26 июля 2012г.  
(дата выдачи, номер Свидетельства)

Генеральный директор  
АС «Инженерная подготовка  
нефтегазовых комплексов»  
(должность уполномоченного лица)

Артемкин Н.Ф.  
(инициалы, фамилия)

(подпись)

(подпись)

Ассоциация  
ОГРН 1127536004012  
«Инженерная  
подготовка  
нефтегазовых  
комплексов»  
ИНН 7536127844  
Санкт-Петербург

|              |         |
|--------------|---------|
| Инв. № подл. | 2504-ТП |
| Подп. и дата |         |
| Взам. Инв. № |         |

|      |         |      |        |       |      |
|------|---------|------|--------|-------|------|
| Изм. | Кол.уч. | Лист | № док. | Подп. | Дата |
|      |         |      |        |       |      |

## ПРИЛОЖЕНИЕ

к Свидетельству о допуске к  
определённому виду или видам работ,  
которые оказывают влияние на  
безопасность объектов капитального  
строительства  
от «07» марта 2017г.  
№ 1266

**Виды работ, которые оказывают влияние на безопасность:**

1. объектов капитального строительства, включая особо опасные и технически сложные объекты капитального строительства, объекты использования атомной энергии, и о допуске к которым член АС «Инженерная подготовка нефтегазовых комплексов» Общество с ограниченной ответственностью «Забтранспроект», ИНН 7536127844 имеет Свидетельство

| № пп | Наименование вида работ |
|------|-------------------------|
|      | НЕТ                     |

2. объектов капитального строительства, включая особо опасные и технически сложные объекты капитального строительства (кроме объектов использования атомной энергии) и о допуске к которым член АС «Инженерная подготовка нефтегазовых комплексов» Общество с ограниченной ответственностью «Забтранспроект», ИНН 7536127844 имеет Свидетельство

| № пп | Наименование вида работ   |
|------|---|
| 1.   | РАБОТЫ В СОСТАВЕ ИНЖЕНЕРНО-ГЕОДЕЗИЧЕСКИХ ИЗЫСКАНИЙ   |
| 1.1. | Создание опорных геодезических сетей.   |
| 1.2. | Геодезические наблюдения за деформациями и осадками зданий и сооружений, движениями земной поверхности и опасными природными процессами.                     |
| 1.3. | Создание и обновление инженерно-топографических планов в масштабах 1:200 – 1:5000, в том числе в цифровой форме, съемка подземных коммуникаций и сооружений. |
| 1.4. | Трассирование линейных объектов.   |
| 1.5. | Инженерно-гидрографические работы.   |
| 1.6. | Специальные геодезические и топографические работы при строительстве и реконструкции зданий и сооружений.                                                    |
| 2.   | РАБОТЫ В СОСТАВЕ ИНЖЕНЕРНО-ГЕОЛОГИЧЕСКИХ ИЗЫСКАНИЙ   |
| 2.1. | Инженерно-геологическая съемка в масштабах 1:500 – 1:25000.                                                                                                  |
| 2.2. | Проходка горных выработок с их опробованием, лабораторные исследования физико-механических свойств грунтов и химических свойств проб подземных вод.          |
| 2.3. | Изучение опасных геологических и инженерно-геологических процессов с разработкой рекомендаций по инженерной защите территории.                               |
| 2.4. | Гидрогеологические исследования.   |
| 2.5. | Инженерно-геофизические исследования.   |
| 2.6. | Инженерно-геокриологические исследования.   |
| 2.7. | Сейсмологические и сейсмотектонические исследования территории, сейсмическое микрорайонирование.                                                             |
| 3.   | РАБОТЫ В СОСТАВЕ ИНЖЕНЕРНО-ГИДРОМЕТЕОРОЛОГИЧЕСКИХ ИЗЫСКАНИЙ                                                                                                  |
| 3.1. | Метеорологические наблюдения и изучение гидрологического режима водных объектов.                                                                             |
| 3.2. | Изучение опасных гидрометеорологических процессов и явлений с расчетами их                                                                                   |

|              |              |
|--------------|--------------|
| Инв. № подл. | Взам. Инв. № |
| 2504-ТП      |              |
| Подп. и дата |              |
| Изм.         | Кол.уч.      |
| Лист         | № док.       |
| Подп.        | Дата         |



|      |   |
|------|---|
|      | характеристик.   |
| 3.3. | Изучение русловых процессов водных объектов, деформаций и переработки берегов.   |
| 3.4. | Исследования ледового режима водных объектов.   |
| 4.   | <b>РАБОТЫ В СОСТАВЕ ИНЖЕНЕРНО-ЭКОЛОГИЧЕСКИХ ИЗЫСКАНИЙ</b>   |
| 4.1. | Инженерно-экологическая съемка территории.   |
| 4.2. | Исследования химического загрязнения почвогрунтов, поверхностных и подземных вод, атмосферного воздуха, источников загрязнения.                                                                                                 |
| 4.3. | Лабораторные химико-аналитические и газохимические исследования образцов и проб почвогрунтов и воды.   |
| 4.4. | Исследования и оценка физических воздействий и радиационной обстановки на территории.   |
| 4.5. | Изучение растительности, животного мира, санитарно-эпидемиологические и медико-биологические исследования территории*   |
| 5.   | <b>РАБОТЫ В СОСТАВЕ ИНЖЕНЕРНО-ГЕОТЕХНИЧЕСКИХ ИЗЫСКАНИЙ (ВЫПОЛНЯЮТСЯ В СОСТАВЕ ИНЖЕНЕРНО-ГЕОЛОГИЧЕСКИХ ИЗЫСКАНИЙ ИЛИ ОТДЕЛЬНО НА ИЗУЧЕННОЙ В ИНЖЕНЕРНО-ГЕОЛОГИЧЕСКОМ ОТНОШЕНИИ ТЕРРИТОРИИ ПОД ОТДЕЛЬНЫЕ ЗДАНИЯ И СООРУЖЕНИЯ)</b> |
| 5.1. | Проходка горных выработок с их опробованием и лабораторные исследования механических свойств грунтов с определением характеристик для конкретных схем расчета оснований фундаментов.                                            |
| 5.2. | Полевые испытания грунтов с определением их стандартных прочностных и деформационных характеристик (штамповые, сдвиговые, прессиометрические, срезные). Испытания эталонных и натурных свай.                                    |
| 5.3. | Определение стандартных механических характеристик грунтов методами статического, динамического и бурового зондирования.   |
| 5.4. | Физическое и математическое моделирование взаимодействия зданий и сооружений с геологической средой.   |
| 5.5. | Специальные исследования характеристик грунтов по отдельным программам для нестандартных, в том числе нелинейных методов расчета оснований фундаментов и конструкций зданий и сооружений.                                       |
| 5.6. | Геотехнический контроль строительства зданий, сооружений и прилегающих территорий.   |
| 6.   | Обследование состояния грунтов основания зданий и сооружений.   |

3. объектов капитального строительства (кроме особо опасных и технически сложных объектов, объектов использования атомной энергии) и о допуске к которым член АС «Инженерная подготовка нефтегазовых комплексов» Общество с ограниченной ответственностью «Забтранспроект», ИНН 7536127844 имеет Свидетельство

| № пп | Наименование вида работ |
|------|-------------------------|
|      | НЕТ                     |

Общество с ограниченной ответственностью «Забтранспроект» вправе заключать договоры по осуществлению организации работ в области инженерных изысканий, которые оказывают влияние на безопасность объектов капитального строительства.

Генеральный директор  
АС «Инженерная подготовка  
нефтегазовых комплексов»  
должность



Артемкин Н.Ф.  
фамилия, инициалы

|              |         |
|--------------|---------|
| Взам. Инв. № |         |
| Подп. и дата |         |
| Инв. № подл. | 2504-ТП |

|      |         |      |        |       |      |
|------|---------|------|--------|-------|------|
| Изм. | Кол.уч. | Лист | № док. | Подп. | Дата |
|      |         |      |        |       |      |

Ведомость ж.д. путей

| №<br>пути | Наименование пути      | Длина пути |          | Граница пути                                |                   |
|-----------|------------------------|------------|----------|---------------------------------------------|-------------------|
|           |                        | полная     | полезная | от                                          | до                |
| ГМСЗ      | Погрузочно-выгрузочный | 486,79     | 463,31   | Знак ГПНП<br>ОА "Читаглавснаб"<br>ПК0+32,98 | Упор<br>ПК5+19,77 |


Ведомость габаритов

| Номер | Тип сооружения   | Путь | Пикет                  | Габарит<br>лево/право |
|-------|------------------|------|------------------------|-----------------------|
| 1     | Подпорная стенка | ГМСЗ | ПК0+00,00<br>ПК1+14,68 | 2,78/-<br>3,25/-      |
| 2     | Ворота           | ГМСЗ | ПК1+89,10              | 3,05/1,50             |
| 3     | Подпорная стенка | ГМСЗ | ПК1+96,61<br>ПК2+81,32 | 2,92/-<br>4,03/-      |
| 4     | Угол здания      | ГМСЗ | ПК3+67,89              | 4,41/-                |
| 5     | Рампа            | ГМСЗ | ПК3+914,7<br>ПК5+17,42 | 3,50/-<br>3,16/-      |

Примечание:

1. Инструментальная съемка железнодорожных пути необщего пользования ГМСЗ ОА "Читаглавснаб" выполнена сотрудниками ООО Забтранспроект" в марте 2025 года с использованием спутникового навигационного оборудования типа JAVAD TRIUMPH-1-G3T.
2. Пикетаж разбит по оси пути ГМСЗ от стыка рамного рельса СПЗ2 ПК0+00,00.

|           |      |               |       |         |       |                                                |                                |      |        |
|-----------|------|---------------|-------|---------|-------|------------------------------------------------|--------------------------------|------|--------|
|           |      |               |       |         |       | 2504-ТП-ГЧ                                     |                                |      |        |
| Изм.      | Кол. | Лист          | Ндэк. | Подпись | Дата  | Пути необщего пользования<br>ОА "Читаглавснаб" |                                |      |        |
| Рук.работ |      | Городный К.А. |       |         | 03.25 | Станция Чита-1                                 | Стадия                         | Лист | Листов |
| Инженер   |      | Егизарян Н.А. |       |         | 03.25 |                                                |                                | 1    | 2      |
|           |      |               |       |         |       |                                                |                                |      |        |
|           |      |               |       |         |       | План пути ГМСЗ                                 | ООО "Забтранспроект"<br>2025г. |      |        |
| Н.контр.  |      | Егизарян Н.А. |       |         | 03.25 |                                                |                                |      |        |

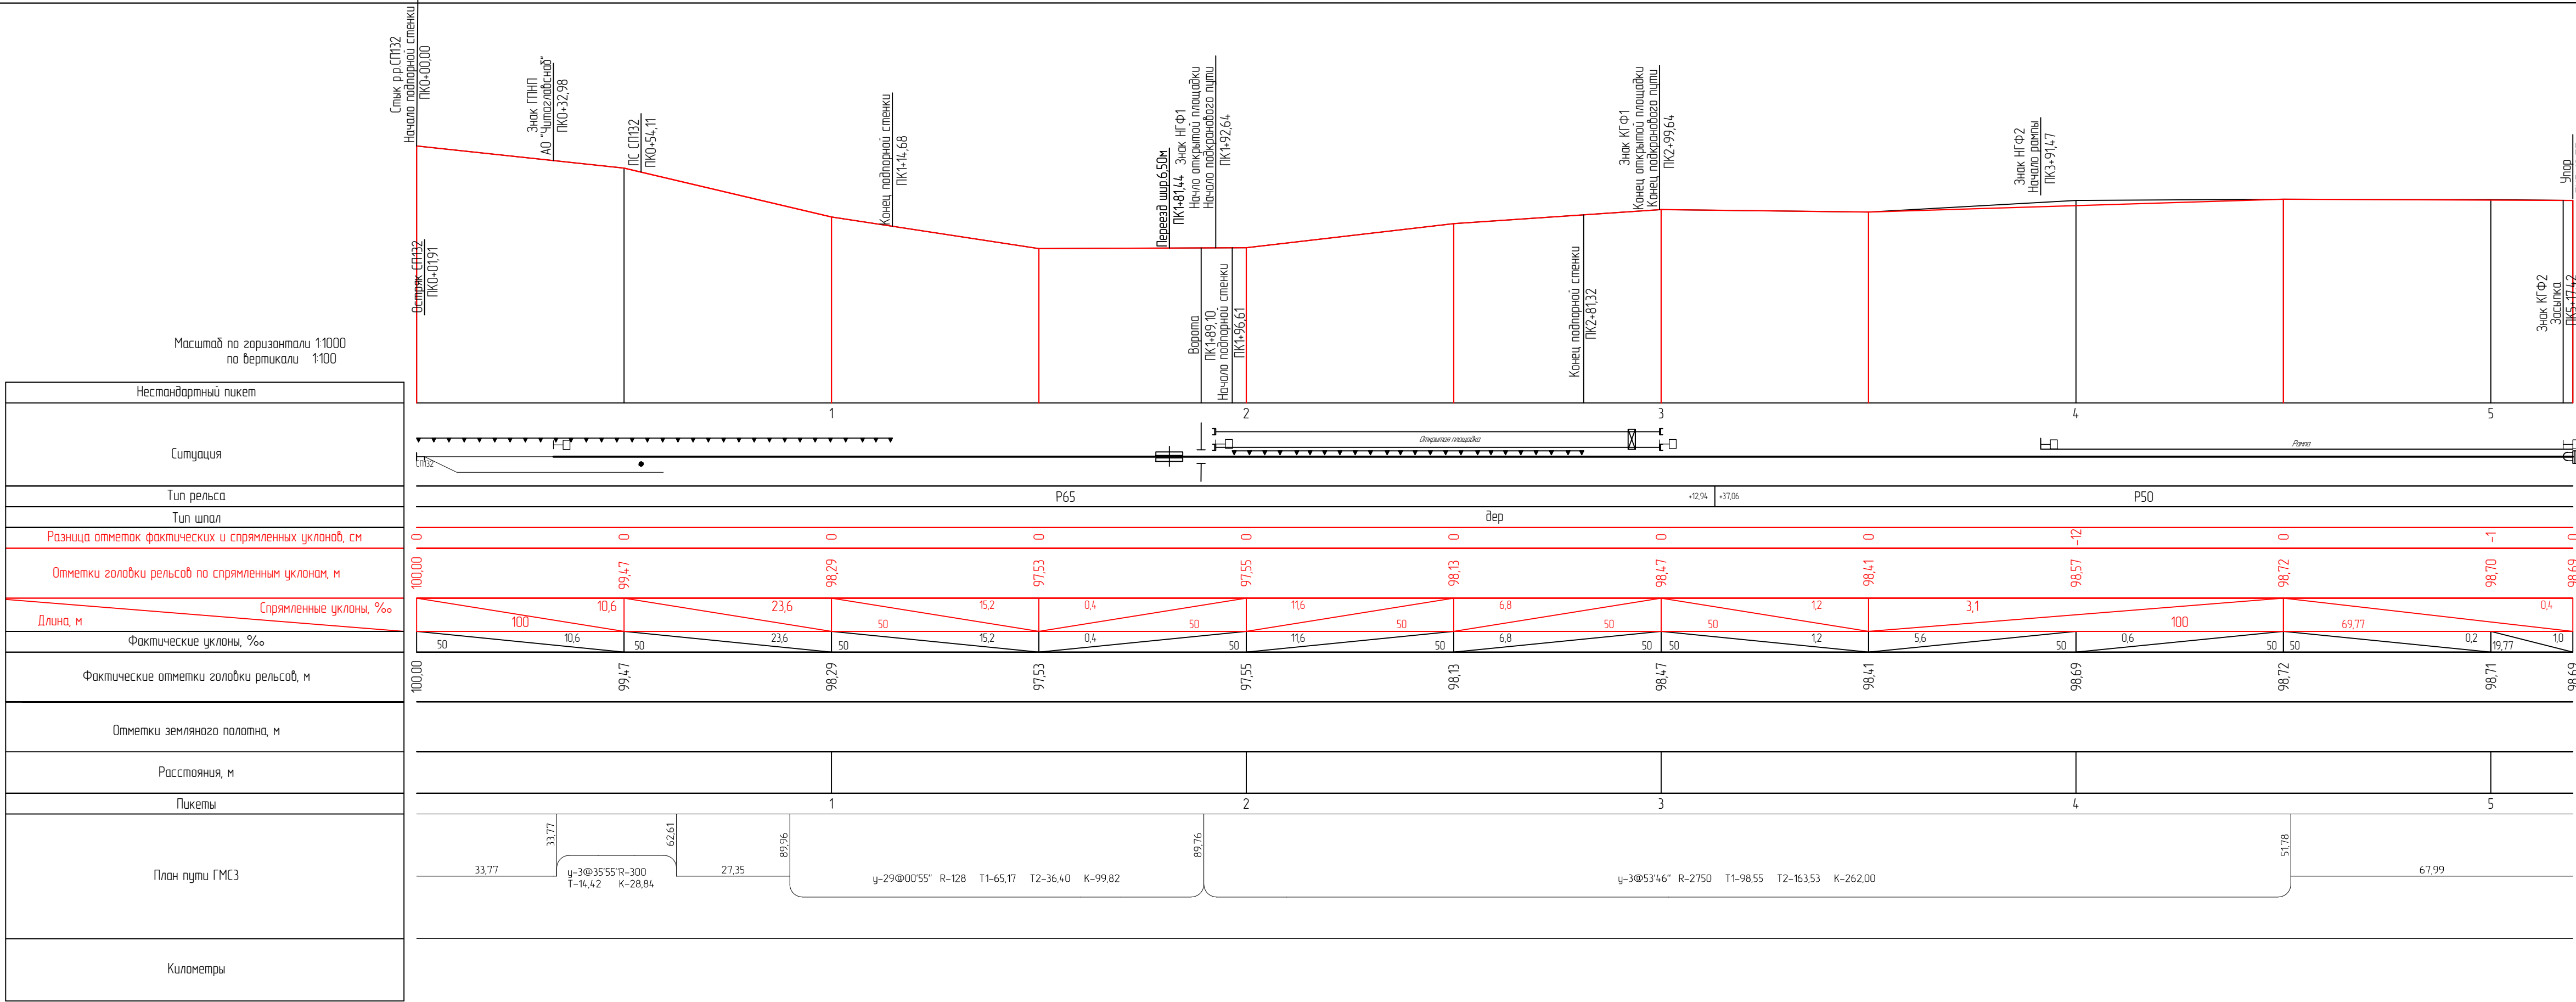

- Примечание:
- Инструментальная съемка железнодорожных пути необщего пользования ГМСЗ АО "Читаглавснаб" выполнена сотрудниками ООО Забтранспроект в марте 2025 года с использованием спутникового навигационного оборудования типа JAVAD TRIUMPH-1-G3T.
  - Пикетаж разбит по оси пути ГМСЗ от стыка рамного рельса СП132 ПКЮ+00,00.
  - Система высот условная.

|           |      |               |      |         |       |                              |                                |      |        |
|-----------|------|---------------|------|---------|-------|------------------------------|--------------------------------|------|--------|
|           |      |               |      |         |       | 2504-ТП-ГЧ                   |                                |      |        |
|           |      |               |      |         |       | Пути неообщего пользования   |                                |      |        |
| Изм.      | Кол. | Лист          | Ндэк | Подпись | Дата  | АО "Читаглавснаб"            |                                |      |        |
| Рук работ |      | Городной К.А. |      |         | 03.25 |                              |                                |      |        |
| Инженер   |      | Егизарян Н.А. |      |         | 03.25 | Станция Чита-1               | Стадия                         | Лист | Листов |
|           |      |               |      |         |       |                              |                                | 2    | 2      |
|           |      |               |      |         |       |                              |                                |      |        |
|           |      |               |      |         |       | Продольный профиль пути ГМСЗ | ООО "Забтранспроект"<br>2025г. |      |        |
| Н контр.  |      | Егизарян Н.А. |      |         | 03.25 |                              |                                |      |        |