



ОБЩЕСТВО С ОГРАНИЧЕННОЙ ОТВЕТСТВЕННОСТЬЮ
«ЗАБТРАНСПРОЕКТ»

Свидетельство № 1266 от 7 марта 2017 г.

СРО-И-032-22122011

ТЕХНИЧЕСКИЙ ПАСПОРТ

железнодорожного пути
необщего пользования
ООО «Восточно-Сибирская Торговая Компания»
ООО «ВСТК»

Путь №14

ст. Чита-I

Главный инженер
ООО «Забтранспроект»

Афанасенко С.Н.

Ведущий инженер

Егiazарян Н.А.

Чита, 2024

Взам. Инв. №	
Подп. и дата	
Инв. № подл.	2008-ТП

ОБЩИЕ СВЕДЕНИЯ

Место примыкания железнодорожного пути необщего пользования:

железнодорожный путь необщего пользования №14 ООО «ВСТК» примыкает стрелочным переводом №414П к железнодорожному пути №305а, находящемуся в ведении Читинской дистанции пути.

Границы железнодорожного пути необщего пользования:

границей железнодорожного пути необщего пользования №14 ООО «ВСТК» является знак «Граница пути необщего пользования» ПК0+42,95, установленный на обочине пути напротив предельного столбика СП№414П.

Наличие предохранительных устройств:

нет

Дата заключения договора на эксплуатацию железнодорожного пути необщего пользования и срок его действия:

Порядок подачи и уборки вагонов (кем производится – железной дорогой, средствами предприятия или маневровым порядком), серия локомотива, применяемого при подаче и уборке вагонов:

подача и уборка вагонов на путь необщего пользования №14 ООО «ВСТК» осуществляется маневровым порядком локомотивами серии ТЭМ-2, ТЭМ-18 ст. Чита-I Забайкальской железной дороги.

Взам. Инв. №	
Подп. и дата	
Инв. №подл.	2008-ТП

							2008 – ТП			
Изм.	Кол.уч.	Лист	№ док.	Подп.	Дата					
Разработал		Егизарян				Технический паспорт железнодорожного пути необщего пользования №14 ООО «Восточно-Сибирская Торговая Компания»		Стадия	Лист	Листов
Проверил		Афанасенко							1	12
						ООО «Забтранспроект»				

1 ХАРАКТЕРИСТИКА ПУТИ

Таблица 1.1 – Примыкания других железнодорожных путей к железнодорожным путям предприятия

Наименование предприятия	Место примыкания (пикет, стрелка)	Длина Путь км.	Предприятие обслуживающее путь необщего пользования
--------------------------	-----------------------------------	----------------	---

-

Таблица 1.2 - Ведомость железнодорожных путей предприятия

№ пути	Граница путей		Специализация	Дата внесения изменений	Ф.И.О. должность внесшего изменения	Подпись
	от	до				
14	Знак ГППП ООО «ВСТК» ПС СП414П ПК0+42,95	Упор ПК2+41,95	Погрузочно-выгрузочный. Для отстоя вагонов.	08.2020	Афанасенко С.Н.	

Таблица 1.3 – Данные по длине путей

№ пути	Граница путей		Длины путей, м		Дата внесения изменений	Ф.И.О. должность внесшего изменения	Подпись
	от	до	полная	полезная			
14	Знак ГППП ООО «ВСТК» ПС СП414П ПК0+42,95	Упор ПК2+41,95	199,00	188,60	08.2020	Афанасенко С.Н.	
ИТОГО			199,00	188,60			

Инва. № подл.	Подп. и дата	Взам. Инв. №
2008-ТП		

Изм.	Кол.уч.	Лист	№ док.	Подп.	Дата

2008 – ТП

Лист

2

2 НИЖНЕЕ СТРОЕНИЕ ПУТИ И ИСКУССТВЕННЫЕ СООРУЖЕНИЯ

Таблица 2.1 – Наличие насыпей или выемок

№ пути	Граница путей		Наличие насыпей право/лево	Дата внесения изменений	Ф.И.О. должность внесшего изменения	Подпись
	от пикета	до пикета				
14	Знак ГПНП ООО «ВСТК» ПС СП414П ПК0+42,95	Упор ПК2+41,95	нет	08.2020	Афанасенко С.Н.	

Таблица 2.2 – Наличие водоотводных сооружений

№ пути	Граница путей		Водоотводное устройство право/лево	Дата внесения изменений	Ф.И.О. должность внесшего изменения	Подпись
	от пикета	до пикета				
14	Знак ГПНП ООО «ВСТК» ПС СП414П ПК0+42,95	Упор ПК2+41,95	нет	08.2020	Афанасенко С.Н.	

Таблица 2.3 – Деформация земляного полотна

№ пути	Граница путей		Тип деформации право/лево	Дата внесения изменений	Ф.И.О. должность внесшего изменения	Подпись
	от пикета	до пикета				
14	Знак ГПНП ООО «ВСТК» ПС СП414П ПК0+42,95	Упор ПК2+41,95	нет	08.2020	Афанасенко С.Н.	

Таблица 2.4 – Искусственные сооружения

№ пути	Граница путей		Вид искусствен- ного сооружения	Дата внесения изменений	Ф.И.О. должность внесшего изменения	Подпись
	от пикета	до пикета				
14	Знак ГПНП ООО «ВСТК» ПС СП414П ПК0+42,95	Упор ПК2+41,95	нет	08.2020	Афанасенко С.Н.	

Взам. Инв. №	
Подп. и дата	
Инв. № подл.	2008-ТП

Изм.	Кол.уч.	Лист	№ док.	Подп.	Дата	2008 – ТП	Лист
							3

Таблица 2.5 – Пересечения с автомобильными дорогами

№ пути	от пикета	до пикета	Вид пересечения	Дата внесения изменений	Ф.И.О. должность внесшего изменения	Подпись
14	Знак ГПНП ООО «ВСТК» ПС СП414П ПК0+42,95	Упор ПК2+41,95	Технологический проезд ПК1+00,89	08.2020	Афанасенко С.Н.	

Инв. № подл.	Подп. и дата	Взам. Инв. №
2008-ТП		

Изм.	Кол.уч.	Лист	№ док.	Подп.	Дата

2008 – ТП

Лист

4

3 ВЕРХНЕЕ СТРОЕНИЕ ПУТИ

Таблица 3.1 – Род балласта в балластном слое

№ пути	Граница путей		Род балласта	Дата внесения изменений	Ф.И.О. должность внесшего изменения	Подпись
	от пикета	до пикета				
14	Знак ГПНП ООО «ВСТК» ПС СП414П ПК0+42,95	ПК1+55,92	щебень	08.2020	Афанасенко С.Н.	
	ПК1+55,92	ПК2+22,06	Бетонное основание			
	ПК2+22,06	Упор ПК2+41,95	щебень			

Таблица 3.2 – Толщина балластного слоя

№ пути	Граница путей		Толщина	Дата внесения изменений	Ф.И.О. должность внесшего изменения	Подпись
	от пикета	до пикета				
14	Знак ГПНП ООО «ВСТК» ПС СП414П ПК0+42,95	ПК1+55,92	до 15 см	08.2020	Афанасенко С.Н.	
	ПК1+55,92	ПК2+22,06	-			
	ПК2+22,06	Упор ПК2+41,95	до 15 см			

Таблица 3.3 – Загрязнение балластного слоя

№ пути	Граница путей		Загрязнение	Дата внесения изменений	Ф.И.О. должность внесшего изменения	Подпись
	от пикета	до пикета				
14	Знак ГПНП ООО «ВСТК» ПС СП414П ПК0+42,95	ПК1+55,92	до 20%	08.2020	Афанасенко С.Н.	
	ПК1+55,92	ПК2+22,06	0%			
	ПК2+22,06	Упор ПК2+41,95	до 20%			

Инва. № подл.	2008-ТП
Подп. и дата	
Взам. Инв. №	

Изм.	Кол.уч.	Лист	№ док.	Подп.	Дата	2008 – ТП	Лист
							5

Таблица 3.4 – Загрязняемость балластного слоя

№ пути	Граница путей		Загрязняе- мость	Дата внесения изменений	Ф.И.О. должность внесшего изменения	Подпись
	от пикета	до пикета				
14	Знак ГПНП ООО «ВСТК» ПС СП414П ПК0+42,95	ПК1+55,92	1%	08.2020	Афанасенко С.Н.	
	ПК1+55,92	ПК2+22,06	нет			
	ПК2+22,06	Упор ПК2+41,95	1%			

Таблица 3.5 – Эпюра шпал, количество шпал в пути, материал шпал

Таблица 3.3 Эпюра шпал, количество шпал в пути, материал шпал						
№ пути	Граница путей		Эпюра, количество материал	Дата внесения изменений	Ф.И.О. должность внесшего изменения	Подпись
	от пикета	до пикета				
Шпалы – эпюра 1600 шп/км						
14	Знак ГПНП ООО «ВСТК» ПС СП414П ПК0+42,95	ПК1+55,92	180 шп – дер.	08.2020	Афанасенко С.Н.	
	ПК1+55,92	Упор ПК2+41,95	137 шп – ж/б			
Итого		Шпалы деревянные – 180 шп железобетонные – 137 шп				

Таблица 3.6 – Тип рельсов

№ пути	Граница путей		Тип рельсов, длина, м.	Дата внесения изменений	Ф.И.О. должность внесшего изменения	Подпись
	от пикета	до пикета				
14	Знак ГПНП ООО «ВСТК» ПС СП414П ПК0+42,95	ПК1+49,62	P43 2x106,67 м	08.2020	Афанасенко С.Н.	
	ПК1+49,62	ПК1+55,92	P50 2x6,30 м			
	ПК1+55,92	Упор ПК2+41,95	P65 2x86,03 м			
Итого		Рельсы P43 – 213,34 м P50 – 12,60 м P65 – 172,06 м				

Взам. Инв. №

Подп. и дата

Инв. № подл.

2008-ТП

2008 – ТП

Лист

6

Изм. Кол.уч. Лист № док. Подп. Дата

Таблица 3.7 – Наличие сварных стыков

№ пути	Граница путей		Наличие сварных стыков	Дата внесения изменений	Ф.И.О. должность внесшего изменения	Подпись
	от пикета	до пикета				
14	Знак ГПНП ООО «ВСТК» ПС СП414П ПК0+42,95	Упор ПК2+41,95	нет	08.2020	Афанасенко С.Н.	

Таблица 3.8 – Ведомость стрелочных переводов

№ Стрелочного перевода	Вид стрелочного перевода, отклонение	Тип и марка стрелочного перевода	Полная длина, м	Дата внесения изменений	Ф.И.О. должность внесшего изменения	Подпись
-						

Таблица 3.9 – Верхнее строение пути на стрелочных переводах

№ стрелочного перевода	Тип рельсов	Подрельсовое основание		Вид балласта	Дата внесения изменений	Ф.И.О. должность внесшего изменения	Подпись
		Шпалы	Брус				
-							

Таблица 3.10 – Стыковые крепления

№ пути	Накладки		Количество стыковых болтов	Дата внесения изменений	Ф.И.О. должность внесшего изменения	Подпись
	тип	Кол-во				
14	Двухголовые Р43	24	144	08.2020	Афанасенко С.Н.	
	Переходные Р43/Р50	2	12			
	Переходные Р50/Р65	2	12			
	Двухголовые Р65	24	48			

Таблица 3.11 – Промежуточные крепления

№ пути	Промежуточное крепление		Дата внесения изменений	Ф.И.О. должность внесшего изменения	Подпись
	Подкладки, шт	Прикрепители, шт			
14	Д43 – 342 Д50 – 20	Костыли – 2172	08.2020	Афанасенко С.Н.	
Скрепление КБ – 274 узла					

Таблица 3.12 – Закрепление от угона

№ пути	Граница путей		Количество/ тип проти-воугонов	Дата внесения изменений	Ф.И.О. должность внесшего изменения	Подпись
	от пикета	до пикета				
14	Знак ГПНП ООО «ВСТК» ПС СП414П ПК0+42,95	Упор ПК2+41,95	нет	08.2020	Афанасенко С.Н.	

Взам. Инв. №	
Подп. и дата	
Инв. № подл.	2008-ТП

Изм.	Кол.уч.	Лист	№ док.	Подп.	Дата	2008 – ТП		Лист
								7

4 ТЕХНИЧЕСКОЕ ОСНАЩЕНИЕ ГРУЗОВОГО ФРОНТА

Наличие договора на подачу/уборку вагонов:

Наличие лицензии:

Наличие таможенных складов временного хранения:

Таблица 4.1 – Вместимость грузовых фронтов

№ грузового фронта	Наименование. Грузового фронта	Местоположение			Длина, м.	Вместимость, усл. ваг.
		№ пути	от пикета	до пикета		
ГФ1	Открытая площадка	14	ПК1+26,19	ПК1+51,73	25,54	1 (кр., пв., пл.) 2 ц.
ГФ2	Сливо-наливная эстакада	14	ПК1+57,66	ПК2+40,15	82,49	6 ц.

Технико-технологическая характеристика грузовых фронтов:

ГФ1 – открытая площадка

Среднесуточный вагонооборот (максимальный) – 2 вагона.

Перечень перерабатываемых грузов – выгрузка: строительные конструкции, оборудование.

Перечень перерабатываемых опасных грузов – ГСМ (отстой цистерн).

Средства механизации – кран на автомобильном ходу, грузоподъемностью 25т.

ГФ2 – Сливно-наливная эстакада

Среднесуточный вагонооборот (максимальный) – 6 вагонов.

Перечень перерабатываемых грузов – слив ГСМ (бензин, дизельное топливо).

Перечень перерабатываемых опасных грузов – ГСМ (бензин, дизельное топливо).

Средства механизации – установка для слива железнодорожных цистерн – бшт., насос КМ-80-170Е производительностью 40м³/ч – 3шт, (2шт в резерве), грузовые автомобили: МАЗ АЦ-8-500, Камаз 6460-63, Скания G400CA6x4HNSA, Скания 400LA6x4HNA, полуприцепы и прицепы: Нефаз 97742-10-10, Граз 96222-0000010, Граз 96222-0000010-03, автокран МАЗ 5334 КС3577.

Технический паспорт составлен на основании имеющихся документов и результатов инструментальной съемки и фактического состояния пути.

Данный технический паспорт предназначен только для разработки инструкции о порядке обслуживания и организации движения на железнодорожном пути необщего пользования ООО «ВСТК»

Данный технический паспорт не устанавливает права собственности на железнодорожные пути, стрелочные переводы.

Главный инженер
ООО «Забтранспроект»

Афанасенко С.Н.

Инв. №подл.	Подп. и дата	Взам. Инв. №
2008-ТП		

						2008 – ТП	Лист
							8
Изм.	Кол.уч.	Лист	№ док.	Подп.	Дата		

ПРИЛОЖЕНИЕ

Свидетельства о допуске к работам в области инженерных изысканий, которые оказывают влияние на безопасность объектов капитального строительства

 Саморегулируемая организация основанная на членстве лиц, осуществляющих изыскания (вид саморегулируемой организации)	
АССОЦИАЦИЯ ИНЖЕНЕРОВ-ИЗЫСКАТЕЛЕЙ «Инженерная подготовка нефтегазовых комплексов» 192012, г. Санкт-Петербург, пер. 3-й Рабфакровский, д. 5, корп. 4, литер А, оф. 4.11, www.ingneft.ru № СРО-И-032-22122011	
Санкт - Петербург (место выдачи Свидетельства)	«07» марта 2017г. (дата выдачи Свидетельства)
СВИДЕТЕЛЬСТВО о допуске к определённому виду или видам работ, которые оказывают влияние на безопасность объектов капитального строительства № 1266	
Выдано члену саморегулируемой организации Общество с ограниченной ответственностью «Забтранспроект», ОГРН 1127536004012, ИНН 7536127844, 672039, Забайкальский край, г.Чита, ул.Красноярская, дом 31, пом.47	
Основание выдачи Свидетельства: решение Контрольно-дисциплинарного комитета (наименование органа управления саморегулируемой организацией, АС «Инженерная подготовка нефтегазовых комплексов» № 7КДК от 07 марта 2017г. номер протокола, дата заседания)	
Настоящим Свидетельством подтверждается допуск к работам, указанным в приложении к настоящему Свидетельству, которые оказывают влияние на безопасность объектов капитального строительства. Начало действия с «07» марта 2017г. Свидетельство без приложения не действительно. Свидетельство выдано без ограничения срока и территории его действия. Свидетельство выдано взамен ранее выданного № 147 от 26 июля 2012г. (дата выдачи, номер Свидетельства)	
Генеральный директор АС «Инженерная подготовка нефтегазовых комплексов» (должность, наименование лица)	Артемкин Н.Ф. (инициалы, фамилия)
	

Взам. Инв. №

Подп. и дата

Инв. № подл.

2008-ТП

Изм.	Кол.уч.	Лист	№ док.	Подп.	Дата
------	---------	------	--------	-------	------

2008 – ТП

Лист

9

ПРИЛОЖЕНИЕ

к Свидетельству о допуске к
определённому виду или видам работ,
которые оказывают влияние на
безопасность объектов капитального
строительства

от «07» марта 2017г.

№ 1266

Виды работ, которые оказывают влияние на безопасность:

1. объектов капитального строительства, включая особо опасные и технически сложные объекты капитального строительства, объекты использования атомной энергии, и о допуске к которым член АС «Инженерная подготовка нефтегазовых комплексов» Общество с ограниченной ответственностью «Забтранспроект», ИНН 7536127844 имеет Свидетельство

№ пп	Наименование вида работ
	НЕТ

2. объектов капитального строительства, включая особо опасные и технически сложные объекты капитального строительства (кроме объектов использования атомной энергии) и о допуске к которым член АС «Инженерная подготовка нефтегазовых комплексов» Общество с ограниченной ответственностью «Забтранспроект», ИНН 7536127844 имеет Свидетельство

№ пп	Наименование вида работ
1.	РАБОТЫ В СОСТАВЕ ИНЖЕНЕРНО-ГЕОДЕЗИЧЕСКИХ ИЗЫСКАНИЙ
1.1.	Создание опорных геодезических сетей.
1.2.	Геодезические наблюдения за деформациями и осадками зданий и сооружений, движениями земной поверхности и опасными природными процессами.
1.3.	Создание и обновление инженерно-топографических планов в масштабах 1:200 – 1:5000, в том числе в цифровой форме, съемка подземных коммуникаций и сооружений.
1.4.	Трассирование линейных объектов.
1.5.	Инженерно-гидрографические работы.
1.6.	Специальные геодезические и топографические работы при строительстве и реконструкции зданий и сооружений.
2.	РАБОТЫ В СОСТАВЕ ИНЖЕНЕРНО-ГЕОЛОГИЧЕСКИХ ИЗЫСКАНИЙ
2.1.	Инженерно-геологическая съемка в масштабах 1:500 – 1:25000.
2.2.	Проходка горных выработок с их опробованием, лабораторные исследования физико-механических свойств грунтов и химических свойств проб подземных вод.
2.3.	Изучение опасных геологических и инженерно-геологических процессов с разработкой рекомендаций по инженерной защите территории.
2.4.	Гидрогеологические исследования.
2.5.	Инженерно-геофизические исследования.
2.6.	Инженерно-геокринологические исследования.
2.7.	Сейсмологические и сейсмотектонические исследования территории, сейсмическое микрорайонирование.
3.	РАБОТЫ В СОСТАВЕ ИНЖЕНЕРНО-ГИДРОМЕТЕОРОЛОГИЧЕСКИХ ИЗЫСКАНИЙ
3.1.	Метеорологические наблюдения и изучение гидрологического режима водных объектов.
3.2.	Изучение опасных гидрометеорологических процессов и явлений с расчетами их

Инв. № подл.	Подп. и дата	Взам. Инв. №
2008-ТП		
Изм.	Кол.уч.	Лист
№ док.	Подп.	Дата

	характеристик.
3.3.	Изучение русловых процессов водных объектов, деформаций и переработки берегов.
3.4.	Исследования ледового режима водных объектов.
4.	РАБОТЫ В СОСТАВЕ ИНЖЕНЕРНО-ЭКОЛОГИЧЕСКИХ ИЗЫСКАНИЙ
4.1.	Инженерно-экологическая съемка территории.
4.2.	Исследования химического загрязнения почвогрунтов, поверхностных и подземных вод, атмосферного воздуха, источников загрязнения.
4.3.	Лабораторные химико-аналитические и газохимические исследования образцов и проб почвогрунтов и воды.
4.4.	Исследования и оценка физических воздействий и радиационной обстановки на территории.
4.5.	Изучение растительности, животного мира, санитарно-эпидемиологические и медико-биологические исследования территории*
5.	РАБОТЫ В СОСТАВЕ ИНЖЕНЕРНО-ГЕОТЕХНИЧЕСКИХ ИЗЫСКАНИЙ (ВЫПОЛНЯЮТСЯ В СОСТАВЕ ИНЖЕНЕРНО-ГЕОЛОГИЧЕСКИХ ИЗЫСКАНИЙ ИЛИ ОТДЕЛЬНО НА ИЗУЧЕННОЙ В ИНЖЕНЕРНО-ГЕОЛОГИЧЕСКОМ ОТНОШЕНИИ ТЕРРИТОРИИ ПОД ОТДЕЛЬНЫЕ ЗДАНИЯ И СООРУЖЕНИЯ)
5.1.	Проходка горных выработок с их опробованием и лабораторные исследования механических свойств грунтов с определением характеристик для конкретных схем расчета оснований фундаментов.
5.2.	Полевые испытания грунтов с определением их стандартных прочностных и деформационных характеристик (штамповые, сдвиговые, прессиометрические, срезные). Испытания эталонных и натурных свай.
5.3.	Определение стандартных механических характеристик грунтов методами статического, динамического и бурового зондирования.
5.4.	Физическое и математическое моделирование взаимодействия зданий и сооружений с геологической средой.
5.5.	Специальные исследования характеристик грунтов по отдельным программам для нестандартных, в том числе нелинейных методов расчета оснований фундаментов и конструкций зданий и сооружений.
5.6.	Геотехнический контроль строительства зданий, сооружений и прилегающих территорий.
6.	Обследование состояния грунтов основания зданий и сооружений.

3. объектов капитального строительства (кроме особо опасных и технически сложных объектов, объектов использования атомной энергии) и о допуске к которым член АС «Инженерная подготовка нефтегазовых комплексов» Общество с ограниченной ответственностью «Забтранспроект», ИНН 7536127844 имеет Свидетельство

№ пп	Наименование вида работ
	НЕТ

Общество с ограниченной ответственностью «Забтранспроект» вправе заключать договоры по осуществлению организации работ в области инженерных изысканий, которые оказывают влияние на безопасность объектов капитального строительства.


Генеральный директор
АС «Инженерная подготовка
нефтегазовых комплексов»
должность



Артемкин Н.Ф.
фамилия, инициалы

Взам. Инв. №	
Подп. и дата	
Инв. № подл.	2008-ТП

Изм.	Кол.уч.	Лист	№ док.	Подп.	Дата

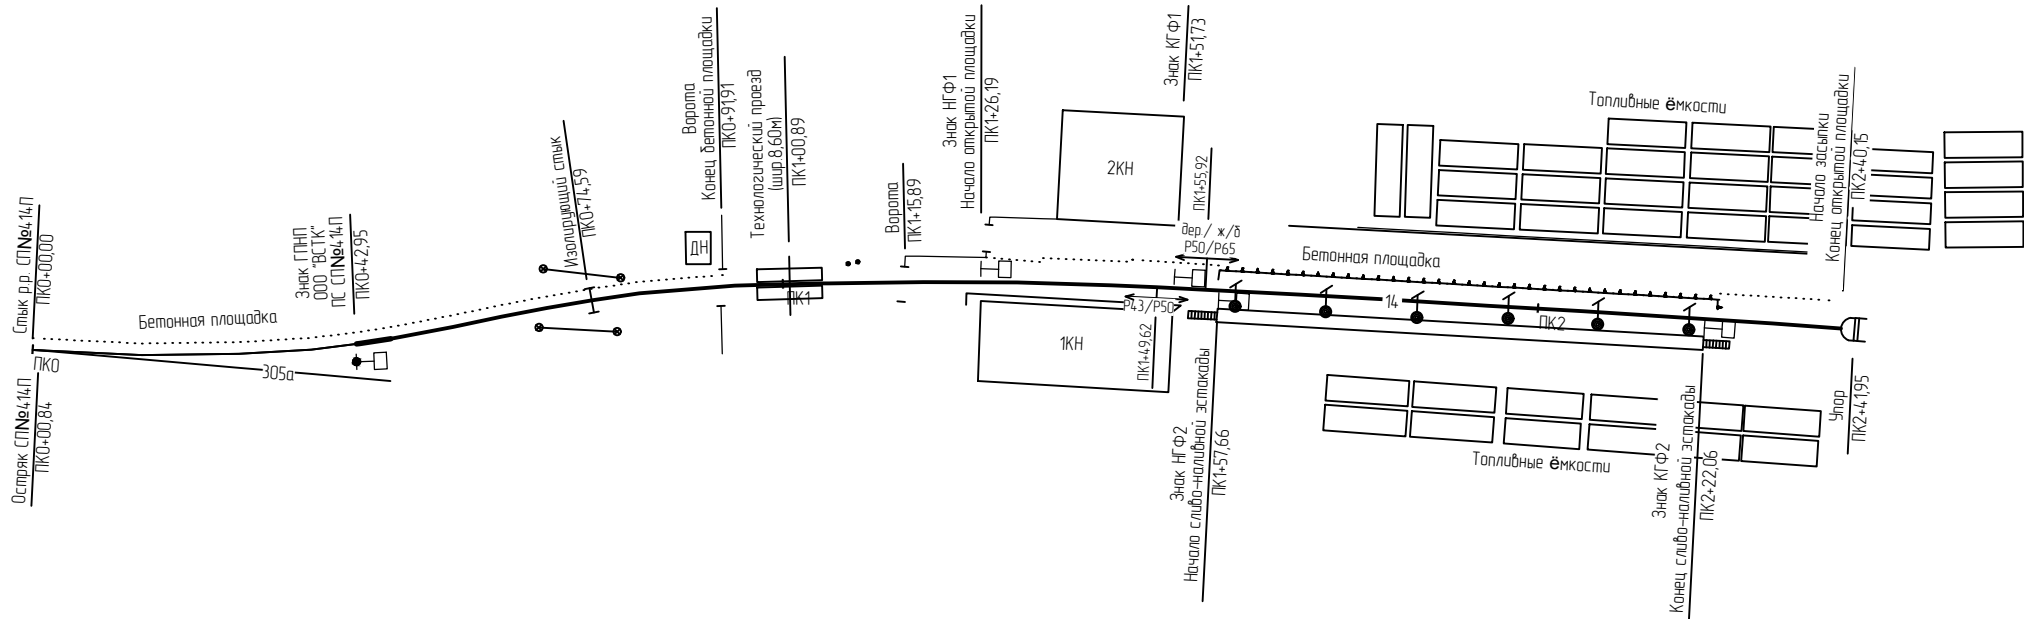

Ведомость ж.д. путей


№ пути	Наименование пути	Длина пути		Граница пути	
		полная	полезная	от	до
14	Погрузочно-выгрузочный	199,00	188,60	Знак ГПНП ООО "ВСТК" ПС СП№414П ПК0+42,95	Упор ПК2+41,95

Примечание:

- 1.Инструментальная съемка железнодорожного пути необщего пользования N14 ООО "ВСТК" выполнена сотрудниками Забтранспроект в августе 2020 года с использованием электронного тахеометра Leica TCR405.
- 2.Пикетаж разбит от стыка рамного рельса СП414П (ПК0+00,00).
3. Произведена замена наименования предприятия с ИП Швалов АА на ООО "ВСТК" (ООО "Восточно-Сибирская Торговая Компания").

Ведомость габаритов


Номер	Тип сооружения	Путь	Пикет	Габарит лево/право
1	Ворота	14	ПК0+91,91	2,32/2,51
2	Ворота	14	ПК1+15,89	2,08/2,57
3	Эстакада	14	ПК1+57,66 ПК2+22,06	-/2,43 -/2,30

 						2008-ТП-ГЧ			
1	-	Егизарян Н.А.			11.24	Путь необщего пользования N14 ООО "Восточно-Сибирская Торговая Компания"			
Изм.	Кол.	Лист	№ док.	Подпись	Дата				
Рук.работ		Афанасенко С.Н.			08.20	Станция Чита-I			
Инженер		Егизарян Н.А.			08.20				
						Стадия		Лист	Листов
						РП		1	2
						План пути N14		ООО "Забтранспроект" 2020г.	
Н.контр.		Афанасенко С.Н.			08.20				

Инд. N подл.	2008-ТП-ГЧ
Подпись и дата	
Взам. инд. N	


Нестандартный пикет
Ситуация
РЕЛЬСЫ
ШПАЛЫ
Разница отметок фактических и спрямленных уклонов, см
Отметки головки рельсов по спрямленным уклонам, м
Длина, м
Спрямоленные уклоны, ‰
Фактические уклоны, ‰
Фактические отметки головки рельсов, м
Отметки земляного полотна, м
Расстояния, м
Пикеты
План пути

Масштаб по горизонтали 1:1000
по вертикали 1:100

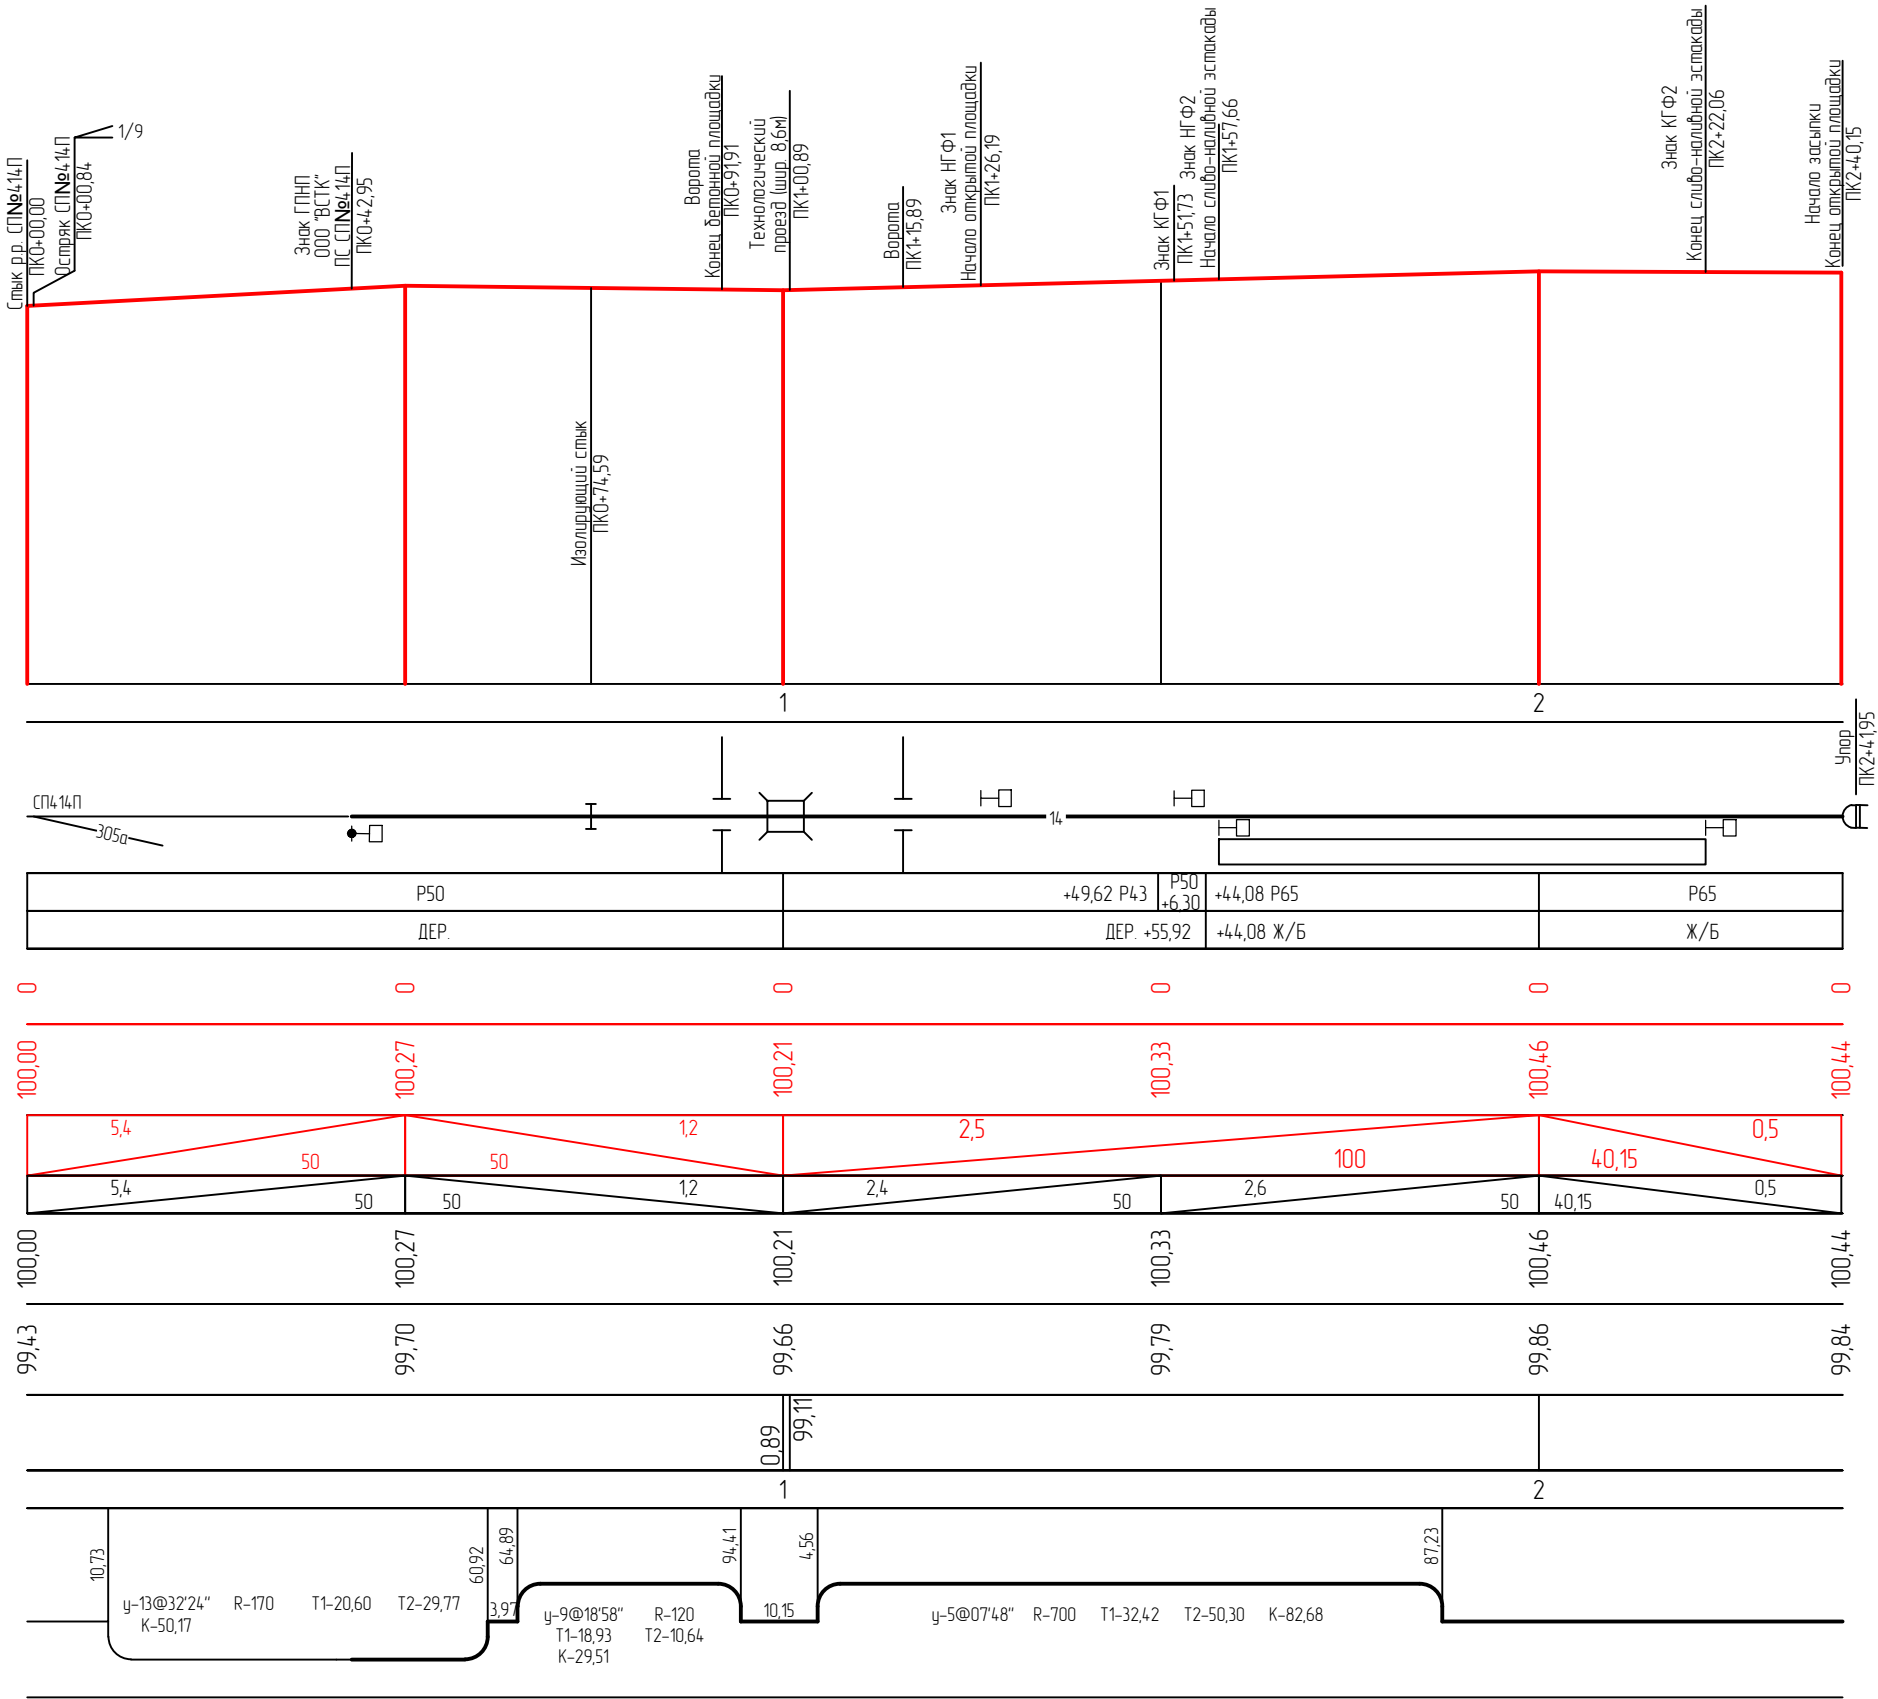

Примечание:

- Инструментальная съемка железнодорожного пути необщего пользования N14 ООО "ВСТК" выполнена сотрудниками Забтранспроект в августе 2020 года с использованием электронного тахеометра Leica TCR405.
- Пикетаж разбит от стыка рамного рельса СП414П (ПК0+00,00).
- Система высот условная. За отметку 100,00 принята поверхность катания головки рельса у стыка рамного рельса СП414П.
- Произведена замена наименования предприятия с ИП Швалов АА на ООО "ВСТК" (ООО "Восточно-Сибирская Торговая Компания").

 						2008-ТП-ГЧ			
1	-	Егизарян Н.А.			11.24	Путь необщего пользования №14 ООО "Восточно-Сибирская Торговая Компания"			
Изм.	Кол.	Лист	Ндок.	Подпись	Дата				
Рук.работ		Афанасенко С.Н.			08.20	Станция Чита-I			
Инженер		Егизарян Н.А.			08.20				
						Стадия	Лист	Листов	
						РП	2	2	
						Продольный профиль пути №14		ООО "Забтранспроект" 2020г.	
Н.контр.		Афанасенко С.Н.			08.20				