



Акционерное общество «Научно-исследовательский институт
железнодорожного транспорта»

ТЕХНИЧЕСКИЙ ПАСПОРТ

железнодорожного пути
необщего пользования
ООО «МеталлСнаб»
Путь №2

ст. Чита-I

2510-ТП

Инженер геодезист

Егиазарян Н.А.

Чита,
2025

Взам. Инв. №	
Подп. и дата	
Инв. № подл.	2510-ТП

ОБЩИЕ СВЕДЕНИЯ

Место примыкания железнодорожного пути необщего пользования:

железнодорожный путь необщего пользования №2 ООО «МеталлСнаб» примыкает стрелочным переводом №561 к железнодорожному пути ЭЧ-1 ст. Чита-I Забайкальской железной дороги

Границы железнодорожного пути необщего пользования:

предельный столбик стрелочного перевода №561 (ПК0+43,56)

Наличие предохранительных устройств:

Ручной сбрасывающий башмак СБР№583а (сброс вправо) ПК1+04,86

Дата заключения договора на эксплуатацию железнодорожного пути необщего пользования и срок его действия:

Порядок подачи и уборки вагонов (кем производится – железной дорогой, средствами предприятия или маневровым порядком), серия локомотива, применяемого при подаче и уборке вагонов:

подача и уборка вагонов на путь необщего пользования №2 ООО «МеталлСнаб» осуществляется маневровым порядком локомотивами серии ТЭМ2, ТЭМ18 ст. Чита-I Забайкальской железной дороги.

Взам. Инв. №		Подп. и дата													
Инв. №подл.	2510-ТП	Изм.	Коп.уч.	Лист	№ док.	Подп.	Дата	2510– ТП				Стадия	Лист	Листов	
		Разработал		Егизарян				Технический паспорт железнодорожного пути необщего пользования №2 ООО «МеталлСнаб»					1	12	
АО «ВНИИЖТ»															

1 ХАРАКТЕРИСТИКА ПУТИ

Таблица 1.1 – Примыкания других железнодорожных путей к железнодорожным путям предприятия

Наименование предприятия	Место примыкания (пикет, стрелка)	Длина путей км.	Предприятие, обслуживающее путь необщего пользования
--------------------------	-----------------------------------	-----------------	--

Таблица 1.2 - Ведомость железнодорожных путей предприятия

№ пути	Граница путей		Специализация	Дата внесения изменений	Ф.И.О. должность внесшего изменения	Подпись
	от	до				
2	ПС СП561 Знак ГППП ООО «МеталлСнаб» ПК0+43,56	Упор ПК2+12,56	Погрузочно-выгрузочный	10.2025	Егиазарян Н.А.	

Таблица 1.3 – Данные по длине путей

№ пути	Граница путей		Длины путей, м		Дата внесения изменений	Ф.И.О. должность внесшего изменения	Подпись
	от	до	полная	полезная			
2	ПС СП561 Знак ГППП ООО «МеталлСнаб» ПК0+43,56	Упор ПК2+12,56	169,00	115,10	10.2025	Егиазарян Н.А.	
ИТОГО			169,00	115,10*			

**полезная длина рассчитана от ПС СП583 до начала засыпки*

Изм.	Кол.уч.	Лист	№ док.	Подп.	Дата
Инва. № подл.	2510-ТП				
Подп. и дата					
Взам. Инв. №					

2 НИЖНЕЕ СТРОЕНИЕ ПУТИ И ИСКУССТВЕННЫЕ СООРУЖЕНИЯ

Таблица 2.1 – Наличие насыпей или выемок

№ пути	Граница путей		Наличие насыпей право/лево	Дата внесения изменений	Ф.И.О. должность внесшего изменения	Подпись
	от пикета	до пикета				
2	ПС СП561 Знак ГПНП ООО «МеталлСнаб» ПК0+43,56	Упор ПК2+12,56	нет	10.2025	Егиазарян Н.А.	

Таблица 2.2 – Наличие водоотводных сооружений

№ пути	Граница путей		Водоотводное устройство право/лево	Дата внесения изменений	Ф.И.О. должность внесшего изменения	Подпись
	от пикета	до пикета				
2	ПС СП561 Знак ГПНП ООО «МеталлСнаб» ПК0+43,56	Упор ПК2+12,56	нет	10.2025	Егиазарян Н.А.	

Таблица 2.3 – Деформация земляного полотна

№ пути	Граница путей		Тип деформации право/лево	Дата внесения изменений	Ф.И.О. должность внесшего изменения	Подпись
	от пикета	до пикета				
2	ПС СП561 Знак ГПНП ООО «МеталлСнаб» ПК0+43,56	Упор ПК2+12,56	нет	10.2025	Егиазарян Н.А.	

Таблица 2.4 – Искусственные сооружения

№ пути	Граница путей		Вид искусственного сооружения	Дата внесения изменений	Ф.И.О. должность внесшего изменения	Подпись
	от пикета	до пикета				
2	ПС СП561 Знак ГПНП ООО «МеталлСнаб» ПК0+43,56	Упор ПК2+12,56	нет	10.2025	Егиазарян Н.А.	

Таблица 2.5 – Пересечения с автомобильными дорогами

№ пути	от пикета	до пикета	Вид пересечения	Дата внесения изменений	Ф.И.О. должность внесшего изменения	Подпись
2	ПС СП561 Знак ГПНП ООО «МеталлСнаб» ПК0+43,56	Упор ПК2+12,56	нет	10.2025	Егиазарян Н.А.	

Инв. №подл.	2510-ТП
Подп. и дата	
Взам. Инв. №	

Изм.	Кол.уч.	Лист	№ док.	Подп.	Дата	2510 – ТП	Лист
							3

3 ВЕРХНЕЕ СТРОЕНИЕ ПУТИ

Таблица 3.1 – Род балласта в балластном слое

№ пути	Граница путей		Род балласта	Дата внесения изменений	Ф.И.О. должность внесшего изменения	Подпись
	от пикета	до пикета				
2	ПС СП561 Знак ГПНП ООО «МеталлСнаб» ПК0+43,56	Упор ПК2+12,56	щебень	10.2025	Егиазарян Н.А.	

Таблица 3.2 – Толщина балластного слоя

№ пути	Граница путей		Толщина	Дата внесения изменений	Ф.И.О. должность внесшего изменения	Подпись
	от пикета	до пикета				
2	ПС СП561 Знак ГПНП ООО «МеталлСнаб» ПК0+43,56	Упор ПК2+12,56	10-15 см	10.2025	Егиазарян Н.А.	

Таблица 3.3 – Загрязнение балластного слоя

№ пути	Граница путей		Загрязнение	Дата внесения изменений	Ф.И.О. должность внесшего изменения	Подпись
	от пикета	до пикета				
2	ПС СП561 Знак ГПНП ООО «МеталлСнаб» ПК0+43,56	Упор ПК2+12,56	до 10%	10.2025	Егиазарян Н.А.	

Таблица 3.4 – Загрязняемость балластного слоя

№ пути	Граница путей		Загрязняемость	Дата внесения изменений	Ф.И.О. должность внесшего изменения	Подпись
	от пикета	до пикета				
2	ПС СП561 Знак ГПНП ООО «МеталлСнаб» ПК0+43,56	Упор ПК2+12,56	до 5%	10.2025	Егиазарян Н.А.	

Таблица 3.5 – Эпюра шпал, количество шпал в пути, материал шпал

№ пути	Граница путей		Эпюра, количество материал	Дата внесения изменений	Ф.И.О. должность внесшего изменения	Подпись
	от пикета	до пикета				
Шпалы – эпюра 1600 шп/км						
2	ПС СП561 Знак ГПНП ООО «МеталлСнаб» ПК0+43,56	Упор ПК2+12,56	220 шп – дер	10.2025	Егиазарян Н.А.	
Итого		Шпалы: дер – 200 шп				

Взам. Инв. №	
Подп. и дата	
Инв. №подл.	2510-ТП

Изм.	Кол.уч.	Лист	№ док.	Подп.	Дата	2510 – ТП		Лист
								4

Таблица 3.9 – Тип рельсов

№ пути	Граница путей		Тип рельсов, длина, м.	Дата внесения изменений	Ф.И.О. должность внесшего изменения	Подпись
	от пикета	до пикета				
2	ПС СП561 Знак ГПНП ООО «МеталлСнаб» ПК0+43,56	Упор ПК2+12,56	P50 137,94мх2	10.2025	Егиазарян Н.А.	
Итого		Рельсы P65 –275,88 м				

Таблица 3.7 – Наличие сварных стыков

№ пути	Граница путей		Наличие сварных стыков	Дата внесения изменений	Ф.И.О. должность внесшего изменения	Подпись
	от пикета	до пикета				
2	ПС СП561 Знак ГПНП ООО «МеталлСнаб» ПК0+43,56	Упор ПК2+12,56	нет	10.2025	Егиазарян Н.А.	

Таблица 3.8 – Ведомость стрелочных переводов

№ Стрелочного перевода	Вид стрелочного перевода, отклонение	Тип и марка стрелочного перевода	Полная длина, м	Дата внесения изменений	Ф.И.О. должность внесшего изменения	Подпись
-				10.2025	Егиазарян Н.А.	

Таблица 3.9 – Верхнее строение пути на стрелочных переводах

№ стрелочного перевода	Тип рельсов	Подрельсовое основание		Вид балласта	Дата внесения изменений	Ф.И.О. должность внесшего изменения	Подпись
		Шпалы	Брус				
-					10.2025	Егиазарян Н.А.	

Таблица 3.10 – Стыковые скрепления

№ пути	Накладки		Количество стыковых болтов	Дата внесения изменений	Ф.И.О. должность внесшего изменения	Подпись
	тип	Кол-во				
2	Двухголовые P50	48	192	10.2025	Егиазарян Н.А.	

Взам. Инв. №	
Подп. и дата	
Инв. №подл.	2510-ТП

						2510 – ТП				Лист
Изм.	Кол.уч.	Лист	№ док.	Подп.	Дата					5

Таблица 3.11 – Промежуточные скрепления

№ пути	Промежуточное скрепление		Дата внесения изменений	Ф.И.О. должность внесшего изменения	Подпись
	Подкладки, шт	Прикрепители, шт			
2	440	1760	10.2025	Егиазарян Н.А.	

Таблица 3.12 – Закрепление от угона

№ пути	Граница путей		Количество/ тип противоугонов	Дата внесения изменений	Ф.И.О. должность внесшего изменения	Подпись
	от пикета	до пикета				
2	ПС СП561 Знак ГППП ООО «МеталлСнаб» ПК0+43,56	Упор ПК2+12,56	нет	10.2025	Егиазарян Н.А.	

Инв. №подл.	2510-ТП
Подп. и дата	
Взам. Инв. №	

4 ТЕХНИЧЕСКОЕ ОСНАЩЕНИЕ ГРУЗОВОГО ФРОНТА

Наличие договора на подачу/уборку вагонов: _____

Наличие лицензии: _____

Наличие таможенных складов временного хранения: _____

Таблица 4.1 – Вместимость грузовых фронтов

№ грузового фронта	Наименование. Грузового фронта	Местоположение			Длина, м.	Вместимость, физ. ваг.
		№ пути	от пикета	до пикета		
ГФ1	Рампа (справа)	2	ПК1+10,00	ПК1+60,33	50,33	3 кр.
ГФ2	Открытая площадка (справа)	2	ПК1+80,56	ПК2+10,56	30,0	2 кр.,пв.

Технико-технологическая характеристика грузовых фронтов:

ГФ1 – рампа (справа)

Среднесуточный вагонооборот (максимальный) – 3 вагона.

Перечень перерабатываемых грузов – выгрузка: тарно-штучные грузы (цемент в мешках 50кг, цемент в МКР 1т, шпатлевка в мешках 50кг), металлопрокат, строительные материалы (кирпич, ГКЛ, ДВП, ДСП, ОСП).

Перечень перерабатываемых опасных грузов – нет.

Средства механизации – фронтальный погрузчик MINGYU 30-Q25K2, грузоподъемность 3т.

ГФ2 – открытая площадка (справа)

Среднесуточный вагонооборот (максимальный) – 2 вагона.

Перечень перерабатываемых грузов – выгрузка: тарно-штучные грузы (цемент в мешках 50кг, цемент в МКР 1т, шпатлевка в мешках 50кг), металлопрокат, строительные материалы (кирпич, ГКЛ, ДВП, ДСП, ОСП).

Перечень перерабатываемых опасных грузов – нет.

Средства механизации – фронтальный погрузчик MINGYU 30-Q25K2, грузоподъемность 3т.

Технический паспорт составлен на основании имеющихся документов и результатов инструментальной съемки и фактического состояния пути.

Данный технический паспорт предназначен только для разработки инструкции о порядке обслуживания и организации движения на железнодорожном пути необщего пользования ООО «МеталлСнаб».

Данный технический паспорт не устанавливает права собственности на железнодорожные пути, стрелочные переводы.

Инженер геодезист

Егиазарян Н.А.

Взам. Инв. №	
Подп. и дата	
Инв. №подл.	2510-ТП

Изм.	Кол.уч.	Лист	№ док.	Подп.	Дата

2510 – ТП

Лист

7



АССОЦИАЦИЯ САМОРЕГУЛИРУЕМЫХ ОРГАНИЗАЦИЙ ОБЩЕРОССИЙСКАЯ НЕГОСУДАРСТВЕННАЯ НЕКОММЕРЧЕСКАЯ ОРГАНИЗАЦИЯ – ОБЩЕРОССИЙСКОЕ МЕЖОТРАСЛЕВОЕ ОБЪЕДИНЕНИЕ РАБОТОДАТЕЛЕЙ «НАЦИОНАЛЬНОЕ ОБЪЕДИНЕНИЕ САМОРЕГУЛИРУЕМЫХ ОРГАНИЗАЦИЙ, ОСНОВАННЫХ НА ЧЛЕНСТВЕ ЛИЦ, ВЫПОЛНЯЮЩИХ ИНЖЕНЕРНЫЕ ИЗЫСКАНИЯ, И САМОРЕГУЛИРУЕМЫХ ОРГАНИЗАЦИЙ, ОСНОВАННЫХ НА ЧЛЕНСТВЕ ЛИЦ, ОСУЩЕСТВЛЯЮЩИХ ПОДГОТОВКУ ПРОЕКТНОЙ ДОКУМЕНТАЦИИ»

7717596862-20240515-1228

(регистрационный номер выписки)

15.05.2024

(дата формирования выписки)

ВЫПИСКА

из единого реестра сведений о членах саморегулируемых организаций в области инженерных изысканий и в области архитектурно-строительного проектирования и их обязательствах

Настоящая выписка содержит сведения о юридическом лице (индивидуальном предпринимателе), осуществляющем подготовку проектной документации:

Акционерное общество "Научно-исследовательский институт железнодорожного транспорта"

(полное наименование юридического лица/ФИО индивидуального предпринимателя)

1077758910900

(основной государственный регистрационный номер)

1. Сведения о члене саморегулируемой организации:

1.1	Идентификационный номер налогоплательщика	7717596862
1.2	Полное наименование юридического лица (Фамилия Имя Отчество индивидуального предпринимателя)	Акционерное общество "Научно-исследовательский институт железнодорожного транспорта"
1.3	Сокращенное наименование юридического лица	АО "ВНИИЖТ"
1.4	Адрес юридического лица Место фактического осуществления деятельности (для индивидуального предпринимателя)	129626, Россия, Москва, г. Москва, ул. 3-я Мытищинская, д. 10
1.5	Является членом саморегулируемой организации	Ассоциация в области архитектурно-строительного проектирования «Саморегулируемая организация «СОВЕТ ПРОЕКТИРОВЩИКОВ» (СРО-П-011-16072009)
1.6	Регистрационный номер члена саморегулируемой организации	П-011-007717596862-1309
1.7	Дата вступления в силу решения о приеме в члены саморегулируемой организации	14.06.2018
1.8	Дата и номер решения об исключении из членов саморегулируемой организации, основания исключения	

2. Сведения о наличии у члена саморегулируемой организации права осуществлять подготовку проектной документации:

2.1 в отношении объектов капитального строительства (кроме особо опасных, технически сложных и уникальных объектов, объектов использования атомной энергии) (дата возникновения/изменения права)	2.2 в отношении особо опасных, технически сложных и уникальных объектов капитального строительства (кроме объектов использования атомной энергии) (дата возникновения/изменения права)	2.3 в отношении объектов использования атомной энергии (дата возникновения/изменения права)
Да, 14.06.2018	Нет	Нет



1

Инв. №подл.	2510-ТП
Подп. и дата	
Взам. Инв. №	

Изм.	Кол.уч.	Лист	№ док.	Подп.	Дата

2510 – ТП

Лист

8

3. Компенсационный фонд возмещения вреда		
3.1	Уровень ответственности члена саморегулируемой организации по обязательствам по договору подряда на подготовку проектной документации, в соответствии с которым указанным членом внесен взнос в компенсационный фонд возмещения вреда	Третий уровень ответственности (не превышает триста миллионов рублей)
3.2	Сведения о приостановлении / прекращении права осуществлять подготовку проектной документации объектов капитального строительства	
4. Компенсационный фонд обеспечения договорных обязательств		
4.1	Дата, с которой член саморегулируемой организации имеет право осуществлять подготовку проектной документации по договорам подряда, заключаемым с использованием конкурентных способов заключения договоров, в соответствии с которым указанным членом внесен взнос в компенсационный фонд обеспечения договорных обязательств	14.06.2018
4.2	Уровень ответственности члена саморегулируемой организации по обязательствам по договорам подряда на подготовку проектной документации, заключаемым с использованием конкурентных способов заключения договоров, в соответствии с которым указанным членом внесен взнос в компенсационный фонд обеспечения договорных обязательств	Второй уровень ответственности (не превышает пятьдесят миллионов рублей)
4.3	Дата уплаты дополнительного взноса	Нет
4.4	Сведения о приостановлении / прекращении права осуществлять подготовку проектной документации по договорам подряда, заключаемым с использованием конкурентных способов заключения договоров	
5. Фактический совокупный размер обязательств		
5.1	Фактический совокупный размер обязательств по договорам подряда на подготовку проектной документации, заключаемым с использованием конкурентных способов заключения договоров на дату выдачи выписки	Нет

Руководитель аппарата



ДОКУМЕНТ ПОДПИСАН УСИЛЕННОЙ КВАЛИФИЦИРОВАННОЙ
ЭЛЕКТРОННОЙ ПОДПИСЬЮ

Владелец: Кожуховский Алексей Олегович
123056, г. Москва, ул. 2-я Брестская, д. 5
СЕРТИФИКАТ 0402FE9100C0B0148D4019113D8DEA876F
ДЕЙСТВИТЕЛЕН: С 20.11.2023 ПО 20.11.2024

А.О. Кожуховский

2



Взам. Инв. №	
Подп. и дата	
Инв. №подл.	2510-ТП

Изм.	Кол.уч.	Лист	№ док.	Подп.	Дата

**СИСТЕМА ДОБРОВОЛЬНОЙ СЕРТИФИКАЦИИ
«ТЕХНОПРОГРЕСС»
ЗАРЕГИСТРИРОВАНА ФЕДЕРАЛЬНЫМ АГЕНТСТВОМ
ПО ТЕХНИЧЕСКОМУ РЕГУЛИРОВАНИЮ И МЕТРОЛОГИИ
РЕГИСТРАЦИОННЫЙ НОМЕР РОСС RU.3293.04TX00**

Орган по сертификации
Общество с ограниченной ответственностью "РусПромГрупп"
Регистрационный номер СДС.ТП.ОС.001136-21

СЕРТИФИКАТ СООТВЕТСТВИЯ

№ СДС.ТП.СМ.18419-22

СМК сертифицирована с сентября 2019

выдан **Акционерному обществу "Научно-исследовательский
институт железнодорожного транспорта" (АО "ВНИИЖТ")**

г.Москва, ул.3-я Мытищинская, д.10

ИНН 7717596862


НАСТОЯЩИЙ СЕРТИФИКАТ УДОСТОВЕРЯЕТ

Система Менеджмента Качества

применительно к работам по подготовке проектной документации,
которые оказывают влияние на безопасность объектов капитального
строительства (кроме особо опасных, технически сложных и уникальных
объектов капитального строительства, объектов использования атомной
энергии); научным исследованиям и разработкам в области
естественных и технических наук


**СООТВЕТСТВУЕТ ТРЕБОВАНИЯМ
ГОСТ Р ИСО 9001-2015 (ISO 9001:2015)**

Дата выдачи
23 сентября 2022 года

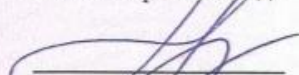
Э.В. Алексеева
Руководитель органа
по сертификации



Срок действия до
23 сентября 2025 года

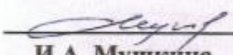
И.А. Мушкина
Руководитель
группы по аудиту

Настоящий сертификат обязывает организацию поддерживать состояние выполняемых работ
в соответствии с вышеуказанным стандартом, что будет находиться под контролем органа по сертификации системы
«ТЕХНОПРОГРЕСС» и подтверждаться при прохождении ежегодного инспекционного контроля

072856

Инв. №подл.	2510-ТП
Подп. и дата	
Взам. Инв. №	

Изм.	Кол.уч.	Лист	№ док.	Подп.	Дата

2510 – ТП

Лист

10

СЕРТИФИКАТ ОБЯЗЫВАЕТ ЕГО ВЛАДЕЛЬЦА:

- поддерживать состояние выполняемых работ в соответствии с указанным стандартом, что будет находиться под контролем органа по сертификации и подтверждаться при прохождении ежегодного инспекционного контроля
- обеспечить соответствие объекта требованиям документов, на соответствие которым он был сертифицирован
- создавать условия для проведения органом по сертификации инспекционного контроля по правилам
- применять знак соответствия по правилам, установленным в СДС "ТЕХНОПРОГРЕСС"
- своевременно извещать Орган по сертификации, выдавший сертификат, о произошедших у владельца сертификата изменениях

Подтверждение проведения плановых проверок

Дата плановой
проверки

Подпись
Руководителя ОС

Печать

ruspromgroup.ru




Инв. №подл.	2510-ТП
Подп. и дата	
Взам. Инв. №	

Изм.	Кол.уч.	Лист	№ док.	Подп.	Дата

2510 – ТП

Лист

11

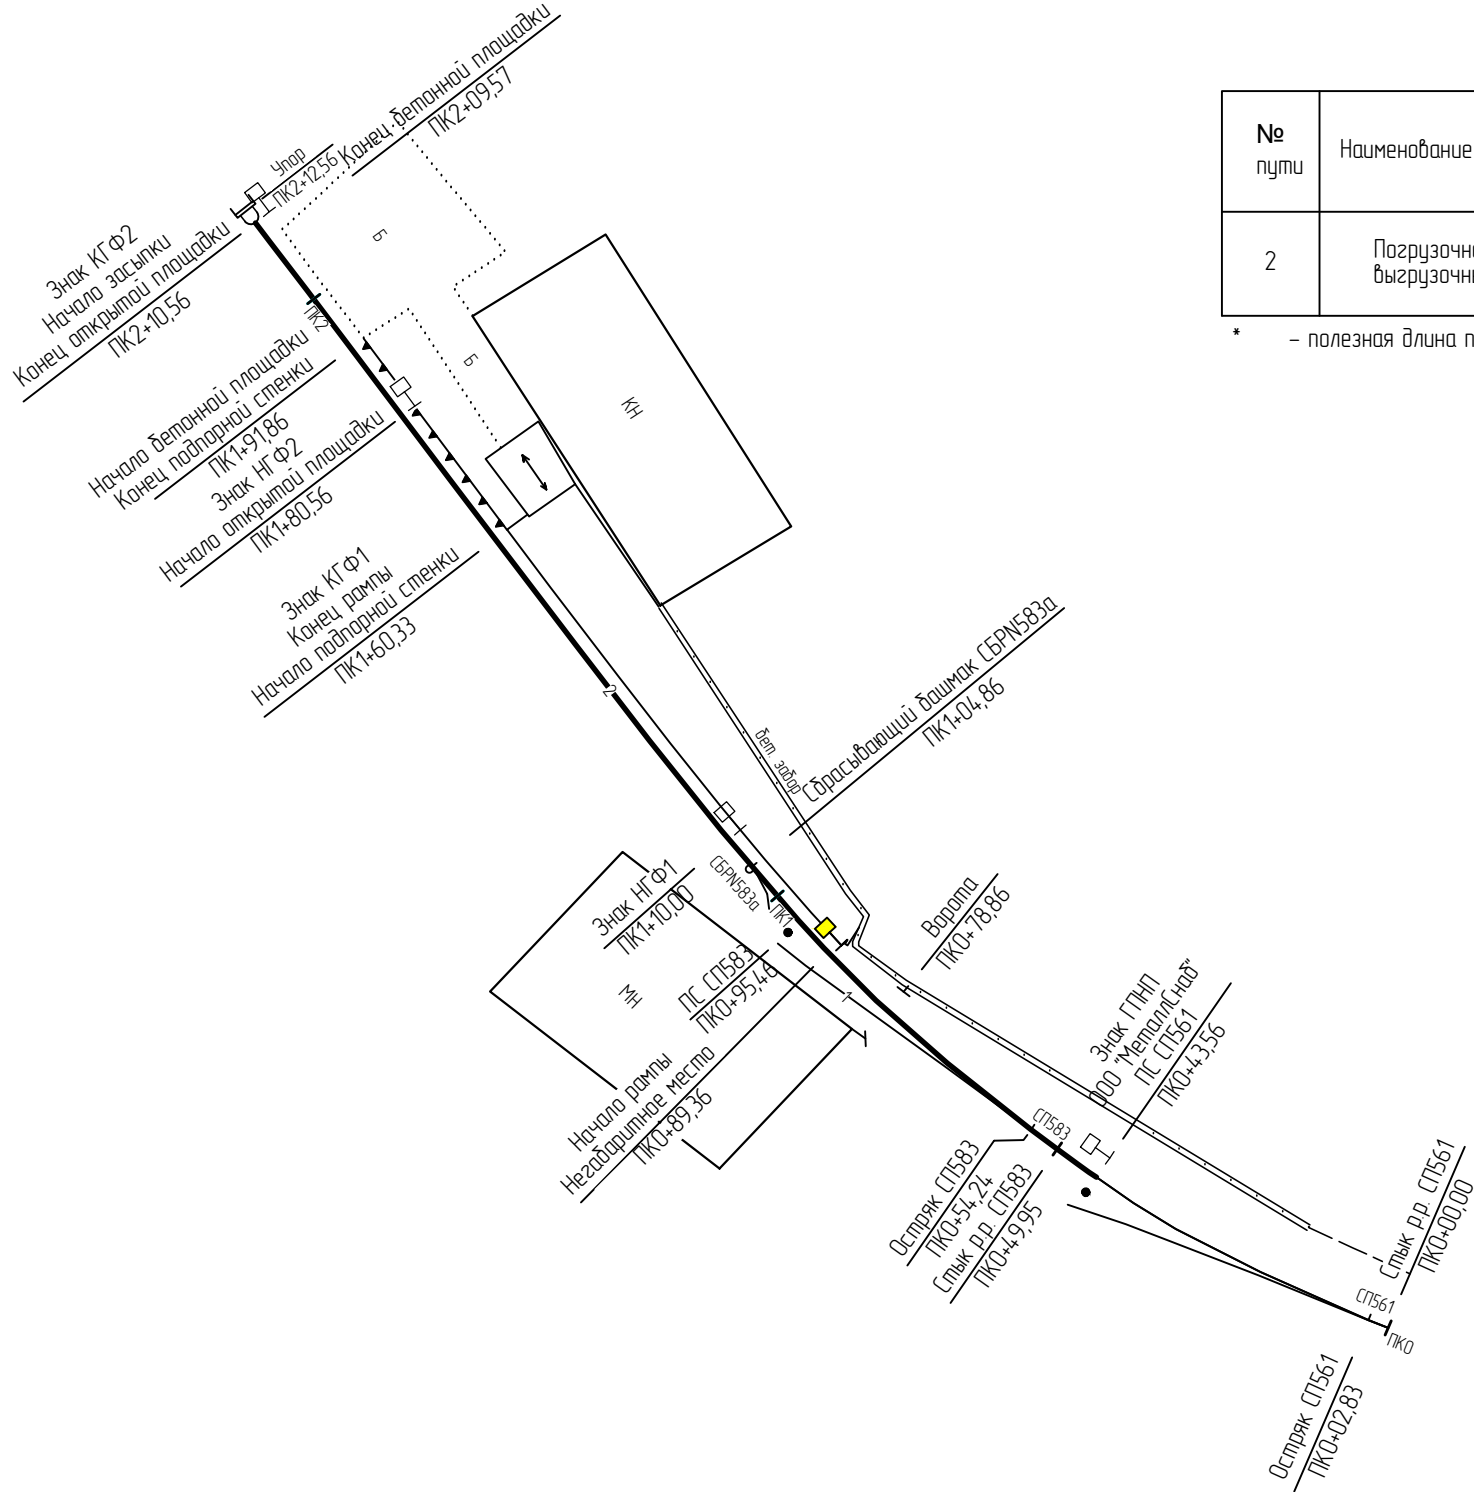

Ведомость ж.д. путей

№ пути	Наименование пути	Длина пути		Граница пути	
		полная	полезная	от	до
2	Погрузочно-выгрузочный	169,00	115,10*	ПС СП561 Знак ГПНП ООО "МеталлСнаб" ПК0+43,56	Упор ПК2+12,56

* – полезная длина пути рассчитана от ПС СП583 до начала засыпки

Ведомость габаритов

Номер	Тип сооружения	Путь	Пикет	Габарит лево/право
1	Ворота	2	ПК0+78,86	3,05/3,30
2	Рампа	2	ПК0+89,36 ПК1+60,33	-/1,93 -/2,01
3	Подпорная стенка	2	ПК1+60,33 ПК1+91,86	-/2,01 -/2,13

Примечание:


- Инструментальная съемка железнодорожного пути необщего пользования N2 ООО "МеталлСнаб" выполнена в октябре 2025 года с использованием геодезической спутниковой аппаратуры типа PrinSe i90.
- Пикетаж разбит по оси пути N2 от стыка рамного рельса СП561 ПК0+00,00.

						2510–ТП–ГЧ			
Изм.	Кол.	Лист	Ндэк.	Подпись	Дата	Путь необщего пользования ООО "МеталлСнаб"			
Разработал		Егуазарян Н.А.			10.25	Станция Чита-I	Стадия	Лист	Листов
								1	2
						План пути N2	АО "ВНИИЖТ" 2025г.		
Н.контр.		Егуазарян Н.А.			10.25				

Нестандартный пикет	
Ситуация	
Тип рельса	
Тип шпал	
Разница отметок фактических и спрямленных уклонов, см	
Отметки головки рельсов по спрямленным уклонам, м	
Длина, м	Спрямленные уклоны, ‰
Фактические уклоны, ‰	
Фактические отметки головки рельсов, м	
Отметки земляного полотна, м	
Расстояния, м	
Пикеты	
План пути N2	
Километры	

Примечание:

1. Инструментальная съемка железнодорожного пути необщего пользования N2 ООО "МеталлСнаб" выполнена в октябре 2025 года с использованием геодезической спутниковой аппаратуры типа PrinCe i90.
2. Пикетаж разбит по оси пути N2 от стыка рамного рельса СП561 ПК0+00,00.
3. Система высот условная.

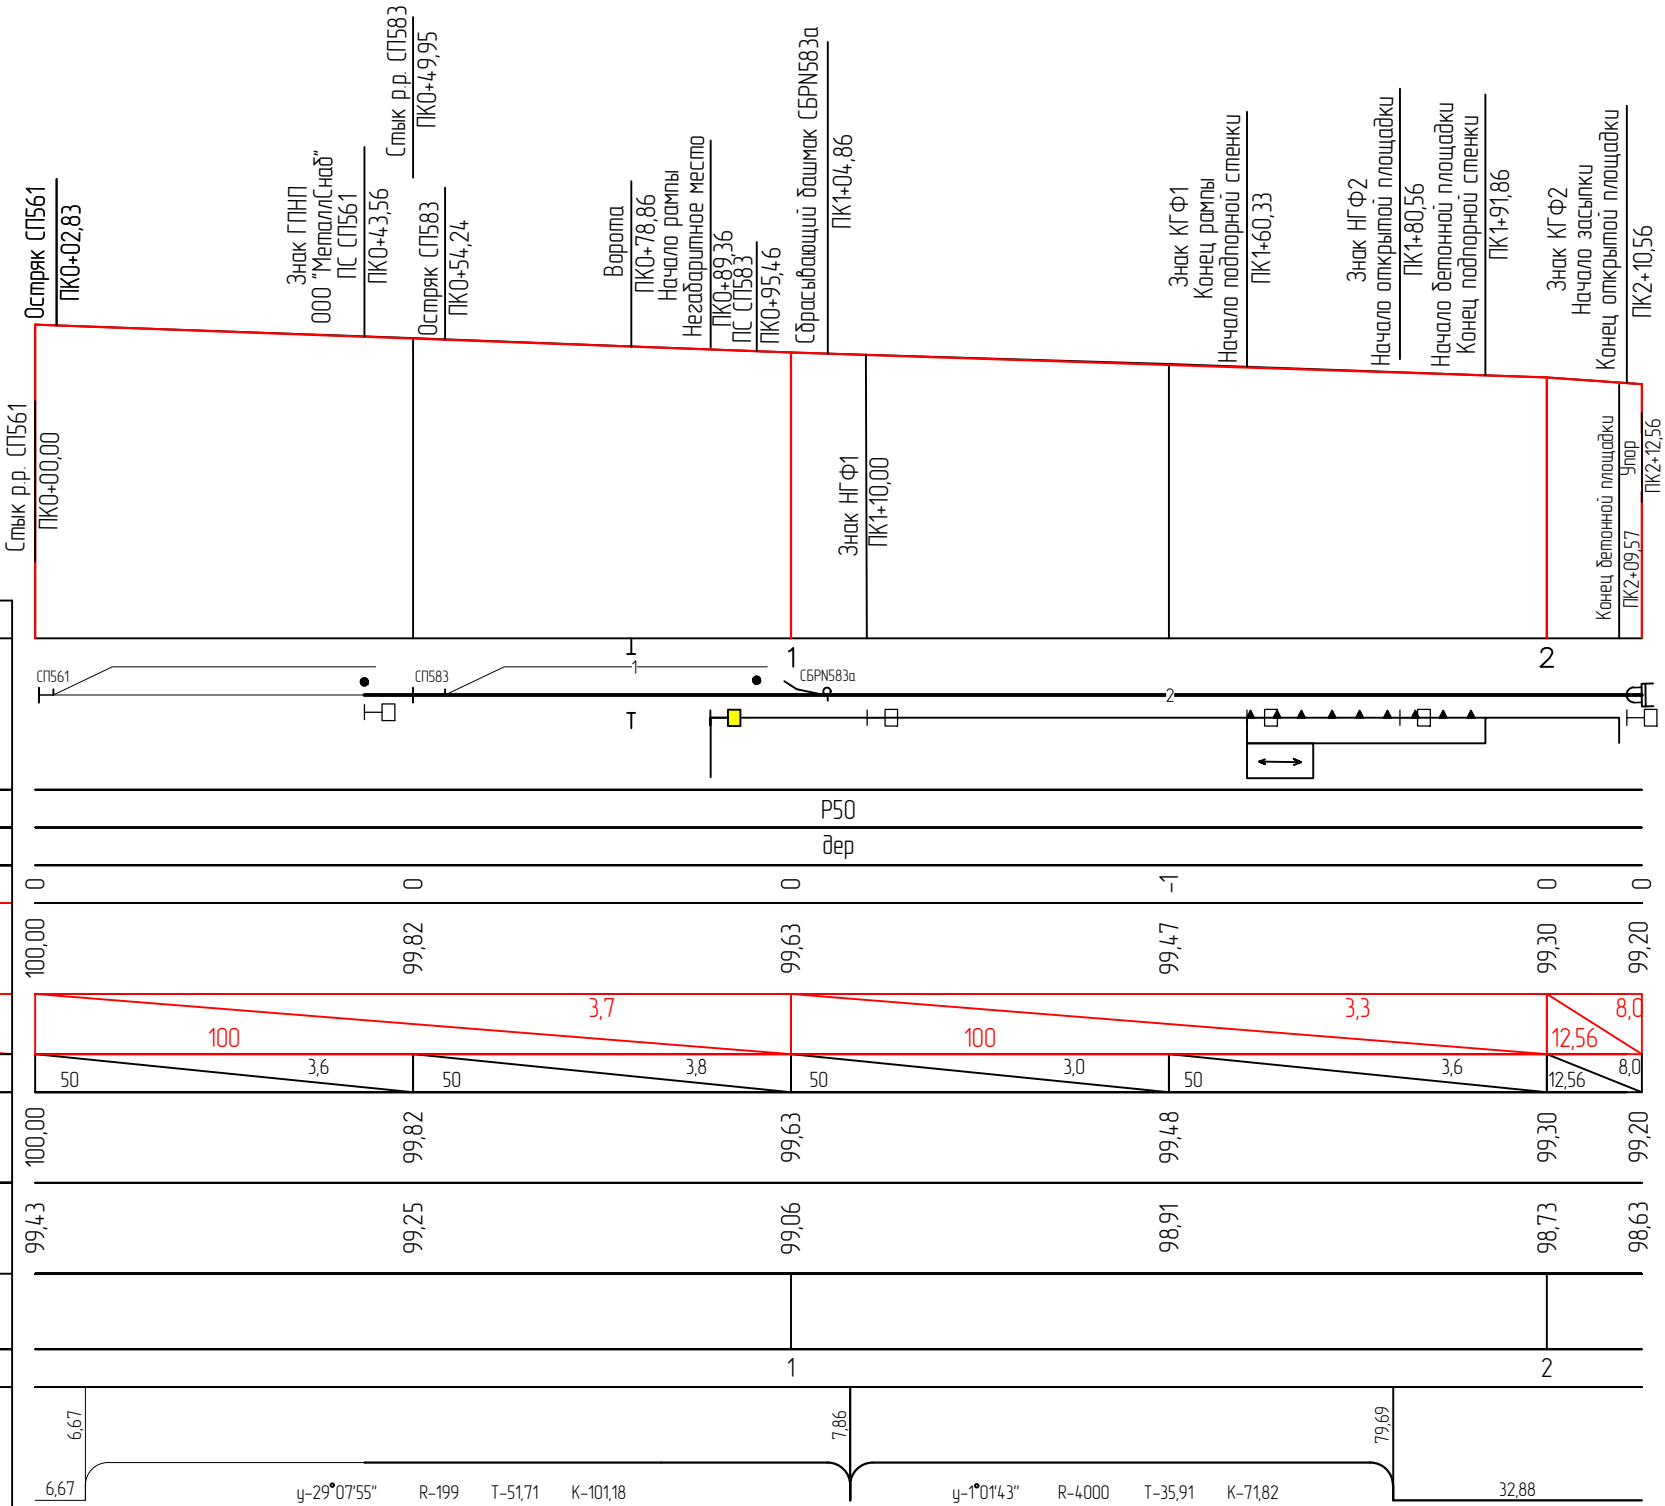

						2510-ТП-ГЧ				
						Путь неoadщего пользования				
Изм.	Кол.	Лист	№док.	Подпись	Дата	ООО "МеталлСнаб"				
Разработал		Егуазарян Н.А.			10.25	Станция Чита-I		Стадия	Лист	Листов
								2	2	
						Продольный профиль пути N2		АО "ВНИИЖТ" 2025г.		
Н.контр.		Егуазарян Н.А.			10.25					