



ОБЩЕСТВО С ОГРАНИЧЕННОЙ ОТВЕТСТВЕННОСТЬЮ
«ЗАБТРАНСПРОЕКТ»

Свидетельство № 1266 от 7 марта 2017 г. СРО-И-032-22122011

ТЕХНИЧЕСКИЙ ПАСПОРТ

железнодорожного пути
необщего пользования
ООО «РОССЫПЬ»

Путь №22

Ст. Бада

2311-ТП

Главный инженер
ООО «Забтранспроект»

Афанасенко С.Н.

Ведущий инженер
ООО «Забтранспроект»

Егиазарян Н.А.

Чита, 2023

Взам. Инв. №	
Подп. и дата	
Инв. № подл.	2311-ТП

ОБЩИЕ СВЕДЕНИЯ

Место примыкания железнодорожного пути необщего пользования:

железнодорожный путь необщего пользования №22 ООО «РОССЫПЬ» находится на продолжении соединительного пути №5 ст. Бада Забайкальской железной дороги.

Границы железнодорожного пути необщего пользования:

границей железнодорожного пути необщего пользования №22 ООО «РОССЫПЬ» является знак «Граница пути необщего пользования» ПК2+27,08, установленный на въездных воротах предприятия.

Наличие предохранительных устройств:

Сбрасывающий башмак СБ02 ПК2+28,62 (сброс вправо).

Дата заключения договора на эксплуатацию железнодорожного пути необщего пользования и срок его действия:

Порядок подачи и уборки вагонов (кем производится – железной дорогой, средствами предприятия или маневровым порядком), серия локомотива, применяемого при подаче и уборке вагонов:

подача и уборка вагонов на пути необщего пользования ООО «РОССЫПЬ» осуществляется маневровым порядком локомотивами серии ТЭМ2, ТЭМ18 ст. Бада Забайкальской железной дороги.

Взам. Инв. №	
Подп. и дата	
Инв. №подл.	2311-ТП

						2311 – ТП			
Изм.	Кол.уч.	Лист	№ док.	Подп.	Дата				
Разработал		Егназарян				Технический паспорт железнодорожного пути необщего пользования ООО «РОССЫПЬ»			
Проверил		Афанасенко							
Стадия	Лист	Листов							
П	1	11	ООО «Забтранспроект»						

1 ХАРАКТЕРИСТИКА ПУТИ

Таблица 1.1 – Примыкания других железнодорожных путей к железнодорожным путям предприятия

Наименование предприятия	Место примыкания (пикет, стрелка)	Длина Путь км.	Предприятие обслуживающее путь необщего пользования
--------------------------	-----------------------------------	----------------	---

-

Таблица 1.2 - Ведомость железнодорожных путей предприятия

№ пути	Граница путей		Специализация	Дата внесения изменений	Ф.И.О. должность внесшего изменения	Подпись
	от	до				
22	Знак ГПНП ООО «РОССЫПЬ» ПК2+27,08	Упор ПК7+75,08	Погрузо-выгрузочный	11.2023	Афанасенко С.Н.	

Таблица 1.3 - Данные по длине путей

№ пути	Граница путей		Длины путей, м		Дата внесения изменений	Ф.И.О. должность внесшего изменения	Подпись
	от	до	полная	полезная			
22	Знак ГПНП ООО «РОССЫПЬ» ПК2+27,08	Упор ПК7+75,08	548,00	501,10	11.2023	Афанасенко С.Н.	
ИТОГО			548,00	501,10			

Изм. № подл.	Подп. и дата	Взам. Инв. №
2311-ТП		

Изм.	Кол.уч.	Лист	№ док.	Подп.	Дата

2311 – ТП

Лист

2

2 НИЖНЕЕ СТРОЕНИЕ ПУТИ И ИСКУССТВЕННЫЕ СООРУЖЕНИЯ

Таблица 2.1 - Наличие насыпей или выемок

№ пути	Граница путей		Наличие выемок/насыпей	Дата внесения изменени й	Ф.И.О. должность внесшего изменения	Подпись
	от пикета	до пикета				
22	Знак ГПНП ООО «РОССЫПЬ» ПК2+27,08	Упор ПК7+75,08	нет	11.2023	Афанасенко С.Н.	

Таблица 2.2 - Наличие водоотводных сооружений

№ пути	Граница путей		Водоотводное устройство право/лево	Дата внесения изменений	Ф.И.О. должность внесшего изменения	Подпись
	от пикета	до пикета				
22	Знак ГПНП ООО «РОССЫПЬ» ПК2+27,08	Упор ПК7+75,08	нет	11.2023	Афанасенко С.Н.	

Таблица 2.3 - Деформация земляного полотна

№ пути	Граница путей		Тип деформации право/лево	Дата внесения изменений	Ф.И.О. должность внесшего изменения	Подпись
	от пикета	до пикета				
22	Знак ГПНП ООО «РОССЫПЬ» ПК2+27,08	Упор ПК7+75,08	нет	11.2023	Афанасенко С.Н.	

Таблица 2.4 - Искусственные сооружения

№ пути	Граница путей		Вид искусствен- ного сооружения	Дата внесения изменений	Ф.И.О. должность внесшего изменения	Подпись
	от пикета	до пикета				
22	Знак ГПНП ООО «РОССЫПЬ» ПК2+27,08	Упор ПК7+75,08	нет	11.2023	Афанасенко С.Н.	

Таблица 2.5 - Пересечения с автомобильными дорогами

№ пути	от пикета	до пикета	Вид пересечения	Дата внесения изменений	Ф.И.О. должность внесшего изменения	Подпись
22	Знак ГПНП ООО «РОССЫПЬ» ПК2+27,08	Упор ПК7+75,08	нет	11.2023	Афанасенко С.Н.	

Взам. Инв. №	
Подп. и дата	
Инв. № подл.	2311-ТП

Изм.	Кол.уч.	Лист	№ док.	Подп.	Дата	2311 – ТП		Лист
								3

3 ВЕРХНЕЕ СТРОЕНИЕ ПУТИ

Таблица 3.1 - Род балласта в балластном слое

№ пути	Граница путей		Род балласта	Дата внесения изменений	Ф.И.О. должность внесшего изменения	Подпись
	от пикета	до пикета				
22	Знак ГПНП ООО «РОССЫПЬ» ПК2+27,08	Упор ПК7+75,08	щебень	11.2023	Афанасенко С.Н.	

Таблица 3.2 - Толщина балластного слоя

№ пути	Граница путей		Толщина	Дата внесения изменений	Ф.И.О. должность внесшего изменения	Подпись
	от пикета	до пикета				
22	Знак ГПНП ООО «РОССЫПЬ» ПК2+27,08	Упор ПК7+75,08	10-15 см	11.2023	Афанасенко С.Н.	

Таблица 3.3 - Загрязнение балластного слоя

№ пути	Граница путей		Загрязнение	Дата внесения изменений	Ф.И.О. должность внесшего изменения	Подпись
	от пикета	до пикета				
22	Знак ГПНП ООО «РОССЫПЬ» ПК2+27,08	Упор ПК7+75,08	до 20%	11.2023	Афанасенко С.Н.	

Таблица 3.4 - Загрязняемость балластного слоя

№ пути	Граница путей		Загрязняе- мость	Дата внесения изменений	Ф.И.О. должность внесшего изменения	Подпись
	от пикета	до пикета				
22	Знак ГПНП ООО «РОССЫПЬ» ПК2+27,08	Упор ПК7+75,08	до 5%	11.2023	Афанасенко С.Н.	

Инв. № подл.	2311-ТП
Подп. и дата	
Взам. Инв. №	

Изм.	Кол.уч.	Лист	№ док.	Подп.	Дата	2311 – ТП	Лист
							4

Таблица 3.5 - Эпюра шпал, количество шпал в пути, материал шпал

№ пути	Граница путей		Эпюра, количество материал	Дата внесения изменений	Ф.И.О. должность внесшего изменения	Подпись
	от пикета	до пикета				
22	Шпалы – эпюра 1840 шп/км			11.2023	Афанасенко С.Н.	
	Знак ГПНП ООО «РОССЫПЬ» ПК2+27,08	ПК2+34,60	14 шп – дер.			
	Шпалы – эпюра 2000 шп/км					
	ПК2+34,60	ПК2+91,90	115 шп - жб			
	Шпалы – эпюра 1840 шп/км					
	ПК2+91,90	Упор ПК7+75,08	889 шп – дер.			
Итого		Шпалы деревянные – 903 шп. железобетонные – 115 шп.				

Таблица 3.6 - Тип рельсов

№ пути	Граница путей		Тип рельсов, длина, м.	Дата внесения изменений	Ф.И.О. должность внесшего изменения	Подпись
	от пикета	до пикета				
22	Знак ГПНП ООО «РОССЫПЬ» ПК2+27,08	ПК2+34,60	P50 2x7,52м	11.2023	Афанасенко С.Н.	
	ПК2+34,60	Упор ПК7+75,08	P65 2x540,48м			
Итого		Рельсы P50 15,04м P65 1080,96м				

Таблица 3.7 - Наличие сварных стыков

№ пути	Граница путей		Наличие сварных стыков	Дата внесения изменений	Ф.И.О. должность внесшего изменения	Подпись
	от пикета	до пикета				
22	Знак ГПНП ООО «РОССЫПЬ» ПК2+27,08	Упор ПК7+75,08	нет	11.2023	Афанасенко С.Н.	

Таблица 3.8 - Ведомость стрелочных переводов

№ Стрелочного перевода	Вид стрелочного перевода, отклонение	Тип и марка стрелочного перевода	Полная длина, м	Дата внесения изменений	Ф.И.О. должность внесшего изменения	Подпись
-				11.2023	Афанасенко С.Н.	

Взам. Инв. №	
Подп. и дата	
Инв. № подл.	2311-ТП

Изм.	Кол.уч.	Лист	№ док.	Подп.	Дата	2311 – ТП		Лист
								5

Таблица 3.9 - Верхнее строение пути на стрелочных переводах

№ стрелочного перевода	Тип рельсов	Подрельсовое основание		Вид балласта	Дата внесения изменений	Ф.И.О. должность внесшего изменения	Подпись
		Шпалы	Брус				
-					11.2023	Афанасенко С.Н.	

Таблица 3.10 - Стыковые крепления

№ пути	Накладки		Количество стыковых болтов	Дата внесения изменений	Ф.И.О. должность внесшего изменения	Подпись
	тип	Кол-во				
22	Двухголовые Р50	8	16	11.2023	Афанасенко С.Н.	
	Двухголовые Р65	86	172			

Таблица 3.11 - Промежуточные крепления

№ пути	Промежуточное скрепление		Дата внесения изменений	Ф.И.О. должность внесшего изменения	Подпись
	Подкладки, шт	Прикрепители, шт			
22	Д50 – 28	Костыли – 112	11.2023	Афанасенко С.Н.	
	Д65 – 1778	Костыли – 7112			
	КБ65 – 230 компл.				

Таблица 3.12 - Закрепление от угона

№ пути	Граница путей		Количество/ тип противоугонов	Дата внесения изменений	Ф.И.О. должность внесшего изменения	Подпись
	от пикета	до пикета				
22	Знак ГПНП ООО «РОССЫПЬ» ПК2+27,08	Упор ПК7+75,08	нет	11.2023	Афанасенко С.Н.	

Инв. № подл.	2311-ТП
Подп. и дата	
Взам. Инв. №	

Изм.	Кол.уч.	Лист	№ док.	Подп.	Дата	2311 – ТП	Лист
							6

4 ТЕХНИЧЕСКОЕ ОСНАЩЕНИЕ ГРУЗОВОГО ФРОНТА

Наличие договора на подачу/уборку вагонов: _____

Наличие лицензии: _____

Наличие таможенных складов временного хранения: _____

Таблица 4.1 - Вместимость грузовых фронтов

№ грузового фронта	Наименование. грузового фронта	Местоположение			Длина, м.	Вместимость, усл. ваг.
		№ пути	от пикета	до пикета		
ГФ1	Платформа (справа)	22	ПК2+78,26	ПК7+26,26	448,00	32 пв. 30пл.

Технико-технологическая характеристика грузовых фронтов:

ГФ1 – платформа (справа):

Среднесуточный вагонооборот (максимальный) – 32 вагона.

Перечень перерабатываемых грузов – *погрузка*: уголь, контейнеры (типа Open Top).

Перечень перерабатываемых опасных грузов – нет.

Средства механизации – фронтальный погрузчик LiuGong 855N, объем ковша 3м³ – 2 шт., автомобильный кран грузоподъемностью 100т.

Железнодорожный путь необщего пользования №22 оборудован вагонными весами марки «ВЕСТА-СД (50/200-50-0,5/0,5)-(1)/141», расположенными: начало весов ПК2+59,19, конец весов ПК2+67,19.

Технический паспорт составлен на основании имеющихся документов и результатов инструментальной съемки и фактического состояния пути.

Данный технический паспорт предназначен только для разработки инструкции «О порядке обслуживания и организации движения на железнодорожном пути необщего пользования ООО «РОССЫПЬ»

Данный технический паспорт не устанавливает права собственности на железнодорожные пути, стрелочные переводы.

Главный инженер
ООО «Забтранспроект»

Афанасенко С.Н.

Взам. Инв. №	
Подп. и дата	
Инв. № подл.	2311-ТП

Изм.	Кол.уч.	Лист	№ док.	Подп.	Дата

2311 – ТП

Лист

7

ПРИЛОЖЕНИЕ

Свидетельства о допуске к работам в области инженерных изысканий, которые оказывают влияние на безопасность объектов капитального строительства

Саморегулируемая организация
основанная на членстве лиц, осуществляющих изыскания
(вид саморегулируемой организации)

АССОЦИАЦИЯ ИНЖЕНЕРОВ-ИЗЫСКАТЕЛЕЙ
«Инженерная подготовка нефтегазовых комплексов»
192012, г. Санкт-Петербург, пер. 3-й Рабфакровский, д. 5,
корп. 4, литер А, оф. 4.11.
www.ingneft.ru
№СРО-И-032-22122011

Санкт - Петербург
(место выдачи Свидетельства)

«07» марта 2017г.
(дата выдачи Свидетельства)

СВИДЕТЕЛЬСТВО
о допуске к определённому виду или видам работ, которые
оказывают влияние на безопасность объектов капитального
строительства
№ 1266

Выдано члену саморегулируемой организации

Общество с ограниченной ответственностью «Забтранспроект»,
ОГРН 1127536004012, ИНН 7536127844,
672039, Забайкальский край, г.Чита, ул.Красноярская, дом 31, пом.47

Основание выдачи Свидетельства: решение Контрольно-дисциплинарного комитета
(наименование органа управления саморегулируемой организации,
АС «Инженерная подготовка нефтегазовых комплексов»
№ 7КДК от 07 марта 2017г.
(номер протокола, дата заседания)

Настоящим Свидетельством подтверждается допуск к работам, указанным в приложении к настоящему Свидетельству, которые оказывают влияние на безопасность объектов капитального строительства.
Начало действия с «07» марта 2017г.
Свидетельство без приложения не действительно.
Свидетельство выдано без ограничения срока и территории его действия.
Свидетельство выдано взамен ранее выданного № 147 от 26 июля 2012г.
(дата выдачи, номер Свидетельства)

Генеральный директор
АС «Инженерная подготовка
нефтегазовых комплексов»
(должность уполномоченного лица)

Артемикин Н.Ф.
(инициалы, фамилия)

(подпись)

(подпись)

Ассоциация
ОГРН 1127536004012
«Инженерная
подготовка
нефтегазовых
комплексов»
ИНН 7536127844
Санкт-Петербург

Инв. № подл.	Взам. Инв. №
2311-ТП	
Подп. и дата	

Изм.	Кол.уч.	Лист	№ док.	Подп.	Дата

ПРИЛОЖЕНИЕ

к Свидетельству о допуске к
определённому виду или видам работ,
которые оказывают влияние на
безопасность объектов капитального
строительства
от «07» марта 2017г.
№ 1266

Виды работ, которые оказывают влияние на безопасность:

1. объектов капитального строительства, включая особо опасные и технически сложные объекты капитального строительства, объекты использования атомной энергии, и о допуске к которым член АС «Инженерная подготовка нефтегазовых комплексов» Общество с ограниченной ответственностью «Забтранспроект», ИНН 7536127844 имеет Свидетельство

№ пп	Наименование вида работ
	НЕТ

2. объектов капитального строительства, включая особо опасные и технически сложные объекты капитального строительства (кроме объектов использования атомной энергии) и о допуске к которым член АС «Инженерная подготовка нефтегазовых комплексов» Общество с ограниченной ответственностью «Забтранспроект», ИНН 7536127844 имеет Свидетельство

№ пп	Наименование вида работ
1.	РАБОТЫ В СОСТАВЕ ИНЖЕНЕРНО-ГЕОДЕЗИЧЕСКИХ ИЗЫСКАНИЙ
1.1.	Создание опорных геодезических сетей.
1.2.	Геодезические наблюдения за деформациями и осадками зданий и сооружений, движениями земной поверхности и опасными природными процессами.
1.3.	Создание и обновление инженерно-топографических планов в масштабах 1:200 – 1:5000, в том числе в цифровой форме, съемка подземных коммуникаций и сооружений.
1.4.	Трассирование линейных объектов.
1.5.	Инженерно-гидрографические работы.
1.6.	Специальные геодезические и топографические работы при строительстве и реконструкции зданий и сооружений.
2.	РАБОТЫ В СОСТАВЕ ИНЖЕНЕРНО-ГЕОЛОГИЧЕСКИХ ИЗЫСКАНИЙ
2.1.	Инженерно-геологическая съемка в масштабах 1:500 – 1:25000.
2.2.	Проходка горных выработок с их опробованием, лабораторные исследования физико-механических свойств грунтов и химических свойств проб подземных вод.
2.3.	Изучение опасных геологических и инженерно-геологических процессов с разработкой рекомендаций по инженерной защите территории.
2.4.	Гидрогеологические исследования.
2.5.	Инженерно-геофизические исследования.
2.6.	Инженерно-геокриологические исследования.
2.7.	Сейсмологические и сейсмотектонические исследования территории, сейсмическое микрорайонирование.
3.	РАБОТЫ В СОСТАВЕ ИНЖЕНЕРНО-ГИДРОМЕТЕОРОЛОГИЧЕСКИХ ИЗЫСКАНИЙ
3.1.	Метеорологические наблюдения и изучение гидрологического режима водных объектов.
3.2.	Изучение опасных гидрометеорологических процессов и явлений с расчетами их

Инв. № подл.	Подп. и дата	Взам. Инв. №
2311-ТП		

Изм.	Кол.уч.	Лист	№ док.	Подп.	Дата

	характеристик.
3.3.	Изучение русловых процессов водных объектов, деформаций и переработки берегов.
3.4.	Исследования ледового режима водных объектов.
4.	РАБОТЫ В СОСТАВЕ ИНЖЕНЕРНО-ЭКОЛОГИЧЕСКИХ ИЗЫСКАНИЙ
4.1.	Инженерно-экологическая съемка территории.
4.2.	Исследования химического загрязнения почвогрунтов, поверхностных и подземных вод, атмосферного воздуха, источников загрязнения.
4.3.	Лабораторные химико-аналитические и газохимические исследования образцов и проб почвогрунтов и воды.
4.4.	Исследования и оценка физических воздействий и радиационной обстановки на территории.
4.5.	Изучение растительности, животного мира, санитарно-эпидемиологические и медико-биологические исследования территории*
5.	РАБОТЫ В СОСТАВЕ ИНЖЕНЕРНО-ГЕОТЕХНИЧЕСКИХ ИЗЫСКАНИЙ (ВЫПОЛНЯЮТСЯ В СОСТАВЕ ИНЖЕНЕРНО-ГЕОЛОГИЧЕСКИХ ИЗЫСКАНИЙ ИЛИ ОТДЕЛЬНО НА ИЗУЧЕННОЙ В ИНЖЕНЕРНО-ГЕОЛОГИЧЕСКОМ ОТНОШЕНИИ ТЕРРИТОРИИ ПОД ОТДЕЛЬНЫЕ ЗДАНИЯ И СООРУЖЕНИЯ)
5.1.	Проходка горных выработок с их опробованием и лабораторные исследования механических свойств грунтов с определением характеристик для конкретных схем расчета оснований фундаментов.
5.2.	Полевые испытания грунтов с определением их стандартных прочностных и деформационных характеристик (штамповые, сдвиговые, прессиометрические, срезные). Испытания эталонных и натурных свай.
5.3.	Определение стандартных механических характеристик грунтов методами статического, динамического и бурового зондирования.
5.4.	Физическое и математическое моделирование взаимодействия зданий и сооружений с геологической средой.
5.5.	Специальные исследования характеристик грунтов по отдельным программам для нестандартных, в том числе нелинейных методов расчета оснований фундаментов и конструкций зданий и сооружений.
5.6.	Геотехнический контроль строительства зданий, сооружений и прилегающих территорий.
6.	Обследование состояния грунтов основания зданий и сооружений.

3. объектов капитального строительства (кроме особо опасных и технически сложных объектов, объектов использования атомной энергии) и о допуске к которым член АС «Инженерная подготовка нефтегазовых комплексов» Общество с ограниченной ответственностью «Забтранспроект», ИНН 7536127844 имеет Свидетельство

№ пп	Наименование вида работ
	НЕТ

Общество с ограниченной ответственностью «Забтранспроект» вправе заключать договоры по осуществлению организации работ в области инженерных изысканий, которые оказывают влияние на безопасность объектов капитального строительства.

Генеральный директор
АС «Инженерная подготовка
нефтегазовых комплексов»
должность



Артекин Н.Ф.
фамилия, инициалы

Взам. Инв. №	
Подп. и дата	
Инв. № подл.	2311-ТП


Изм.	Кол.уч.	Лист	№ док.	Подп.	Дата

Ведомость ж.д. путей

N пути	Наименование пути	Длина пути		Граница пути	
		полная	полезная	от	до
22	Погрузо-выгрузочный	548,00	501,10	Знак ПНП ООО "РОССЫПЬ" ПК2+27,08	Упор ПК7+75,08



Ведомость габаритов

Номер	Тип сооружения	Путь	Пикет	Габарит лево/право
1	Въездные ворота	22	ПК2+27,08	2,52/2,66
2	Габаритные ворота	22	ПК2+40,10	2,49/2,47
3	Смотровая эстакада	22	ПК2+50,86 ПК2+52,29	-/2,77 -/2,93
4	Платформа	22	ПК2+78,26 ПК7+26,26	-/1,81 -/2,05

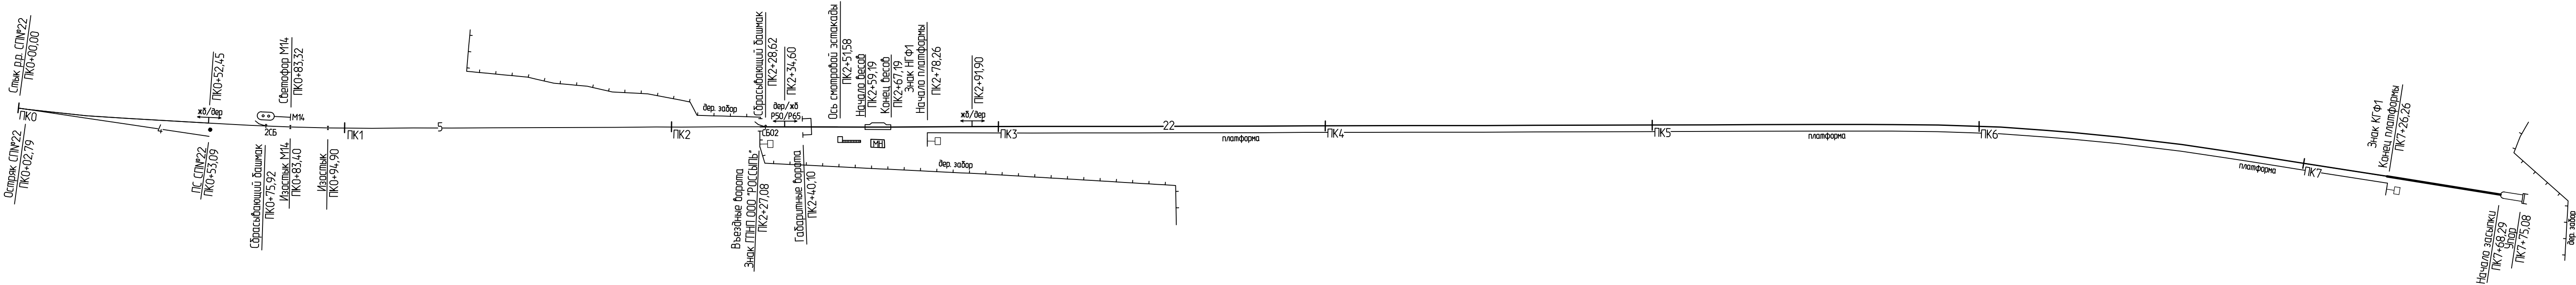


Примечание:

1. Инструментальная съемка железнодорожного пути необщего пользования N22 ООО "РОССЫПЬ" выполнена сотрудниками ООО Забтранспроект" в ноябре 2023 года с использованием электронного тахеометра Leica TCR405.
2. Пикетаж разбит по оси пути N5 от стыка рамного рельса стрелочного перевода N22 ПК0+00,00.

  						2311-ТП-ГЧ			
Изм.	Кол.	Лист	Ндэк.	Подпись	Дата	Пути необщего пользования №22 ООО "РОССЫПЬ"			
Рук.работ		Афанасенко С.Н.			11.23	Станция Бада	Стадия	Лист	Листов
Инженер		Егизарян Н.А.			11.23			1	2
						План пути №22	ООО "Забтранспроект" 2023г.		
Н.контр.		Афанасенко С.Н.			11.23				

Нестандартный пикет
Ситуация
Тип рельса
Тип шпал
Разница отметок фактических и спрямленных уклонов, см
Отметки головки рельсов по спрямленным уклонам, м
Длина, м
Спрямоленные уклоны, %
Фактические уклоны, %
Фактические отметки головки рельсов, м
Отметки земляного полотна, м
Расстояния, м
Пикеты
План 22 пути
Километры

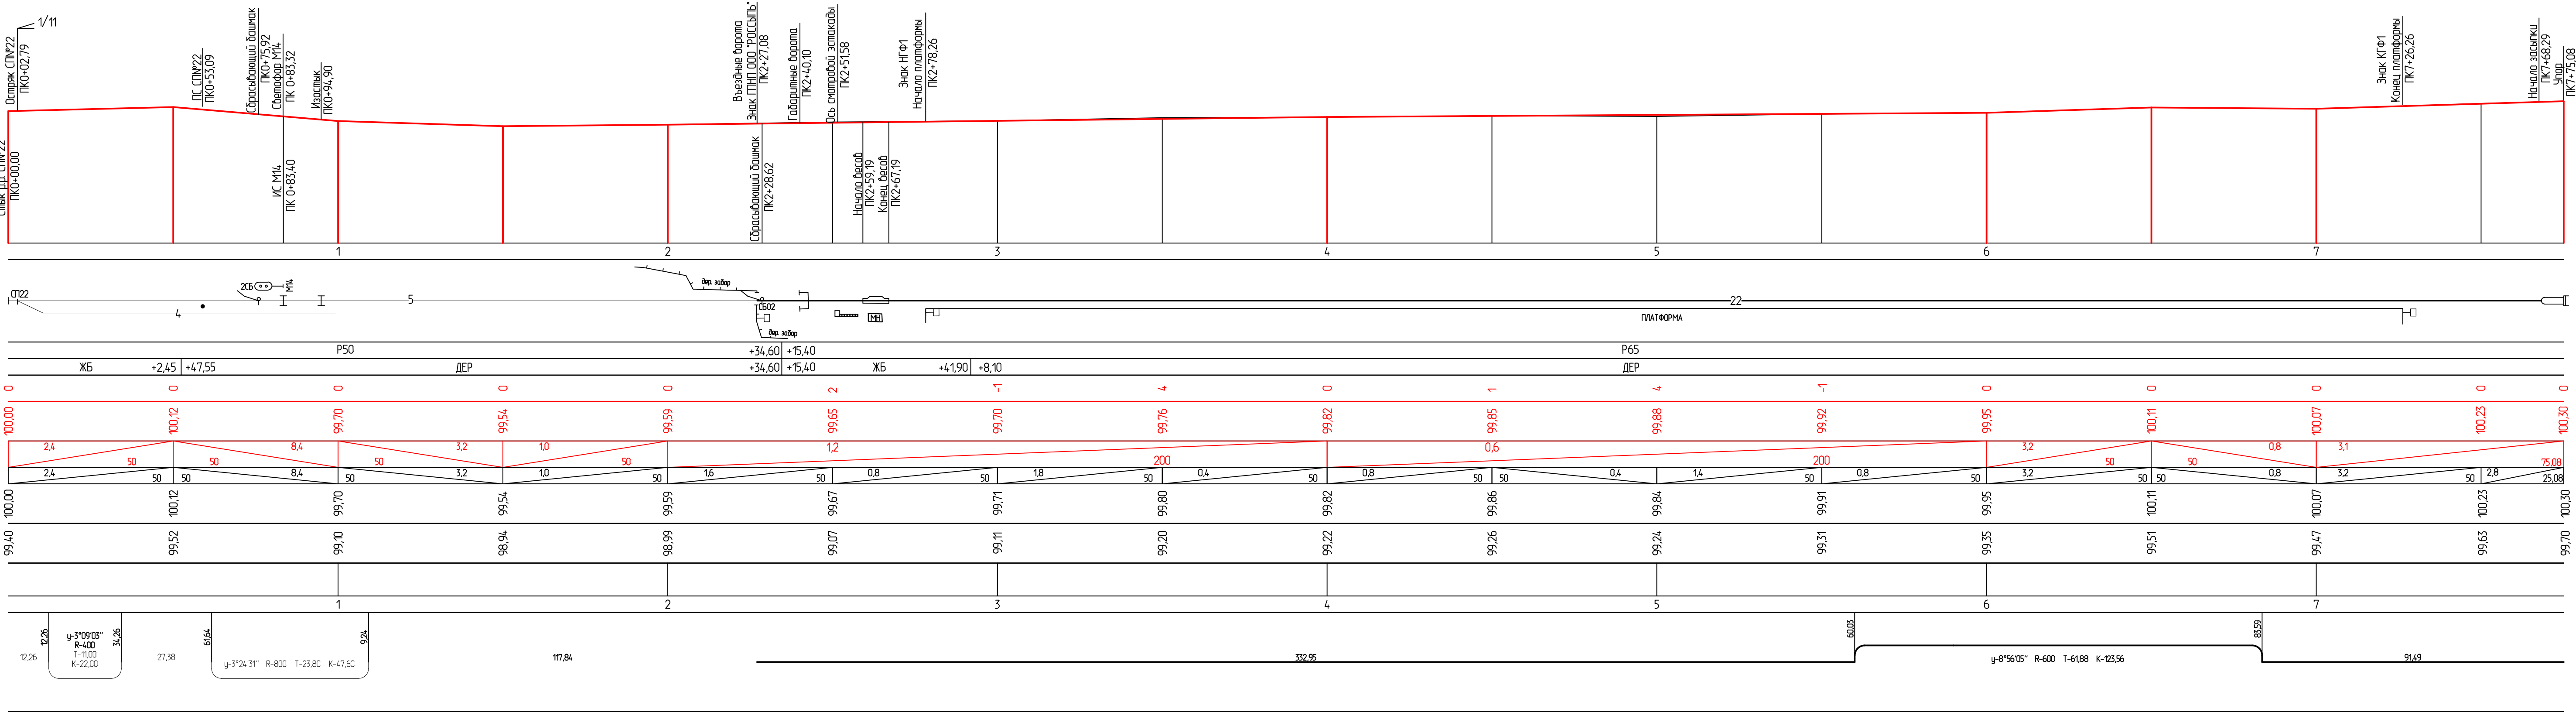

- Примечания:
- Инструментальная съемка железнодорожного пути необщего пользования N22 ООО "РОССЫЛЬ" выполнена сотрудниками ООО Забтранспроект в ноябре 2023 года с использованием электронного тахеометра Leica TOR405.
 - Пикетаж разбит по оси пути N5 от стыка рамного рельса стрелочного перевода N22 ПК0+00,00.
 - Система высот условная.

Изм.	Кол.	Лист	Изд.	Подпись	Дата	2311-ТП-ГЧ			
Рук.работ	Афанасенко С.Н.	1123				Пути необщего пользования N22 ООО "РОССЫЛЬ"			
Инженер	Евгизарян Н.А.	1123				Станция Бада	Лист	Листов	
							2	2	
Н.контр.	Афанасенко С.Н.	1123				Продольный профиль пути №22			
							ООО "Забтранспроект" 2023г.		