



ОБЩЕСТВО С ОГРАНИЧЕННОЙ ОТВЕТСТВЕННОСТЬЮ
«ЗАБТРАНСПРОЕКТ»

Свидетельство № 1266 от 7 марта 2026 г.

СРО-И-032-111011

ТЕХНИЧЕСКИЙ ПАСПОРТ

железнодорожного пути
необщего пользования
ИП Цивинский Н.Н.

Пути №1, 2

ст. Чита-1

Главный инженер
ООО «Забтранспроект»

Афанасенко С.Н.

Ведущий инженер

Егiazарян Н.А.

Чита, 2023

Взам. Инв. №	
Подп. и дата	
Инв. № подл.	2307-ТП

ОБЩИЕ СВЕДЕНИЯ

Место примыкания железнодорожного пути необщего пользования:

железнодорожный путь необщего пользования №1 ИП Цивинский Н.Н. находится на продолжении железнодорожного пути необщего пользования ИП Талибов Западного парка ст. Чита-1 Забайкальской железной дороги.

Границы железнодорожного пути необщего пользования:

границей железнодорожных путей необщего пользования ИП Цивинский Н.Н. является знак «Граница пути необщего пользования» ПК0+00,00, установленный на расстоянии 415,93м от остряка стрелочного перевода №354.

Наличие предохранительных устройств:

нет

Дата заключения договора на эксплуатацию железнодорожного пути необщего пользования и срок его действия:

Порядок подачи и уборки вагонов (кем производится – железной дорогой, средствами предприятия или маневровым порядком), серия локомотива, применяемого при подаче и уборке вагонов:

подача и уборка вагонов на пути необщего пользования №1, 2 ИП Цивинский Н.Н. осуществляется маневровым порядком локомотивами серии ТЭМ2, ТЭМ2А, ТЭМ18Д, ТЭМ18ДМ ст. Чита-1 Забайкальской железной дороги.

Взам. Инв. №	
Подп. и дата	
Инв. №подл.	2307-ТП

							2307– ТП			
Изм.	Коп.уч.	Лист	№ док.	Подп.	Дата					
Разработал		Егизарян				Технический паспорт железнодорожного пути необщего пользования №1 ИП Цивинский Н.Н.		Стадия	Лист	Листов
Проверил		Афанасенко							1	12
						ООО «Забтранспроект»				

1 ХАРАКТЕРИСТИКА ПУТИ

Таблица 1.1 – Примыкания других железнодорожных путей к железнодорожным путям предприятия

Наименование предприятия	Место примыкания (пикет, стрелка)	Длина Путь км.	Предприятие обслуживающее путь необщего пользования
ИП Талибов	ПК0+00,00 (Знак ГПНП ИП Цивинский Н.Н.)	0,220	ИП Талибов

Таблица 1.2 - Ведомость железнодорожных путей предприятия

№ пути	Граница путей		Специализация	Дата внесения изменений	Ф.И.О. должность внесшего изменения	Подпись
	от	до				
1	Знак ГПНП ИП Цивинский Н.Н ПК0+00,00	Конец пути ПК2+71,70	Погрузочно-выгрузочный	08.2023	Афанасенко С.Н.	
2	Остряк СП№1 ПК0+24,16	Конец пути ПК1+50,76	Погрузочно-выгрузочный			

Таблица 1.3 – Данные по длине путей

№ пути	Граница путей		Длины путей, м		Дата внесения изменений	Ф.И.О. должность внесшего изменения	Подпись
	от	до	полная	полезная			
1	Знак ГПНП ИП Цивинский Н.Н ПК0+00,00	Конец пути ПК2+71,70	271,70	174,77	08.2023	Афанасенко С.Н.	
2	Остряк СП№1 ПК0+24,16	Конец пути ПК1+50,76	126,60	59,83			
ИТОГО			398,30	234,60			

Изм.	Кол.уч.	Лист	№ док.	Подп.	Дата
Инд. № подл.	2307-ТП				
Взам. Инв. №					
Подп. и дата					

2307 – ТП

Лист

2

2 НИЖНЕЕ СТРОЕНИЕ ПУТИ И ИСКУССТВЕННЫЕ СООРУЖЕНИЯ

Таблица 2.1 – Наличие насыпей или выемок

№ пути	Граница путей		Наличие насыпей право/лево	Дата внесения изменений	Ф.И.О. должность внесшего изменения	Подпись
	от пикета	до пикета				
1	Знак ГПНП ИП Цивинский Н.Н ПК0+00,00	Конец пути ПК2+71,70	нет	08.2023	Афанасенко С.Н.	
2	Остряк СП№1 ПК0+24,16	Конец пути ПК1+50,76	нет			

Таблица 2.2 – Наличие водоотводных сооружений

№ пути	Граница путей		Водоотводное устройство право/лево	Дата внесения изменений	Ф.И.О. должность внесшего изменения	Подпись
	от пикета	до пикета				
1	Знак ГПНП ИП Цивинский Н.Н ПК0+00,00	Конец пути ПК2+71,70	нет	08.2023	Афанасенко С.Н.	
2	Остряк СП№1 ПК0+24,16	Конец пути ПК1+50,76	нет			

Таблица 2.3 – Деформация земляного полотна

№ пути	Граница путей		Тип деформации право/лево	Дата внесения изменений	Ф.И.О. должность внесшего изменения	Подпись
	от пикета	до пикета				
1	Знак ГПНП ИП Цивинский Н.Н ПК0+00,00	Конец пути ПК2+71,70	нет	08.2023	Афанасенко С.Н.	
2	Остряк СП№1 ПК0+24,16	Конец пути ПК1+50,76	нет			

Таблица 2.4 – Искусственные сооружения

№ пути	Граница путей		Вид искусственного сооружения	Дата внесения изменений	Ф.И.О. должность внесшего изменения	Подпись
	от пикета	до пикета				
1	Знак ГПНП ИП Цивинский Н.Н ПК0+00,00	Конец пути ПК2+71,70	нет	08.2023	Афанасенко С.Н.	
2	Остряк СП№1 ПК0+24,16	Конец пути ПК1+50,76	нет			

Взам. Инв. №	
Подп. и дата	
Инв. № подл.	2307-ТП

Изм.	Кол.уч.	Лист	№ док.	Подп.	Дата	2307 – ТП	Лист
							3

Таблица 2.5 – Пересечения с автомобильными дорогами

№ пути	от пикета	до пикета	Вид пересечения	Дата внесения изменений	Ф.И.О. должность внесшего изменения	Подпись
1	Знак ГПНП ИП Цивинский Н.Н ПК0+00,00	Конец пути ПК2+71,70	Технологический проезд (шир.12м) ПК0+90,87	08.2023	Афанасенко С.Н.	
			Технологический проезд (шир.6м) ПК2+47,50			
2	Остряк СП№1 ПК0+24,16	Конец пути ПК1+50,76	Технологический проезд (шир.12м) ПК0+91,28			

Взам. Инв. №	
Подп. и дата	
Инв. № подл.	2307-ТП

Изм.	Кол.уч.	Лист	№ док.	Подп.	Дата

2307 – ТП

Лист

4

3 ВЕРХНЕЕ СТРОЕНИЕ ПУТИ

Таблица 3.1 – Род балласта в балластном слое

№ пути	Граница путей		Род балласта	Дата внесения изменений	Ф.И.О. должность внесшего изменения	Подпись
	от пикета	до пикета				
1	Знак ГПНП ИП Цивинский Н.Н ПК0+00,00	Конец пути ПК2+71,70	Щебень	08.2023	Афанасенко С.Н.	
2	Остряк СП№1 ПК0+24,16	Конец пути ПК1+50,76	Щебень			

Таблица 3.2 – Толщина балластного слоя

№ пути	Граница путей		Толщина	Дата внесения изменений	Ф.И.О. должность внесшего изменения	Подпись
	от пикета	до пикета				
1	Знак ГПНП ИП Цивинский Н.Н ПК0+00,00	Конец пути ПК2+71,70	до 25 см	08.2023	Афанасенко С.Н.	
2	Остряк СП№1 ПК0+24,16	Конец пути ПК1+50,76	до 25 см			

Таблица 3.3 – Загрязнение балластного слоя

№ пути	Граница путей		Загрязнение	Дата внесения изменений	Ф.И.О. должность внесшего изменения	Подпись
	от пикета	до пикета				
1	Знак ГПНП ИП Цивинский Н.Н ПК0+00,00	Конец пути ПК2+71,70	до 10 %	08.2023	Афанасенко С.Н.	
2	Остряк СП№1 ПК0+24,16	Конец пути ПК1+50,76	до 10 %			

Таблица 3.4 – Загрязняемость балластного слоя

№ пути	Граница путей		Загрязняемость	Дата внесения изменений	Ф.И.О. должность внесшего изменения	Подпись
	от пикета	до пикета				
1	Знак ГПНП ИП Цивинский Н.Н ПК0+00,00	Конец пути ПК2+71,70	нет	08.2023	Афанасенко С.Н.	
2	Остряк СП№1 ПК0+24,16	Конец пути ПК1+50,76	нет			

Взам. Инв. №

Подп. и дата

Инв. № подл.

2307-ТП

2307 – ТП

Лист

5

Изм. Кол.уч. Лист № док. Подп. Дата

Таблица 3.5 – Эпюра шпал, количество шпал в пути, материал шпал

№ пути	Граница путей		Эпюра, количество материал	Дата внесения изменений	Ф.И.О. должность внесшего изменения	Подпись
	от пикета	до пикета				
Шпалы – эпюра 1440 шп/км						
1	Знак ГПНП ИП Цивинский Н.Н ПК0+00,00	Конец пути ПК2+71,70	343 шп – дер.	08.2023	Афанасенко С.Н.	
2	Остряк СП№1 ПК0+24,16	Конец пути ПК1+50,76	138 шп - дер			
Итого		Шпалы деревянные – 481 шп				

Таблица 3.6 – Тип рельсов

№ пути	Граница путей		Тип рельсов, длина, м.	Дата внесения изменений	Ф.И.О. должность внесшего изменения	Подпись
	от пикета	до пикета				
1	Знак ГПНП ИП Цивинский Н.Н ПК0+00,00	Конец пути ПК2+71,70	P65 – 238,30м x2	08.2023	Афанасенко С.Н.	
2	Остряк СП№1 ПК0+24,16	Конец пути ПК1+50,76	P65 – 95,97м x 2			
Итого		Рельсы P65 – 668,54 м				

Таблица 3.7 – Наличие сварных стыков

№ пути	Граница путей		Наличие сварных стыков	Дата внесения изменений	Ф.И.О. должность внесшего изменения	Подпись
	от пикета	до пикета				
1	Знак ГПНП ИП Цивинский Н.Н ПК0+00,00	Конец пути ПК2+71,70	нет	08.2023	Афанасенко С.Н.	
2	Остряк СП№1 ПК0+24,16	Конец пути ПК1+50,76	нет			

Таблица 3.8 – Ведомость стрелочных переводов

№ Стрелочного перевода	Вид стрелочного перевода, отклонение	Тип и марка стрелочного перевода	Полная длина, м	Дата внесения изменений	Ф.И.О. должность внесшего изменения	Подпись
1	Обыкновенный, нецентрализованый, левый	1/11 P65	33,40	08.2023	Афанасенко С.Н.	

Таблица 3.9 – Верхнее строение пути на стрелочных переводах

№ стрелочного перевода	Тип рельсов	Подрельсовое основание		Вид балласта	Дата внесения изменений	Ф.И.О. должность внесшего изменения	Подпись
		Шпалы	Брус				
1	P65	5	55	Щебень	08.2023	Афанасенко С.Н.	

Взам. Инв. №

Подп. и дата

Инв. № подл.

2307-ТП

2307 – ТП

Лист

6

Изм. Кол.уч. Лист № док. Подп. Дата

Таблица 3.10 – Стыковые крепления

№ пути	Накладки		Количество стыковых болтов	Дата внесения изменений	Ф.И.О. должность внесшего изменения	Подпись
	тип	Кол-во				
1	Двухголовые Р65	72	144	08.2023	Афанасенко С.Н.	
2	Двухголовые Р65	28	56			

Таблица 3.11 – Промежуточные крепления

№ пути	Промежуточное крепление		Дата внесения изменений	Ф.И.О. должность внесшего изменения	Подпись
	Подкладки, шт	Прикрепители, шт			
1	Д65 – 686	Костыли – 2744	08.2023	Афанасенко С.Н.	
2	Д65 – 276	Костыли – 1104			

Таблица 3.12 – Закрепление от угона

№ пути	Граница путей		Количество/ тип противоугонов	Дата внесения изменений	Ф.И.О. должность внесшего изменения	Подпись
	от пикета	до пикета				
1	Знак ГПНП ИП Цивинский Н.Н ПК0+00,00	Конец пути ПК2+71,70	нет	08.2023	Афанасенко С.Н.	
2	Остряк СП№1 ПК0+24,16	Конец пути ПК1+50,76				

Инв. № подл.	2307-ТП
Подп. и дата	
Взам. Инв. №	

Изм.	Кол.уч.	Лист	№ док.	Подп.	Дата

2307 – ТП

Лист

7

4 ТЕХНИЧЕСКОЕ ОСНАЩЕНИЕ ГРУЗОВОГО ФРОНТА

Наличие договора на подачу/уборку вагонов: _____

Наличие лицензии: _____

Наличие таможенных складов временного хранения: _____

Таблица 4.1 – Вместимость грузовых фронтов

№ грузового фронта	Наименование грузового фронта	Местоположение			Длина, м.	Вместимость, физ. ваг.
		№ пути	от пикета	до пикета		
ГФ1	Рампа (слева)	1	ПК1+01,26	ПК1+57,00	55,74	3 (пл., пв., кр.)
ГФ2	Рампа (справа)	2	ПК1+02,68	ПК1+50,76	48,08	3 (пл., пв., кр.)
ГФ3	Открытая площадка (справа)	1	ПК1+60,50	ПК2+42,50	82,00	5 (пл., пв., кр.)
ГФ4	Эстакада	1	ПК2+56,70	ПК2+71,70	15,00	1 пл.

Технико-технологическая характеристика грузовых фронтов:

ГФ1 – рампа (слева):

Среднесуточный вагонооборот (максимальный) – 3 вагона.

Перечень перерабатываемых грузов – **выгрузка:** тарно-штучные грузы, автотракторная техника, цемент в мешках 50кг, строительные материалы, разделка вагонов.

Перечень перерабатываемых опасных грузов – нет.

Средства механизации: фронтальный погрузчик, грузоподъемностью 4т, вилочный погрузчик, грузоподъемностью 5т, автомобильный кран, грузоподъемностью 25т.

ГФ2 – рампа (справа):

Среднесуточный вагонооборот (максимальный) – 3 вагона.

Перечень перерабатываемых грузов – **погрузка:** стеклобой навалом, металлолом, строительные материалы; **выгрузка:** тарно-штучные грузы, автотракторная техника, цемент в мешках 50кг, строительные материалы, сборный груз.

Перечень перерабатываемых опасных грузов – нет.

Средства механизации: фронтальный погрузчик, грузоподъемностью 4т, вилочный погрузчик, грузоподъемностью 5т, автомобильный кран, грузоподъемностью 25т.

ГФ3 – открытая площадка (справа):

Среднесуточный вагонооборот (максимальный) – 5 вагонов.

Перечень перерабатываемых грузов – **погрузка/выгрузка:** металлопрокат, пиломатериалы, кирпич, цемент в мешках 1000кг, ЖБИ.

Перечень перерабатываемых опасных грузов – нет.

Средства механизации: козловой кран ККС-16/30, грузоподъемность 16т, вилочный погрузчик, грузоподъемностью 5т

ГФ4 – эстакада:

Среднесуточный вагонооборот (максимальный) – 1 вагон.

Перечень перерабатываемых грузов – **выгрузка:** легковые автомобили

Перечень перерабатываемых опасных грузов – нет.

Средства механизации: нет.

Взам. №	
Подп. и дата	
Инв. № подл.	2307-ТП

Изм.	Кол.уч.	Лист	№ док.	Подп.	Дата

2307 – ТП

Лист

8

Технический паспорт составлен на основании имеющихся документов и результатов инструментальной съемки и фактического состояния пути.

Данный технический паспорт предназначен только для разработки инструкции «О порядке обслуживания и организации движения на железнодорожном пути необщего пользования ИП Цивинский Н.Н.

Данный технический паспорт не устанавливает права собственности на железнодорожные пути, стрелочные переводы.

Главный инженер
ООО «Забтранспроект»

Афанасенко С.Н.

Инв. № подл.	2307-ТП	Подп. и дата	Взам. Инв. №						
Изм.	Кол.уч.	Лист	№ док.	Подп.	Дата	2307 – ТП			Лист
									9

ПРИЛОЖЕНИЕ

Свидетельства о допуске к работам в области инженерных изысканий, которые оказывают влияние на безопасность объектов капитального строительства

Саморегулируемая организация
основанная на членстве лиц, осуществляющих изыскания
(вид саморегулируемой организации)

АССОЦИАЦИЯ ИНЖЕНЕРОВ-ИЗЫСКАТЕЛЕЙ
«Инженерная подготовка нефтегазовых комплексов»
192012, г. Санкт-Петербург, пер. 3-й Рабфакровский, д. 5,
корп. 4, литер А, оф. 4.11.
www.ingneft.ru
№СРО-И-032-22122011

Санкт - Петербург
(место выдачи Свидетельства)

«07» марта 2017г.
(дата выдачи Свидетельства)

СВИДЕТЕЛЬСТВО
о допуске к определённому виду или видам работ, которые
оказывают влияние на безопасность объектов капитального
строительства
№ 1266

Выдано члену саморегулируемой организации

Общество с ограниченной ответственностью «Забтранспроект»,
ОГРН 1127536004012, ИНН 7536127844,
672039, Забайкальский край, г.Чита, ул.Красноярская, дом 31, пом.47

Основание выдачи Свидетельства: решение Контрольно-дисциплинарного комитета
(наименование органа управления саморегулируемой организации,
АС «Инженерная подготовка нефтегазовых комплексов»
№ 7КДК от 07 марта 2017г.
(номер протокола, дата заседания)

Настоящим Свидетельством подтверждается допуск к работам, указанным в приложении к настоящему Свидетельству, которые оказывают влияние на безопасность объектов капитального строительства.
Начало действия с «07» марта 2017г.
Свидетельство без приложения не действительно.
Свидетельство выдано без ограничения срока и территории его действия.
Свидетельство выдано взамен ранее выданного № 147 от 26 июля 2012г.
(дата выдачи, номер Свидетельства)

Генеральный директор
АС «Инженерная подготовка
нефтегазовых комплексов»
(должность уполномоченного лица)

Артемикин Н.Ф.
(инициалы, фамилия)

(подпись)

(подпись)

Ассоциация
ОГРН 1027500032045
«Инженерная
подготовка
нефтегазовых
комплексов»
ИНН 7511154090
Санкт-Петербург

Инв. № подл.	2307-ТП
Подп. и дата	
Взам. Инв. №	

Изм.	Кол.уч.	Лист	№ док.	Подп.	Дата

2307 – ТП

Лист

10

ПРИЛОЖЕНИЕ

к Свидетельству о допуске к
определённому виду или видам работ,
которые оказывают влияние на
безопасность объектов капитального
строительства
от «07» марта 2017г.
№ 1266

Виды работ, которые оказывают влияние на безопасность:

1. объектов капитального строительства, включая особо опасные и технически сложные объекты капитального строительства, объекты использования атомной энергии, и о допуске к которым член АС «Инженерная подготовка нефтегазовых комплексов» Общество с ограниченной ответственностью «Забтранспроект», ИНН 7536127844 имеет Свидетельство

№ пп	Наименование вида работ
	НЕТ

2. объектов капитального строительства, включая особо опасные и технически сложные объекты капитального строительства (кроме объектов использования атомной энергии) и о допуске к которым член АС «Инженерная подготовка нефтегазовых комплексов» Общество с ограниченной ответственностью «Забтранспроект», ИНН 7536127844 имеет Свидетельство

№ пп	Наименование вида работ
1.	РАБОТЫ В СОСТАВЕ ИНЖЕНЕРНО-ГЕОДЕЗИЧЕСКИХ ИЗЫСКАНИЙ
1.1.	Создание опорных геодезических сетей.
1.2.	Геодезические наблюдения за деформациями и осадками зданий и сооружений, движениями земной поверхности и опасными природными процессами.
1.3.	Создание и обновление инженерно-топографических планов в масштабах 1:200 – 1:5000, в том числе в цифровой форме, съемка подземных коммуникаций и сооружений.
1.4.	Трассирование линейных объектов.
1.5.	Инженерно-гидрографические работы.
1.6.	Специальные геодезические и топографические работы при строительстве и реконструкции зданий и сооружений.
2.	РАБОТЫ В СОСТАВЕ ИНЖЕНЕРНО-ГЕОЛОГИЧЕСКИХ ИЗЫСКАНИЙ
2.1.	Инженерно-геологическая съемка в масштабах 1:500 – 1:25000.
2.2.	Проходка горных выработок с их опробованием, лабораторные исследования физико-механических свойств грунтов и химических свойств проб подземных вод.
2.3.	Изучение опасных геологических и инженерно-геологических процессов с разработкой рекомендаций по инженерной защите территории.
2.4.	Гидрогеологические исследования.
2.5.	Инженерно-геофизические исследования.
2.6.	Инженерно-геокриологические исследования.
2.7.	Сейсмологические и сейсмотектонические исследования территории, сейсмическое микрорайонирование.
3.	РАБОТЫ В СОСТАВЕ ИНЖЕНЕРНО-ГИДРОМЕТЕОРОЛОГИЧЕСКИХ ИЗЫСКАНИЙ
3.1.	Метеорологические наблюдения и изучение гидрологического режима водных объектов.
3.2.	Изучение опасных гидрометеорологических процессов и явлений с расчетами их

Инв. № подл.	Подп. и дата	Взам. Инв. №
2307-ТП		

Изм.	Кол.уч.	Лист	№ док.	Подп.	Дата

	характеристик.
3.3.	Изучение русловых процессов водных объектов, деформаций и переработки берегов.
3.4.	Исследования ледового режима водных объектов.
4.	РАБОТЫ В СОСТАВЕ ИНЖЕНЕРНО-ЭКОЛОГИЧЕСКИХ ИЗЫСКАНИЙ
4.1.	Инженерно-экологическая съемка территории.
4.2.	Исследования химического загрязнения почвогрунтов, поверхностных и подземных вод, атмосферного воздуха, источников загрязнения.
4.3.	Лабораторные химико-аналитические и газохимические исследования образцов и проб почвогрунтов и воды.
4.4.	Исследования и оценка физических воздействий и радиационной обстановки на территории.
4.5.	Изучение растительности, животного мира, санитарно-эпидемиологические и медико-биологические исследования территории*
5.	РАБОТЫ В СОСТАВЕ ИНЖЕНЕРНО-ГЕОТЕХНИЧЕСКИХ ИЗЫСКАНИЙ (ВЫПОЛНЯЮТСЯ В СОСТАВЕ ИНЖЕНЕРНО-ГЕОЛОГИЧЕСКИХ ИЗЫСКАНИЙ ИЛИ ОТДЕЛЬНО НА ИЗУЧЕННОЙ В ИНЖЕНЕРНО-ГЕОЛОГИЧЕСКОМ ОТНОШЕНИИ ТЕРРИТОРИИ ПОД ОТДЕЛЬНЫЕ ЗДАНИЯ И СООРУЖЕНИЯ)
5.1.	Проходка горных выработок с их опробованием и лабораторные исследования механических свойств грунтов с определением характеристик для конкретных схем расчета оснований фундаментов.
5.2.	Полевые испытания грунтов с определением их стандартных прочностных и деформационных характеристик (штамповые, сдвиговые, прессиометрические, срезные). Испытания эталонных и натуральных свай.
5.3.	Определение стандартных механических характеристик грунтов методами статического, динамического и бурового зондирования.
5.4.	Физическое и математическое моделирование взаимодействия зданий и сооружений с геологической средой.
5.5.	Специальные исследования характеристик грунтов по отдельным программам для нестандартных, в том числе нелинейных методов расчета оснований фундаментов и конструкций зданий и сооружений.
5.6.	Геотехнический контроль строительства зданий, сооружений и прилегающих территорий.
6.	Обследование состояния грунтов основания зданий и сооружений.

3. объектов капитального строительства (кроме особо опасных и технически сложных объектов, объектов использования атомной энергии) и о допуске к которым член АС «Инженерная подготовка нефтегазовых комплексов» Общество с ограниченной ответственностью «Забтранспроект», ИНН 7536127844 имеет Свидетельство

№ пп	Наименование вида работ
	НЕТ

Общество с ограниченной ответственностью «Забтранспроект» вправе заключать договоры по осуществлению организации работ в области инженерных изысканий, которые оказывают влияние на безопасность объектов капитального строительства.

Генеральный директор
АС «Инженерная подготовка
нефтегазовых комплексов»
должность



Артемкин Н.Ф.
фамилия, инициалы

Взам. Инв. №	
Подп. и дата	
Инв. № подл.	2307-ТП

Изм.	Кол.уч.	Лист	№ док.	Подп.	Дата

Ведомость ж.д. путей


N пути	Наименование пути	Длина пути		Граница пути	
		полная	полезная	от	до
1	Погрузочно-выгрузочный	271,70	174,77	Знак ГПНП ПК0+00,00	Конец пути ПК2+71,70
2	Погрузочно-выгрузочный	126,60	59,83	Остряк СПН1 ПК0+24,16	Конец пути ПК1+50,76

Ведомость стрелочных переводов

N стр. перевода	Вид стрелочного перевода, отклонения	Марка крестовины	Полная длина, м
СП N1	Обыкновенный, нецентрализованный левый	1/11 Р65	33,40

Ведомость габаритов

Номер	Тип сооружения	Пикет	Габарит лево/право
1	Ворота	ПК0+12,67	2,50/2,61
1	Рампа	ПК1+01,26 ПК1+57,00	2,05/- 2,04/-
1	Подпорная стенка	ПК1+58,46 ПК2+34,64	- /3,60 - /2,35
2	Рампа	ПК1+02,68 ПК1+50,76	- /2,00 - /2,02

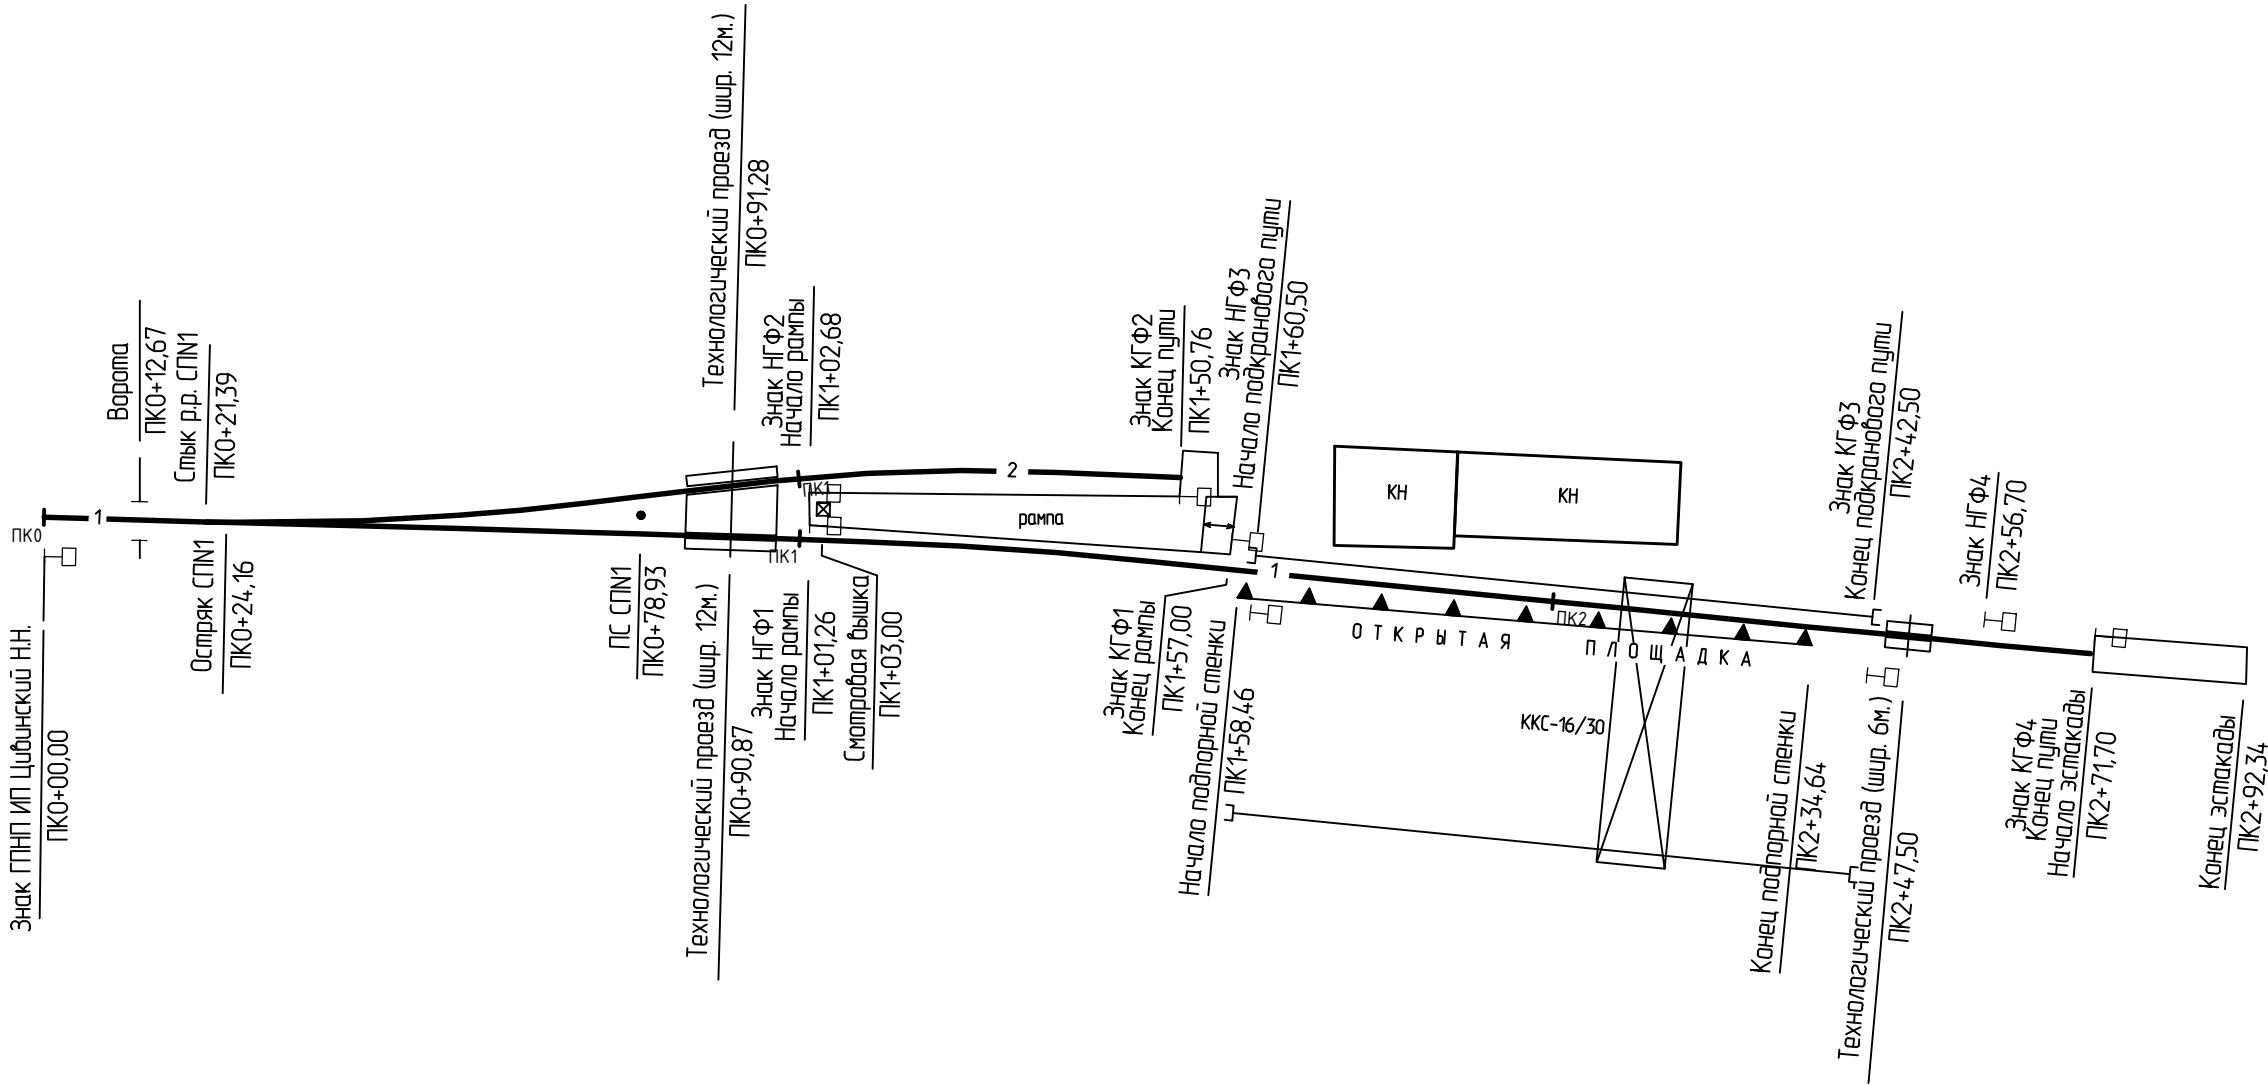

Примечание:


1. Инструментальная съемка железнодорожных путей необщего пользования N1,2 ИП Цивинский Н.Н. выполнена сотрудниками ООО "Забтранспроект" в августе 2023 года с использованием электронного тахеометра Leica TCR405.
2. Пикетаж разбит по оси пути N1 от знака ГПНП ПК0+00,00.


						2307-ТП-ГЧ			
Изм.	Кол.	Лист	Изд.	Подпись	Дата	Пути необщего пользования N1,2 ИП Цивинский Н.Н.			
Рук.работ		Афанасенко С.Н.		<i>Афанасенко</i>	08.23	Станция Чита-1	Стадия	Лист	Листов
Инженер		Егизарян Н.А.		<i>Егизарян</i>	08.23			1	3
						План путей №1, 2	ООО "Забтранспроект" 2023г.		
Н.контр.		Афанасенко С.Н.		<i>Афанасенко</i>	08.23				

Нестандартный пикет
Ситуация
Разница отметок фактических и спрямленных уклонов, см
Отметки головки рельсов по спрямленным уклонам, м
Длина, м
Спрямленные уклоны, %
Фактические уклоны, %
Фактические отметки головки рельсов, м
Отметки земляного полотна, м
Расстояния, м
Пикеты
План 1 пути
Километры

Примечание:

1. Инструментальная съемка железнодорожных путей необщего пользования №1,2 ИП Цивинский Н.Н. выполнена сотрудниками ООО «Забтранспроект» в августе 2023 года с использованием электронного тахеометра Leica TCR405.
2. Пикетаж разбит по оси пути №1 от знака ГПНП ПК0+00,00.
3. Система высот условная.

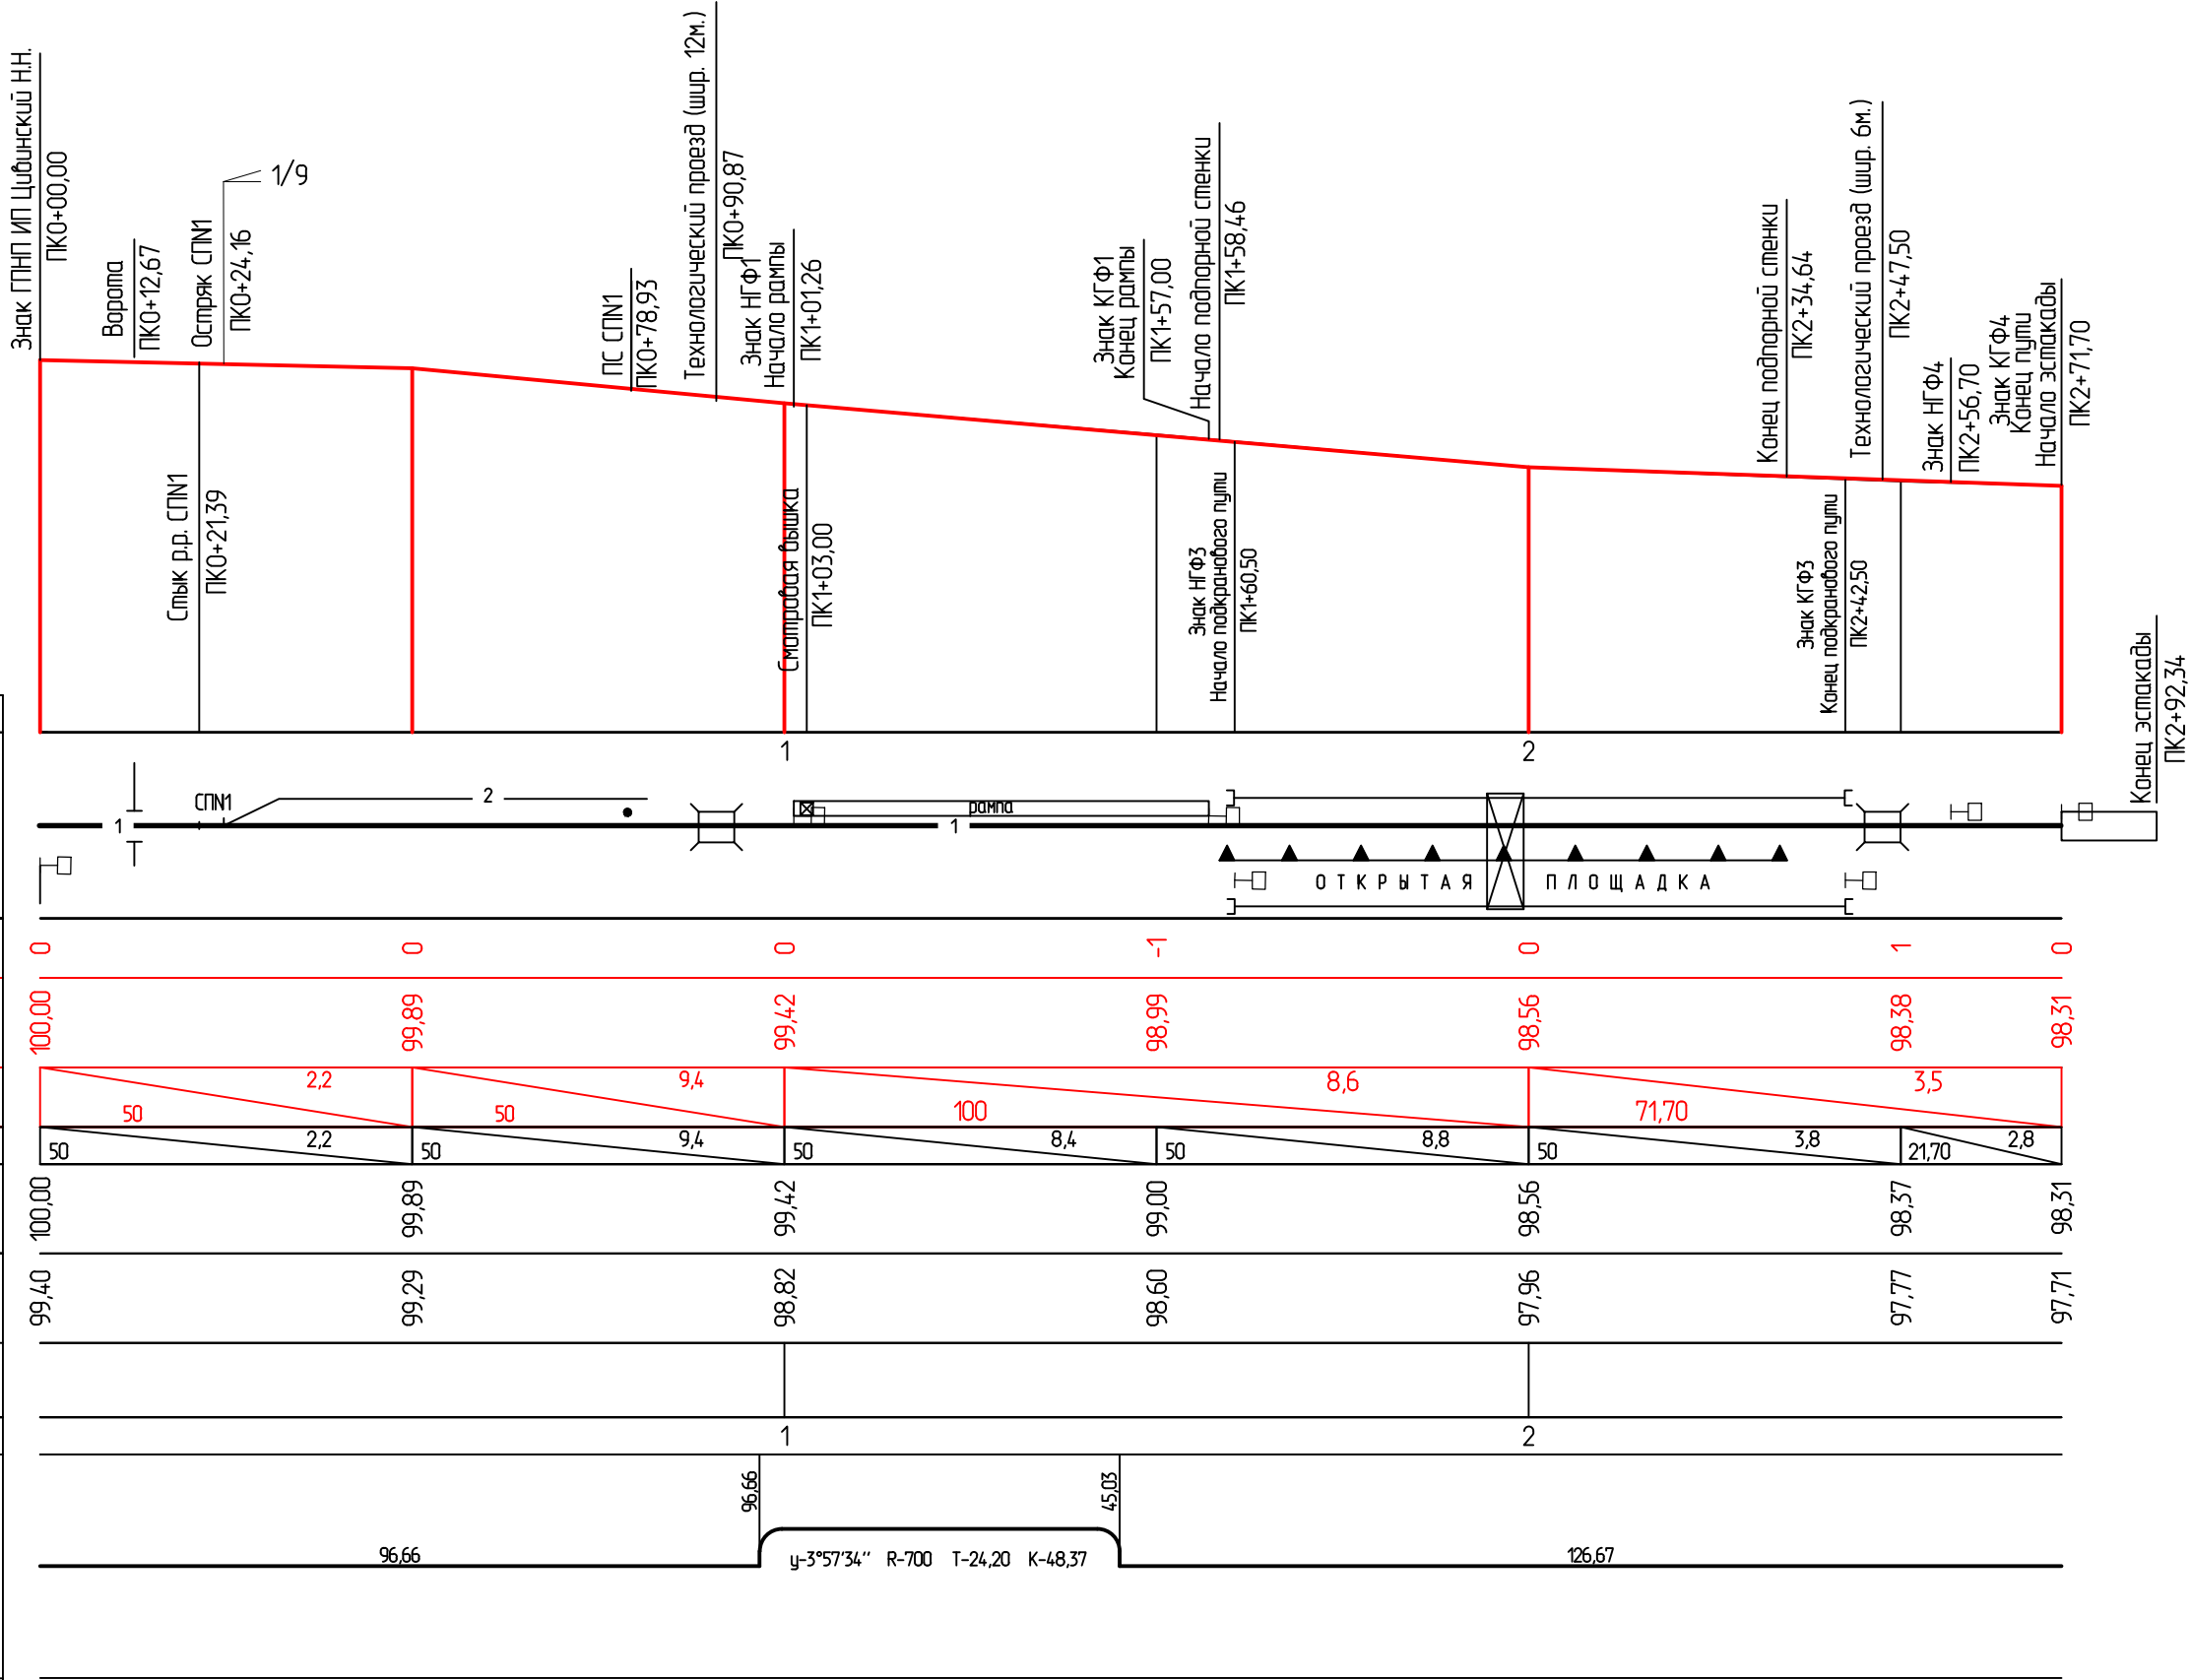


 						2307-ТП-ГЧ				
						Пути необщего пользования №1,2 ИП Цивинский Н.Н.				
Изм.	Кол.	Лист	Надк.	Подпись	Дата	Станция Чита-1		Стадия	Лист	Листов
Рук.работ		Афанасенко С.Н.			08.23				2	3
Инженер		Егизарян Н.А.			08.23	Продольный профиль пути №1		ООО "Забтранспроект" 2023г.		
						Продольный профиль пути №1		ООО "Забтранспроект" 2023г.		
Н.контр.		Афанасенко С.Н.			08.23					

Инф. N подл.	Подпись и дата	Взам. ин. N
2307		


Масштаб по горизонталі 1:1000
по вертикалі 1:100

Нестандартный пикет	
Ситуация	
Разница отметок фактических и спрямленных уклонов, см	
Отметки головки рельсов по спрямленным уклонам, м	
Длина, м	Спрямленные уклоны, ‰
Фактические уклоны, ‰	
Фактические отметки головки рельсов, м	
Отметки земляного полотна, м	
Расстояния, м	
Пикеты	
План 2 пути	
Километры	

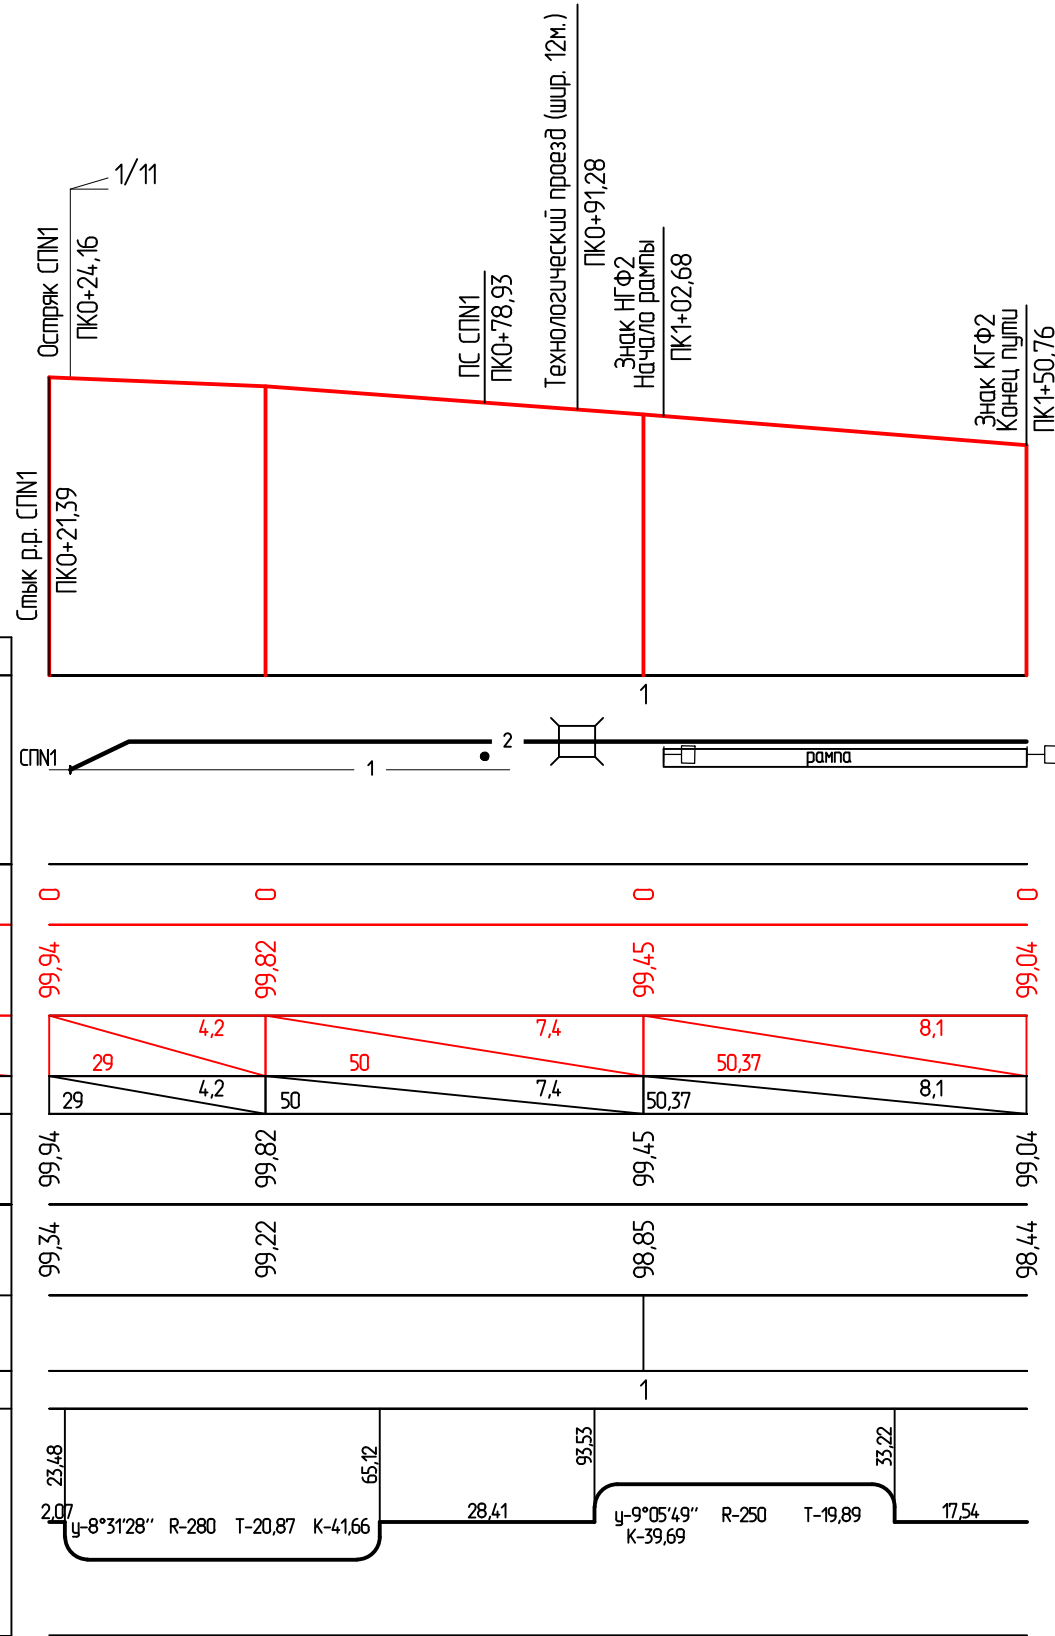

Примечание:

1. Инструментальная съемка железнодорожных путей необщего пользования №1,2 ИП Цивинский Н.Н. выполнена сотрудниками ООО «Забтранспроект» в августе 2023 года с использованием электронного тахеометра Leica TCR405.
2. Пикетаж разбит по оси пути №1 от знака ГПНП ПК0+00,00.
3. Система высот условная.

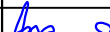						2307-ТП-ГЧ				
Изм.	Кол.	Лист	Изд.	Подпись	Дата	Пути необщего пользования N1,2 ИП Цивинский Н.Н.				
Рук.работ		Афанасенко С.Н.			08.23					
Инженер		Егизарян Н.А.			08.23	Станция Чита-1	Стадия	Лист	Листов	
								3	3	
						Продольный профиль пути №2	ООО "Забтранспроект" 2023г.			
Н.контр.		Афанасенко С.Н.			08.23					