



ОБЩЕСТВО С ОГРАНИЧЕННОЙ ОТВЕТСТВЕННОСТЬЮ
«ЗАБТРАНСПРОЕКТ»

Свидетельство № 1266 от 7 марта 2017 г.

СРО-И-032-22122011

ТЕХНИЧЕСКИЙ ПАСПОРТ

железнодорожных путей
необщего пользования
ООО «Русский экспорт»

Пути №71, 71а, МСУ 262-270

ст. Кадала

Главный инженер
ООО «Забтранспроект»

Афанасенко С.Н.

Ведущий инженер

Егиазарян Н.А.

Чита, 2022

Инв. № подл.	Подп. и дата	Взам. Инв. №
2206-ТП		

ОБЩИЕ СВЕДЕНИЯ

Место примыкания железнодорожного пути необщего пользования:

железнодорожные пути необщего пользования ООО «Русский экспорт» примыкают стрелочными переводами №260 и №262 к пути необщего пользования №25а АО «Хиагда» ст. Кадала.

Границы железнодорожного пути необщего пользования:

границей железнодорожных путей необщего пользования ООО «Русский экспорт» являются предельные столбики стрелочных переводов №260 (ПК0+62,65) и №262 (ПК2+85,15), напротив которых установлены знаки «Граница пути необщего пользования».

Наличие предохранительных устройств:

*колесосбрасывающий башмак №5СБ (ручной, сброс вправо) ПК1+16,36 на пути №71
колесосбрасывающий башмак №6СБ (ручной, сброс вправо) ПК3+16,33 на МСУ 262-270*

Дата заключения договора на эксплуатацию железнодорожного пути необщего пользования и срок его действия:

Порядок подачи и уборки вагонов (кем производится – железной дорогой, средствами предприятия или маневровым порядком), серия локомотива, применяемого при подаче и уборке вагонов:

подача и уборка вагонов на пути необщего пользования ООО «Русский экспорт» осуществляется маневровым порядком локомотивами серии ТЭМ2, ТЭМ2УМ, ТЭМ18ДМ ст. Кадала Забайкальской железной дороги.

Взам. Инв. №	
Подп. и дата	
Инв. № подл.	2206-ТП

							2206 – ТП			
Изм.	Кол.уч.	Лист	№ док.	Подп.	Дата					
Разработал		Егиазарян				Технический паспорт железнодорожных путей необщего пользования ООО «Русский экспорт»		Стадия	Лист	Листов
Проверил		Афанасенко						П	1	14
								ООО «Забтранспроект»		

1 ХАРАКТЕРИСТИКА ПУТИ

Таблица 1.1 – Примыкания других железнодорожных путей к железнодорожным путям предприятия

Наименование предприятия	Место примыкания (пикет, стрелка)	Длина путей км.	Предприятие, обслуживающее путь необщего пользования
-	-	-	-

Таблица 1.2 - Ведомость железнодорожных путей предприятия

№ пути	Граница путей		Специализация	Дата внесения изменений	Ф.И.О. должность внесшего изменения	Подпись
	от	до				
71	Знак ГПНП ПС СП№260 ПК0+62,65	Остряк СП№270 ПК3+66,27	Погрузочно-выгрузочный	07.2022	Афанасенко С.Н.	
71a	Остряк СП№270 ПК3+66,27	Упор ПК4+00,87	Погрузочно-выгрузочный, обгонный			
МСУ 262-270	ПС СП№262 ПК2+85,15	Остряк СП№270 ПК3+66,27	МСУ			

Таблица 1.3 - Данные по длине путей

№ пути	Граница путей		Длины путей, м		Дата внесения изменений	Ф.И.О. должность внесшего изменения	Подпись
	от	до	полная	полезная			
71	Знак ГПНП ПС СП№260 ПК0+62,65	Остряк СП№270 ПК3+66,27	303,62	254,48	07.2022	Афанасенко С.Н.	
71a	Остряк СП№270 ПК3+66,27	Упор ПК4+00,87	34,60	32,86			
МСУ 262-270	ПС СП№262 ПК2+85,15	Остряк СП№270 ПК3+66,27	81,12	-			
ИТОГО			419,34	287,34			

Взам. Инв. №	
Подп. и дата	
Инв. № подл.	2206-ТП

						2206-ТП		Лист
Изм.	Кол.уч.	Лист	№ док.	Подп.	Дата			2

2 НИЖНЕЕ СТРОЕНИЕ ПУТИ И ИСКУССТВЕННЫЕ СООРУЖЕНИЯ

Таблица 2.1 - Наличие насыпей или выемок

№ пути	Граница путей		Наличие выемок/насыпей	Дата внесения изменений	Ф.И.О. должность внесшего изменения	Подпись
	от пикета	до пикета				
71	Знак ГПНП ПС СП№260 ПК0+62,65	Остряк СП№270 ПК3+66,27	нет	07.2022	Афанасенко С.Н.	
71a	Остряк СП№270 ПК3+66,27	Упор ПК4+00,87	нет			
МСУ 262- 270	ПС СП№262 ПК2+85,15	Остряк СП№270 ПК3+66,27	нет			

Таблица 2.2 - Наличие водоотводных сооружений

№ пути	Граница путей		Водоотводное устройство право/лево	Дата внесения изменений	Ф.И.О. должность внесшего изменения	Подпись
	от пикета	до пикета				
71	Знак ГПНП ПС СП№260 ПК0+62,65	Остряк СП№270 ПК3+66,27	нет	07.2022	Афанасенко С.Н.	
71a	Остряк СП№270 ПК3+66,27	Упор ПК4+00,87				
МСУ 262- 270	ПС СП№262 ПК2+85,15	Остряк СП№270 ПК3+66,27				

Инв. № подл.	Подп. и дата	Взам. Инв. №
2206-ТП		

Изм.	Кол.уч.	Лист	№ док.	Подп.	Дата

2206 – ТП

Лист

3

Таблица 2.3 - Деформация земляного полотна

№ пути	Граница путей		Тип деформации право/лево	Дата внесения изменений	Ф.И.О. должность внесшего изменения	Подпись
	от пикета	до пикета				
71	Знак ГПНП ПС СП№260 ПК0+62,65	Остряк СП№270 ПК3+66,27	нет	07.2022	Афанасенко С.Н.	
71a	Остряк СП№270 ПК3+66,27	Упор ПК4+00,87				
МСУ 262- 270	ПС СП№262 ПК2+85,15	Остряк СП№270 ПК3+66,27				

Таблица 2.4 - Искусственные сооружения

№ пути	Граница путей		Вид искусствен-ного сооружения	Дата внесения изменений	Ф.И.О. должность внесшего изменения	Подпись
	от пикета	до пикета				
71	Знак ГПНП ПС СП№260 ПК0+62,65	Остряк СП№270 ПК3+66,27	нет	07.2022	Афанасенко С.Н.	
71a	Остряк СП№270 ПК3+66,27	Упор ПК4+00,87				
МСУ 262- 270	ПС СП№262 ПК2+85,15	Остряк СП№270 ПК3+66,27				

Таблица 2.5 - Пересечения с автомобильными дорогами

№ пути	от пикета	до пикета	Вид пересечения	Дата внесения изменений	Ф.И.О. должность внесшего изменения	Подпись
71	Знак ГПНП ПС СП№260 ПК0+62,65	Остряк СП№270 ПК3+66,27	нет	07.2022	Афанасенко С.Н.	
71a	Остряк СП№270 ПК3+66,27	Упор ПК4+00,87	нет			
МСУ 262- 270	ПС СП№262 ПК2+85,15	Остряк СП№270 ПК3+66,27	нет			

Инва. № подл.	Взам. Инв. №
2206-ТП	
Подп. и дата	
Изм.	Кол.уч.
Лист	№ док.
Подп.	Дата

3 ВЕРХНЕЕ СТРОЕНИЕ ПУТИ

Таблица 3.1 - Род балласта в балластном слое

№ пути	Граница путей		Род балласта	Дата внесения изменений	Ф.И.О. должность внесшего изменения	Подпись
	от пикета	до пикета				
71	Знак ГПНП ПС СП№260 ПК0+62,65	Остряк СП№270 ПК3+66,27	щебень	07.2022	Афанасенко С.Н.	
71a	Остряк СП№270 ПК3+66,27	Упор ПК4+00,87	щебень			
МСУ 262- 270	ПС СП№262 ПК2+85,15	Остряк СП№270 ПК3+66,27	щебень			

Таблица 3.2 - Толщина балластного слоя

№ пути	Граница путей		Толщина	Дата внесения изменений	Ф.И.О. должность внесшего изменения	Подпись
	от пикета	до пикета				
71	Знак ГПНП ПС СП№260 ПК0+62,65	Остряк СП№270 ПК3+66,27	до 20 см	07.2022	Афанасенко С.Н.	
71a	Остряк СП№270 ПК3+66,27	Упор ПК4+00,87	до 20 см			
МСУ 262- 270	ПС СП№262 ПК2+85,15	Остряк СП№270 ПК3+66,27	до 20 см			

Таблица 3.3 - Загрязнение балластного слоя

№ пути	Граница путей		Загрязнение	Дата внесения изменений	Ф.И.О. должность внесшего изменения	Подпись
	от пикета	до пикета				
71	Знак ГПНП ПС СП№260 ПК0+62,65	Остряк СП№270 ПК3+66,27	до 10%	07.2022	Афанасенко С.Н.	
71a	Остряк СП№270 ПК3+66,27	Упор ПК4+00,87	до 10%			
МСУ 262- 270	ПС СП№262 ПК2+85,15	Остряк СП№270 ПК3+66,27	до 10%			

Взам. Инв. №	
Подп. и дата	
Инв. № подл.	2206-ТП

Изм.	Кол.уч.	Лист	№ док.	Подп.	Дата	2206 – ТП	Лист
							5

Таблица 3.4 - Загрязняемость балластного слоя

№ пути	Граница путей		Загрязняе- мость	Дата внесения изменений	Ф.И.О. должность внесшего изменения	Подпись
	от пикета	до пикета				
71	Знак ГПНП ПС СП№260 ПК0+62,65	Остряк СП№270 ПК3+66,27	до 5%	07.2022	Афанасенко С.Н.	
71a	Остряк СП№270 ПК3+66,27	Упор ПК4+00,87	до 5%			
МСУ 262- 270	ПС СП№262 ПК2+85,15	Остряк СП№270 ПК3+66,27	до 5%			

Таблица 3.5 - Закрепление от угона

№ пути	Граница путей		Количество/ тип проти- воугонов	Дата внесения изменений	Ф.И.О. должность внесшего изменения	Подпись
	от пикета	до пикета				
71	Знак ГПНП ПС СП№260 ПК0+62,65	Остряк СП№270 ПК3+66,27	288 пар	07.2022	Афанасенко С.Н.	
71a	Остряк СП№270 ПК3+66,27	Упор ПК4+00,87	36 пар			
МСУ 262- 270	ПС СП№262 ПК2+85,15	Остряк СП№270 ПК3+66,27	108 пар			

Инв. № подл.	2206-ТП
Подп. и дата	
Взам. Инв. №	

Изм.	Кол.уч.	Лист	№ док.	Подп.	Дата

Таблица 3.6 - Этюра шпал, количество шпал в пути, материал шпал

№ пути	Граница путей		Эпюра, количество материал	Дата внесения изменений	Ф.И.О. должность внесшего изменения	Подпись
	от пикета	до пикета				
71	<i>Шпалы – эпюра 1840 шп/км</i>			07.2022	Афанасенко С.Н.	
	Знак ГПНП ПС СП№260 ПК0+62,65	Остряк СП№270 ПК3+66,27	497 шп – дер			
71а	<i>Шпалы – эпюра 1840 шп/км</i>					
	Остряк СП№270 ПК3+66,27	Упор ПК4+00,87	63 шп - дер			
МСУ 262- 270	<i>Шпалы – эпюра 1840 шп/км</i>					
	ПС СП№262 ПК2+85,15	Остряк СП№270 ПК3+66,27	93 шп - дер			
<i>Итого</i>		<i>Шпалы: дер – 653 шп</i>				

Инв. № подл.	Подп. и дата	Взам. Инв. №
2206-ТП		

Изм.	Кол.уч.	Лист	№ док.	Подп.	Дата

2206 – ТП

Лист

7

Таблица 3.7 - Тип рельсов

№ пути	Граница путей		Тип рельсов, длина, м.	Дата внесения изменений	Ф.И.О. должность внесшего изменения	Подпись
	от пикета	до пикета				
71	Знак ГПНП ПС СП№260 ПК0+62,65	Остряк СП№270 ПК3+66,27	Р65 – 303,62м x 2	07.2022	Афанасенко С.Н.	
71а	Остряк СП№270 ПК3+66,27	Упор ПК4+00,87	Р65 – 34,60м x 2			
МСУ 262- 270	ПС СП№262 ПК2+85,15	Остряк СП№270 ПК3+66,27	Р65 – 81,12м x 2			
Итого		Р65 – 838,68м.				

Таблица 3.8 - Наличие сварных стыков

№ пути	Граница путей		Наличие сварных стыков	Дата внесения изменений	Ф.И.О. должность внесшего изменения	Подпись
	от пикета	до пикета				
71	Знак ГПНП ПС СП№260 ПК0+62,65	Остряк СП№270 ПК3+66,27	нет	07.2022	Афанасенко С.Н.	
71а	Остряк СП№270 ПК3+66,27	Упор ПК4+00,87	нет			
МСУ 262- 270	ПС СП№262 ПК2+85,15	Остряк СП№270 ПК3+66,27	нет			

Инв. № подл.	Подп. и дата	Взам. Инв. №
2206-ТП		

Изм.	Кол.уч.	Лист	№ док.	Подп.	Дата

2206 – ТП

Лист

8

Таблица 3.9 - Ведомость стрелочных переводов

№ Стрелочного перевода	Вид стрелочного перевода, отклонение	Тип и марка стрелочного перевода	Полная длина, м	Дата внесения изменений	Ф.И.О. должность внесшего изменения	Подпись
270	Обыкновенный, правосторонний, ручной	1/11 Р65	33,36	07.2022	Афанасенко С.Н.	

Таблица 3.10 - Верхнее строение пути на стрелочных переводах

№ стрелочного перевода	Тип рельсов	Подрельсовое основание		Вид балласта	Дата внесения изменений	Ф.И.О. должность внесшего изменения	Подпись
		Шпалы	Брус				
270	Р65	13	80	Щебень	07.2022	Афанасенко С.Н.	

Таблица 3.11 - Стыковые скрепления

№ пути	Накладки		Количество стыковых болтов	Дата внесения изменений	Ф.И.О. должность внесшего изменения	Подпись
	тип	Кол-во				
71	Двухголовые Р65	52	104	07.2022	Афанасенко С.Н.	
71а	Двухголовые Р65	12	24			
МСУ 262- 270	Двухголовые Р65	28	56			
	Итого	92	184			

Инв. № подл.	2206-ТП
Подп. и дата	
Взам. Инв. №	

Изм.	Кол.уч.	Лист	№ док.	Подп.	Дата

2206 – ТП

Лист

9

Таблица 3.12 - Промежуточные скрепления

№ пути	Промежуточное скрепление		Дата внесения изменений	Ф.И.О. должность внесшего изменения	Подпись
	Подкладки, шт	Прикрепители, шт			
71	Д-65 – 994	Костыли – 3976	07.2022	Афанасенко С.Н.	
71a	Д-65 – 126	Костыли – 504			
МСУ 262-270	Д-65 – 186	Костыли – 744			
Итого	1306	5224			

Инв. № подл.	Подп. и дата	Взам. Инв. №
2206-ТП		

Изм.	Кол.уч.	Лист	№ док.	Подп.	Дата

2206 – ТП

Лист

10

4 ТЕХНИЧЕСКОЕ ОСНАЩЕНИЕ ГРУЗОВОГО ФРОНТА

Наличие договора на подачу/уборку вагонов: _____

Наличие лицензии: _____

Наличие таможенных складов временного хранения: _____

Таблица 4.1 - Вместимость грузовых фронтов

№ грузового фронта	Наименование. грузового фронта	Местоположение			Длина, м.	Вместимость, усл. ваг.
		№ пути	от пикета	до пикета		
ГФ1	Открытая площадка	71	ПК1+17,36	ПК1+60,00	42,64	2 кр.
ГФ2	Рампа	71	ПК1+60,00	ПК3+17,13	157,13	11 пв.
ГФ3	Рампа	71а	ПК3+68,01	ПК4+00,87	32,86	2 пв.

Технико-технологическая характеристика грузовых фронтов:

ГФ1 – открытая площадка

Среднесуточный вагонооборот – 1 вагон.

Перечень перерабатываемых грузов – погрузка: пиломатериал, тарно-штучные грузы.

Перечень перерабатываемых опасных грузов – нет.

Средства механизации – вилочный погрузчик, грузоподъемностью 3,5т – 2 шт.

ГФ2 – рампа

Среднесуточный вагонооборот – 11 вагонов.

Перечень перерабатываемых грузов – погрузка: уголь.

Перечень перерабатываемых опасных грузов – нет.

Средства механизации – погрузчик ковшовый, объем ковша 5м³ – 4 шт.

ГФ3 – рампа

Среднесуточный вагонооборот – 1 вагон.

Перечень перерабатываемых грузов – погрузка: уголь.

Перечень перерабатываемых опасных грузов – нет.

Средства механизации – погрузчик ковшовый, объем ковша 5м³ – 1 шт.

Технический паспорт составлен на основании имеющихся документов и результатов инструментальной съемки и фактического состояния пути.

Данный технический паспорт предназначен только для разработки инструкции «О порядке обслуживания и организации движения на железнодорожном пути необщего пользования ООО «Русский экспорт»

Данный технический паспорт не устанавливает права собственности на железнодорожные пути, стрелочные переводы.

Главный инженер

Взам. Инв. №	
Подп. и дата	
Инв. № подл.	2206-ТП

Изм.	Кол.уч.	Лист	№ док.	Подп.	Дата	2206 – ТП	Лист
							11

ПРИЛОЖЕНИЕ

Свидетельства о допуске к работам в области инженерных изысканий, которые оказывают влияние на безопасность объектов капитального строительства

Саморегулируемая организация
основанная на членстве лиц, осуществляющих изыскания
(вид саморегулируемой организации)

АССОЦИАЦИЯ ИНЖЕНЕРОВ-ИЗЫСКАТЕЛЕЙ
«Инженерная подготовка нефтегазовых комплексов»
192012, г. Санкт-Петербург, пер. 3-й Рабфакровский, д. 5,
корп. 4, литер А, оф. 4.11,
www.ingneft.ru
№ СРО-И-032-22122011

Санкт - Петербург
(место выдачи Свидетельства)

«07» марта 2017г.
(дата выдачи Свидетельства)

СВИДЕТЕЛЬСТВО
о допуске к определённому виду или видам работ, которые
оказывают влияние на безопасность объектов капитального
строительства
№ 1266

Выдано члену саморегулируемой организации

Общество с ограниченной ответственностью «Забтранспроект»,
ОГРН 1127536004012, ИНН 7536127844,
672039, Забайкальский край, г.Чита, ул.Красноярская, дом 31, пом.47

Основание выдачи Свидетельства: решение Контрольно-дисциплинарного комитета
(наименование органа управления саморегулируемой организацией,
АС «Инженерная подготовка нефтегазовых комплексов»
№ 7КДК от 07 марта 2017г.
номер протокола, дата заседания)

Настоящим Свидетельством подтверждается допуск к работам, указанным в
приложении к настоящему Свидетельству, которые оказывают влияние на
безопасность объектов капитального строительства.
Начало действия с «07» марта 2017г.
Свидетельство без приложения не действительно.
Свидетельство выдано без ограничения срока и территории его действия.
Свидетельство выдано взамен ранее выданного № 147 от 26 июля 2012г.
(дата выдачи, номер Свидетельства)

Генеральный директор
АС «Инженерная подготовка
нефтегазовых комплексов»
(должность, наименование лица)

Артекин Н.Ф.
(инициалы, фамилия)



Инв. № подл.	2206-ТП
Подп. и дата	
Взам. Инв. №	

Изм.	Кол.уч.	Лист	№ док.	Подп.	Дата

ПРИЛОЖЕНИЕ

к Свидетельству о допуске к
определённому виду или видам работ,
которые оказывают влияние на
безопасность объектов капитального
строительства
от «07» марта 2017г.
№ 1266

Виды работ, которые оказывают влияние на безопасность:

1. объектов капитального строительства, включая особо опасные и технически сложные объекты капитального строительства, объекты использования атомной энергии, и о допуске к которым член АС «Инженерная подготовка нефтегазовых комплексов» Общество с ограниченной ответственностью «Забтранспроект», ИНН 7536127844 имеет Свидетельство

№ пп	Наименование вида работ
	НЕТ

2. объектов капитального строительства, включая особо опасные и технически сложные объекты капитального строительства (кроме объектов использования атомной энергии) и о допуске к которым член АС «Инженерная подготовка нефтегазовых комплексов» Общество с ограниченной ответственностью «Забтранспроект», ИНН 7536127844 имеет Свидетельство

№ пп	Наименование вида работ
1.	РАБОТЫ В СОСТАВЕ ИНЖЕНЕРНО-ГЕОДЕЗИЧЕСКИХ ИЗЫСКАНИЙ
1.1.	Создание опорных геодезических сетей.
1.2.	Геодезические наблюдения за деформациями и осадками зданий и сооружений, движениями земной поверхности и опасными природными процессами.
1.3.	Создание и обновление инженерно-топографических планов в масштабах 1:200 – 1:5000, в том числе в цифровой форме, съемка подземных коммуникаций и сооружений.
1.4.	Трассирование линейных объектов.
1.5.	Инженерно-гидрографические работы.
1.6.	Специальные геодезические и топографические работы при строительстве и реконструкции зданий и сооружений.
2.	РАБОТЫ В СОСТАВЕ ИНЖЕНЕРНО-ГЕОЛОГИЧЕСКИХ ИЗЫСКАНИЙ
2.1.	Инженерно-геологическая съемка в масштабах 1:500 – 1:25000.
2.2.	Проходка горных выработок с их опробованием, лабораторные исследования физико-механических свойств грунтов и химических свойств проб подземных вод.
2.3.	Изучение опасных геологических и инженерно-геологических процессов с разработкой рекомендаций по инженерной защите территории.
2.4.	Гидрогеологические исследования.
2.5.	Инженерно-геофизические исследования.
2.6.	Инженерно-геокриологические исследования.
2.7.	Сейсмологические и сейсмостектонические исследования территории, сейсмическое микрорайонирование.
3.	РАБОТЫ В СОСТАВЕ ИНЖЕНЕРНО-ГИДРОМЕТЕОРОЛОГИЧЕСКИХ ИЗЫСКАНИЙ
3.1.	Метеорологические наблюдения и изучение гидрологического режима водных объектов.
3.2.	Изучение опасных гидрометеорологических процессов и явлений с расчетами их

Инв. № подл.	Подп. и дата	Взам. Инв. №
2206-ТП		

Изм.	Кол.уч.	Лист	№ док.	Подп.	Дата

	характеристик.
3.3.	Изучение русловых процессов водных объектов, деформаций и переработки берегов.
3.4.	Исследования ледового режима водных объектов.
4.	РАБОТЫ В СОСТАВЕ ИНЖЕНЕРНО-ЭКОЛОГИЧЕСКИХ ИЗЫСКАНИЙ
4.1.	Инженерно-экологическая съемка территории.
4.2.	Исследования химического загрязнения почвогрунтов, поверхностных и подземных вод, атмосферного воздуха, источников загрязнения.
4.3.	Лабораторные химико-аналитические и газохимические исследования образцов и проб почвогрунтов и воды.
4.4.	Исследования и оценка физических воздействий и радиационной обстановки на территории.
4.5.	Изучение растительности, животного мира, санитарно-эпидемиологические и медико-биологические исследования территории*
5.	РАБОТЫ В СОСТАВЕ ИНЖЕНЕРНО-ГЕОТЕХНИЧЕСКИХ ИЗЫСКАНИЙ (ВЫПОЛНЯЮТСЯ В СОСТАВЕ ИНЖЕНЕРНО-ГЕОЛОГИЧЕСКИХ ИЗЫСКАНИЙ ИЛИ ОТДЕЛЬНО НА ИЗУЧЕННОЙ В ИНЖЕНЕРНО-ГЕОЛОГИЧЕСКОМ ОТНОШЕНИИ ТЕРРИТОРИИ ПОД ОТДЕЛЬНЫЕ ЗДАНИЯ И СООРУЖЕНИЯ)
5.1.	Проходка горных выработок с их опробованием и лабораторные исследования механических свойств грунтов с определением характеристик для конкретных схем расчета оснований фундаментов.
5.2.	Полевые испытания грунтов с определением их стандартных прочностных и деформационных характеристик (штамповые, сдвиговые, прессиометрические, срезные). Испытания эталонных и натурных свай.
5.3.	Определение стандартных механических характеристик грунтов методами статического, динамического и бурового зондирования.
5.4.	Физическое и математическое моделирование взаимодействия зданий и сооружений с геологической средой.
5.5.	Специальные исследования характеристик грунтов по отдельным программам для нестандартных, в том числе нелинейных методов расчета оснований фундаментов и конструкций зданий и сооружений.
5.6.	Геотехнический контроль строительства зданий, сооружений и прилегающих территорий.
6.	Обследование состояния грунтов основания зданий и сооружений.

3. объектов капитального строительства (кроме особо опасных и технически сложных объектов, объектов использования атомной энергии) и о допуске к которым член АС «Инженерная подготовка нефтегазовых комплексов» Общество с ограниченной ответственностью «Забтранспроект», ИНН 7536127844 имеет Свидетельство

№ пп	Наименование вида работ
	НЕТ

Общество с ограниченной ответственностью «Забтранспроект» вправе заключать договоры по осуществлению организации работ в области инженерных изысканий, которые оказывают влияние на безопасность объектов капитального строительства.

Генеральный директор
АС «Инженерная подготовка
нефтегазовых комплексов»
должность



Артемкин Н.Ф.
фамилия, инициалы

Инв. № подл.	2206-ТП
Подп. и дата	
Взам. Инв. №	

Изм.	Кол.уч.	Лист	№ док.	Подп.	Дата

Взам. инв. N	
Подпись и дата	
Инв. N подл.	

Ведомость стрелочных переводов



N стр. перевода	Вид стрелочного перевода, отклонения	Марка крестовины	Полная длина, м
СП N270	Обыкновенный, нецентрализованный, правый	1/11 Р65	33,36

Ведомость габаритов

Номер	Тип сооружения	Путь	Пикет	Габарит лево/право
1	Ворота	71	ПК1+08,87	3,32/3,36
2	Начало рампы	71	ПК1+60,00	2,20/ -
3	Конец рампы	71а	ПК4+00,87	2,00/ -
4	Ворота	МСУ	ПК3+01,29	2,87/3,80


Примечание:

- 1.Технический паспорт железнодорожных путей необщего пользования ООО "Русский экспорт" составлен по материалам инструментальной съемки, выполненной сотрудниками Забтранспроект в июле 2022г с использованием электронного тахеометра Leica TC405.
- 2.Пикетаж разбит по оси пути N71 от стрелочного перевода №260.

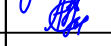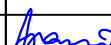
						2206-ТП-ГЧ			
Изм.	Кол.	Лист	Изд.	Подпись	Дата	Пути необщего пользования N71, 71а, МСУ 262-270 ООО "Русский экспорт"			
Рук.работ		Афанасенко С.Н.			08.22	ст. Кадала		Стадия	Лист
Инженер		Егизарян Н.А.			08.22			РП	1
						План путей		ООО "Забтранспроект" 2022г.	
Н.контр.		Афанасенко С.Н.			08.22				
								Листов	3

Ведомость ж.д. путей

№ пути	Наименование пути	Длина пути		Граница пути	
		полная	полезная	от	до
71	Погрузочно-выгрузочный	303,62	254,45	Знак ГПП ПС СП260 ПК0+62,65	Остряк СП270 ПК3+66,27
71а	Погрузочно-выгрузочный, обгонный	34,60	32,86	Остряк СП№270 ПК3+66,27	Упор ПК4+00,87
МСУ 262-270	МСУ	81,12	-	ПС СП№262 ПК2+85,15	Остряк СП№270 ПК3+66,27

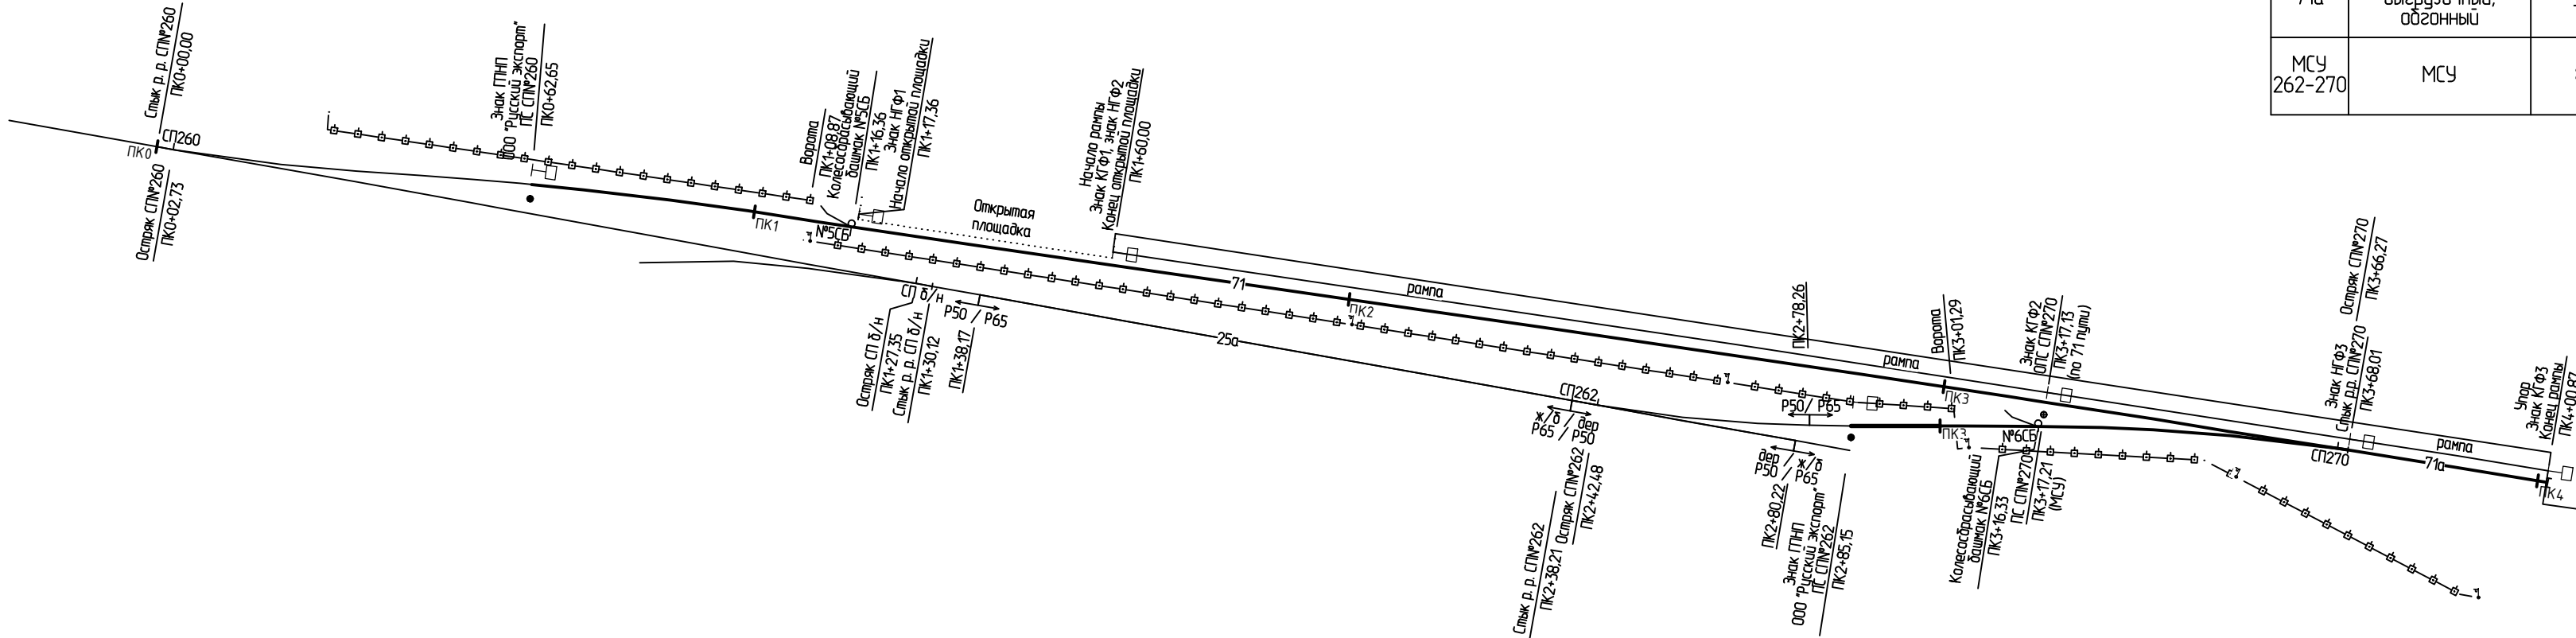

Масштаб по горизонтали 1:1000 по вертикали 1:100
Нестандартный пикет
Ситуация
Разница отметок фактических и спрямленных уклонов, см
Отметки головки рельсов по спрямленным уклонам, м
Длина, м
Спрямленные уклоны, %
Фактические уклоны, %
Фактические отметки головки рельсов, м
Отметки земляного полотна, м
Расстояния, м
Пикеты
План пути
Километры

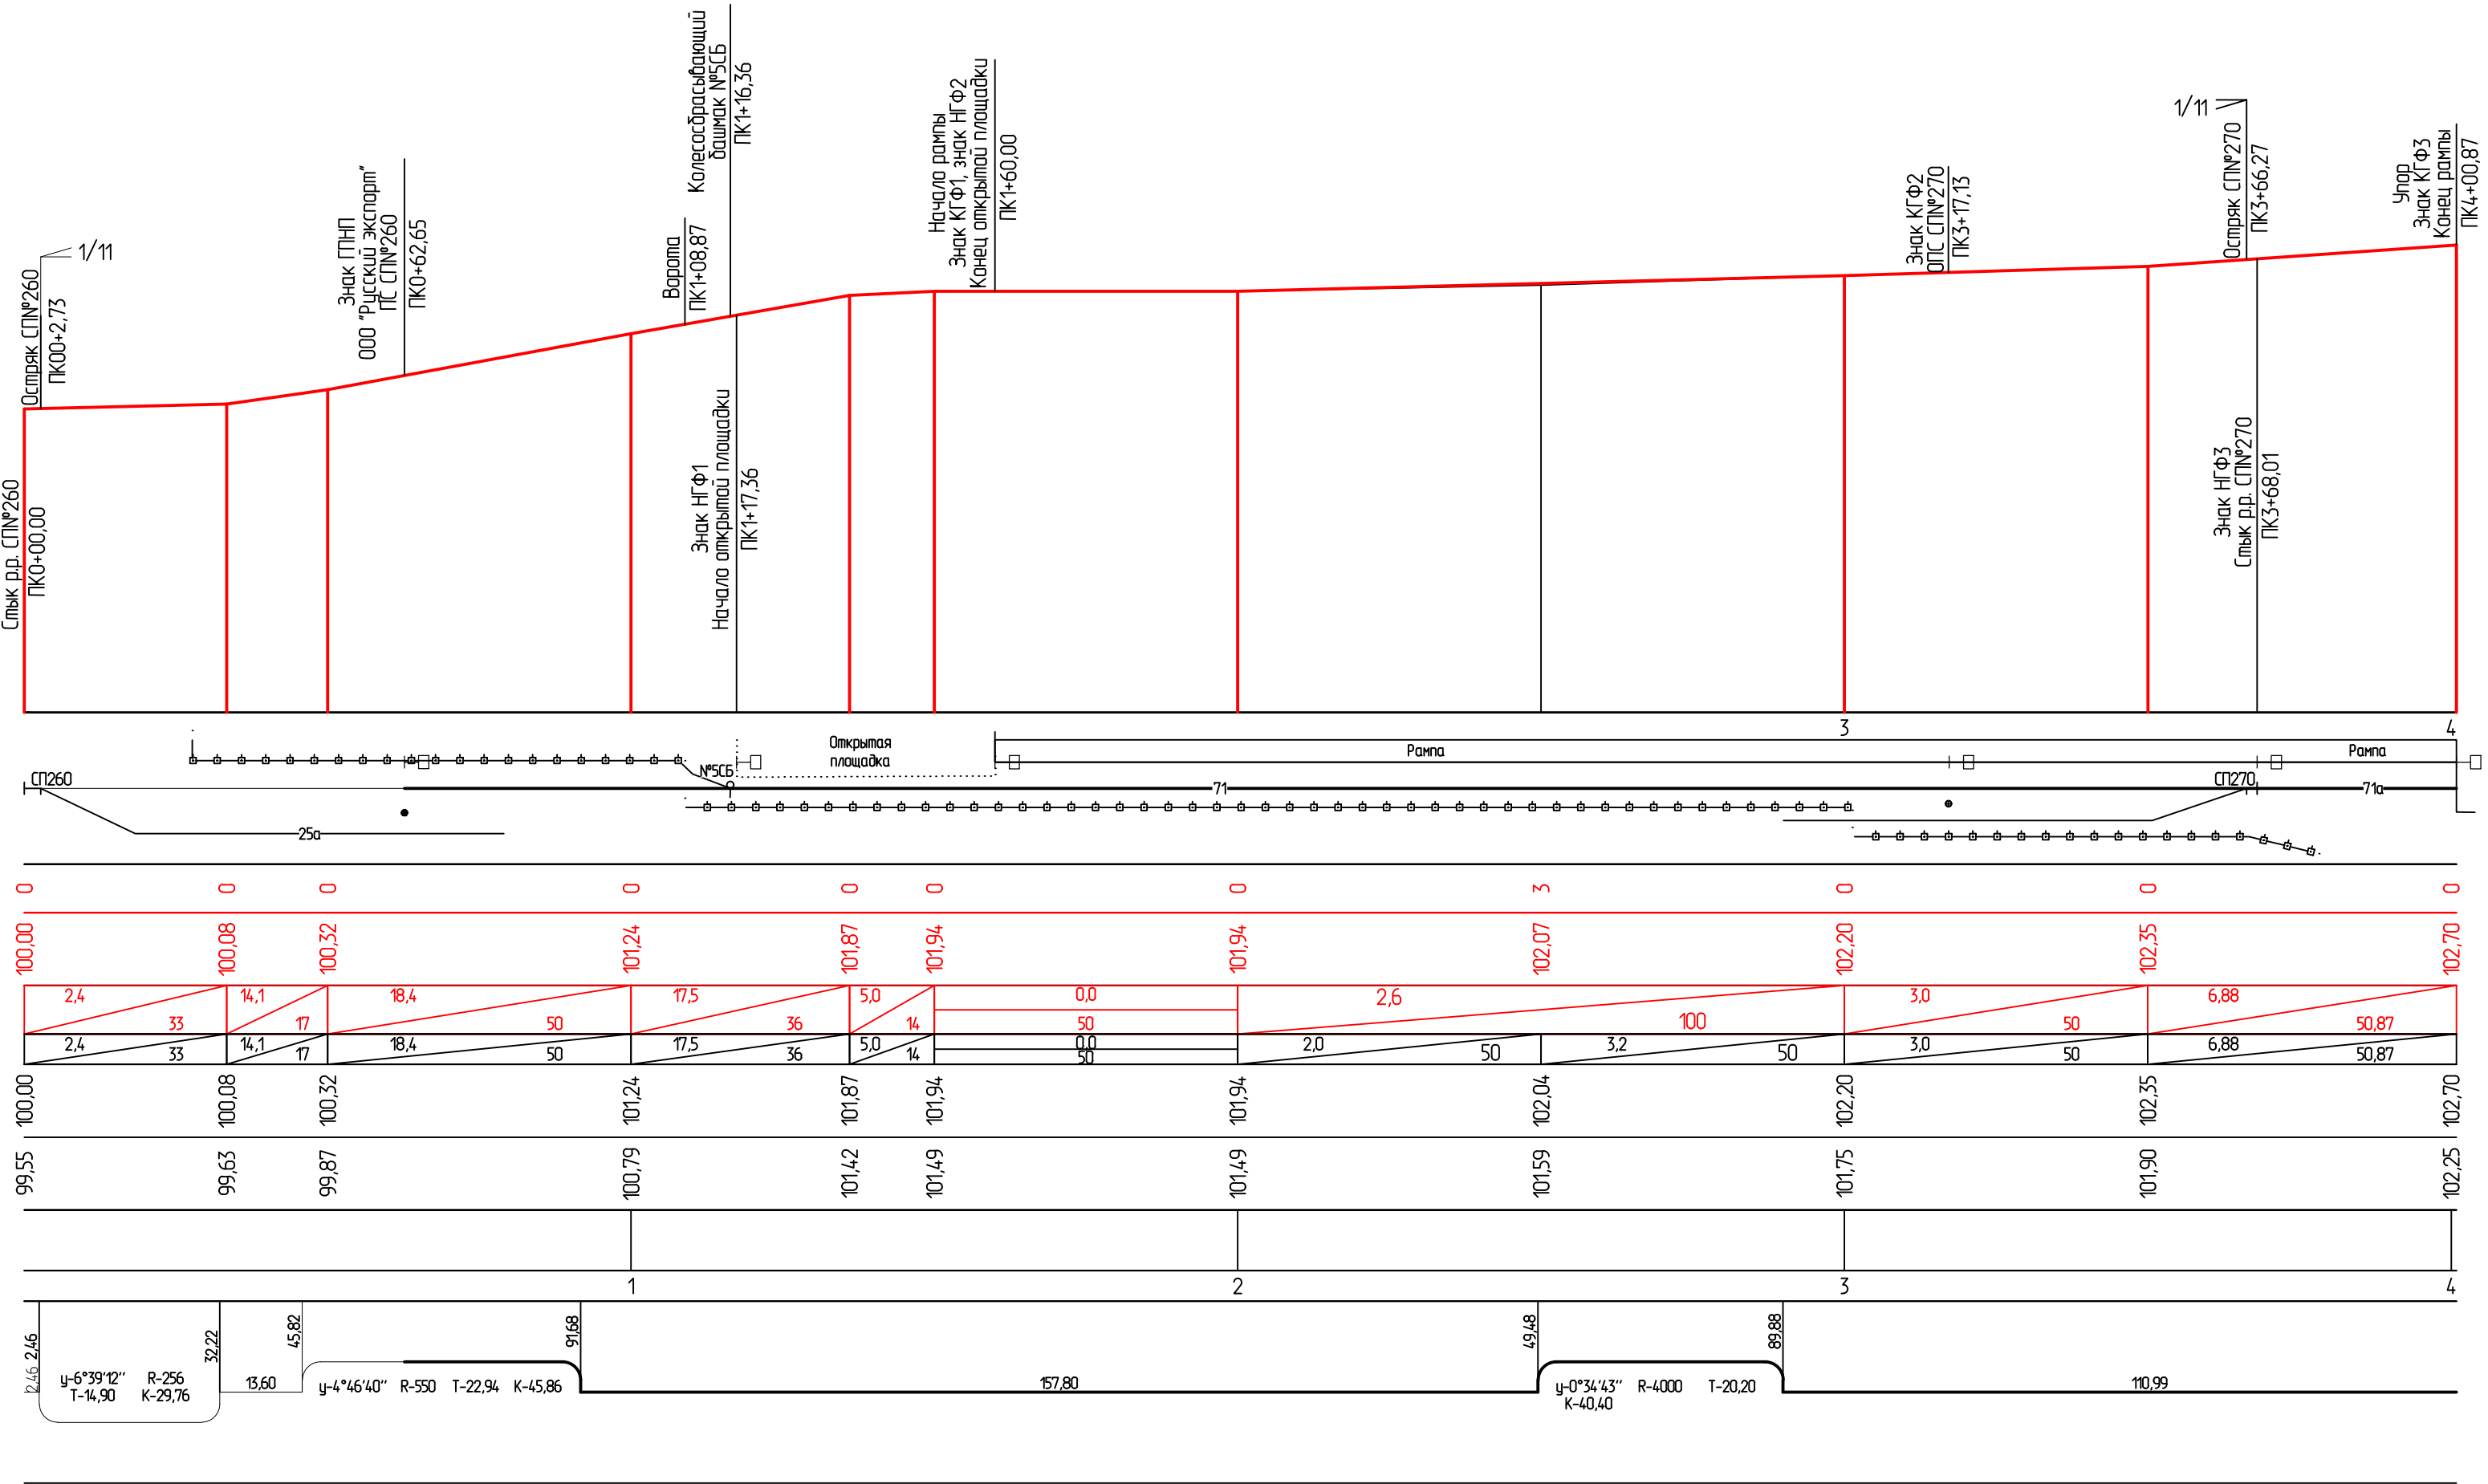


Примечание:

1. Технический паспорт железнодорожных путей необщего пользования ООО "Русский экспорт" составлен по материалам инструментальной съемки, выполненной сотрудниками Забтранспроект в июле 2022г с использованием электронного тахеометра Leica TCR405.
2. Пикетаж разбит по оси пути N71 от стрелочного перевода N260.
3. Система высот условная.

						2206-ТП-ГЧ
Изм.	Кол.	Лист	Ндэк.	Подпись	Дата	Пути необщего пользования N71, 71а, МСУ 262-270 ООО "Русский экспорт"
Рук.работ	Афанасенко С.Н.	08.22				
Инженер	Егизарян Н.А.	08.22				ст. Кадала
						РП
						2
						3
Н.контр.	Афанасенко С.Н.	08.22				Продольный профиль путей N71, 71а
						ООО "Забтранспроект" 2022г.

Масштаб по горизонтали 1:1000 по вертикали 1:100	
Нестандартный пикет	
Ситуация	
Разница отметок фактических и спрямленных уклонов, см	
Отметки головки рельсов по спрямленным уклонам, м	
Длина, м	Спрямленные уклоны, ‰
Фактические уклоны, ‰	
Фактические отметки головки рельсов, м	
Отметки земляного полотна, м	
Расстояния, м	
Пикеты	
План пути	
Километры	

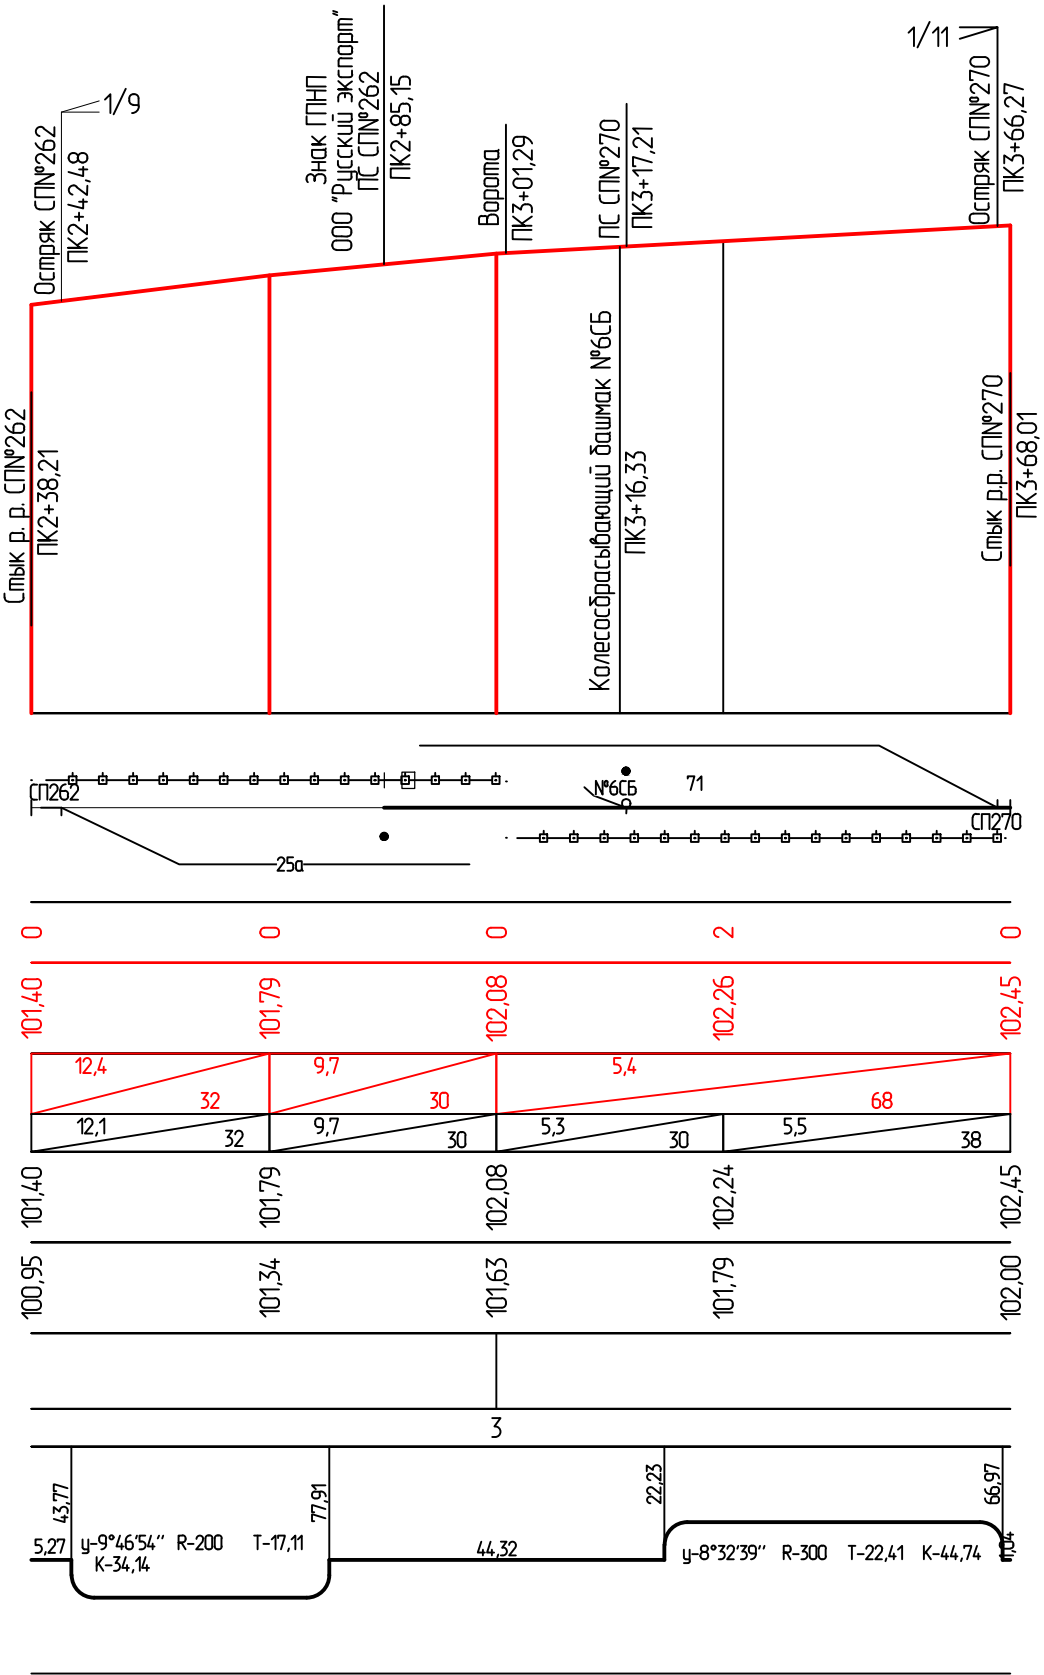

Примечание:

- Технический паспорт железнодорожных путей необщего пользования ООО "Русский экспорт" составлен по материалам инструментальной съемки, выполненной сотрудниками Забтранспроект в июле 2022г с использованием электронного тахеометра Leica TCR405.
- Пикетаж разбит по оси пути N71 от стрелочного перевода №260.
- Система высот условная.

						2206-ТП-ГЧ			
						Пути необщего пользования N71, 71а, МСУ 262-270 ООО "Русский экспорт"			
Изм.	Кол.	Лист	Ндк.	Подпись	Дата	ст. Кадала	Стадия	Лист	Листов
Рук.работ		Афанасенко С.Н.		<i>Афанасенко С.Н.</i>	08.22		РП	3	3
Инженер		Егизарян Н.А.		<i>Егизарян Н.А.</i>	08.22	Продольный профиль МСУ 262 -270	ООО "Забтранспроект" 2022г.		
Н.контр.		Афанасенко С.Н.		<i>Афанасенко С.Н.</i>	08.22				